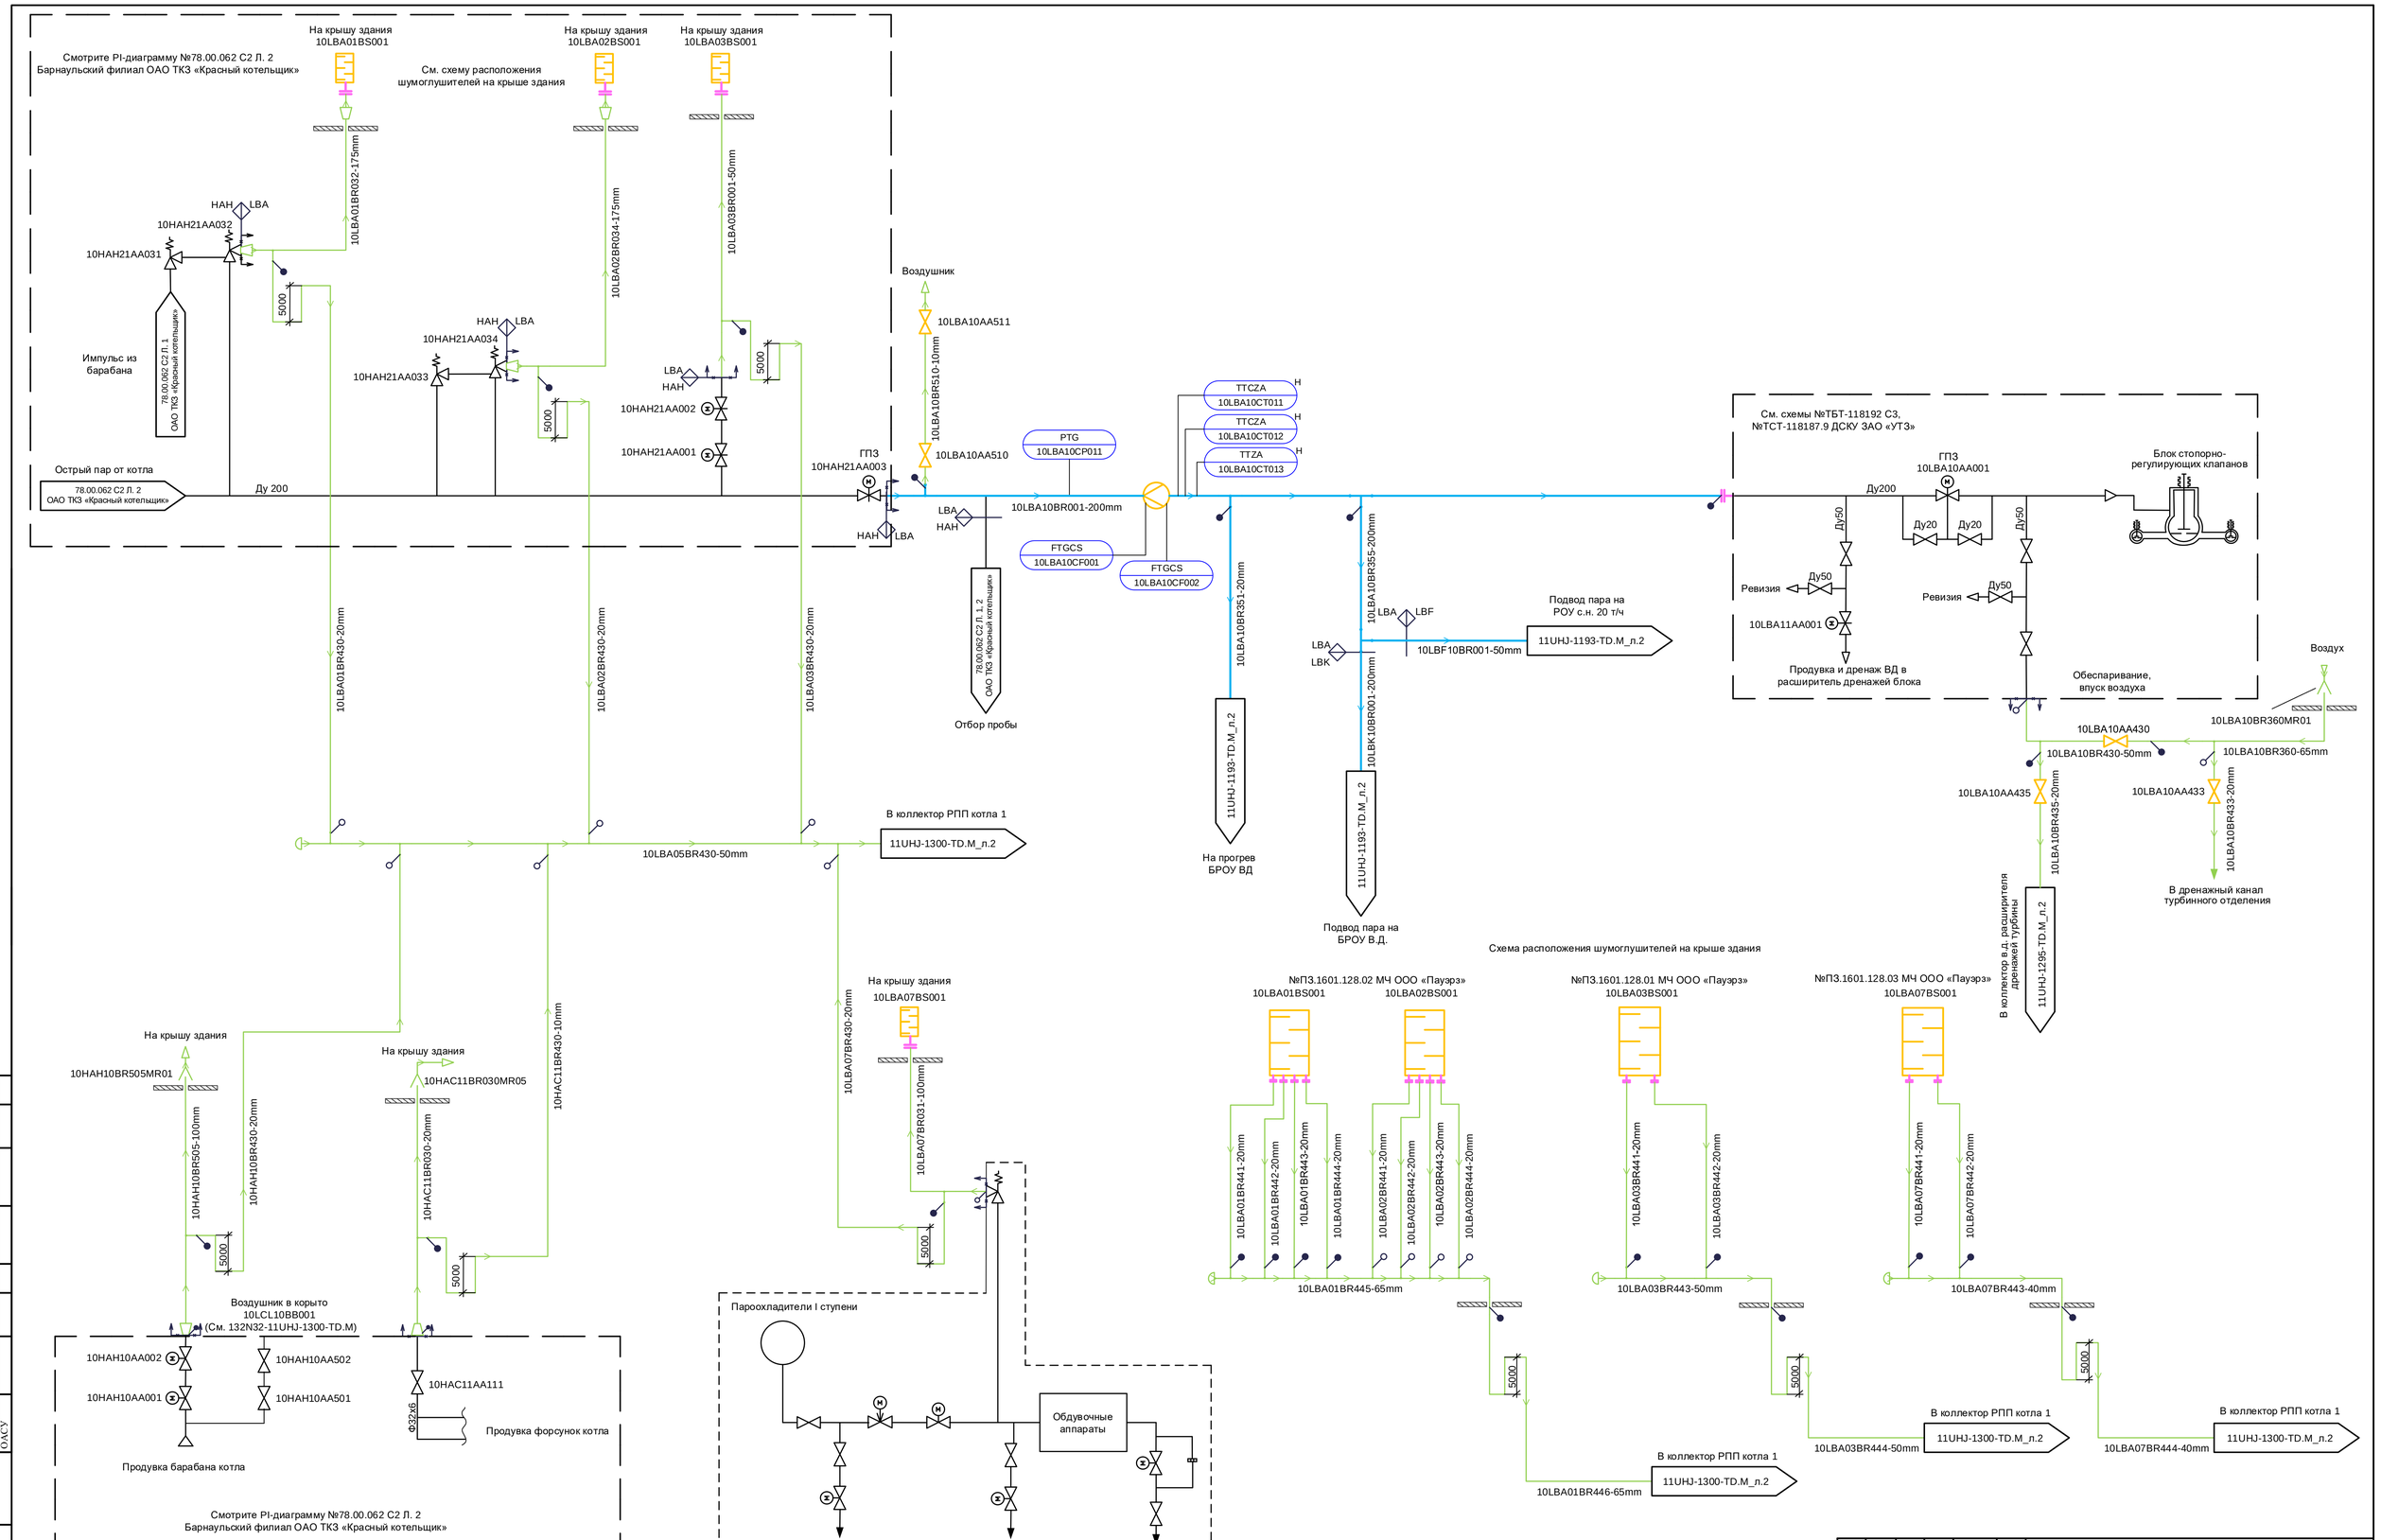

1	-	Зам.	474-16			
Изм.	Кол.уч	Лист	№ док.	Подп.	Дата	
Разработал		Калинкина				
Проверил		Бобров				
Гл. спец.		Бакатин				
Н. контр.		Гридчина				

132N32-11UHJ-1143-TD.M

Строительство Сахалинской ГРЭС-2. Основной производственный комплекс. Внутриплощадочные объекты (1очередь)

Главный корпус. PI-диаграмма трубопроводов острого пара

PI-диаграмма трубопроводов острого пара. Система LBA

Стадия	Лист	Листов
Р	2	

АКЦИОНЕРНОЕ ОБЩЕСТВО ИНСТИТУТ ТЕПЛОЭЛЕКТРОПРОЕКТ г. МОСКВА

Согласовано

ОАСУ

Взам. инв. №

Подпись и дата

Инв. № подл.

Формат А1