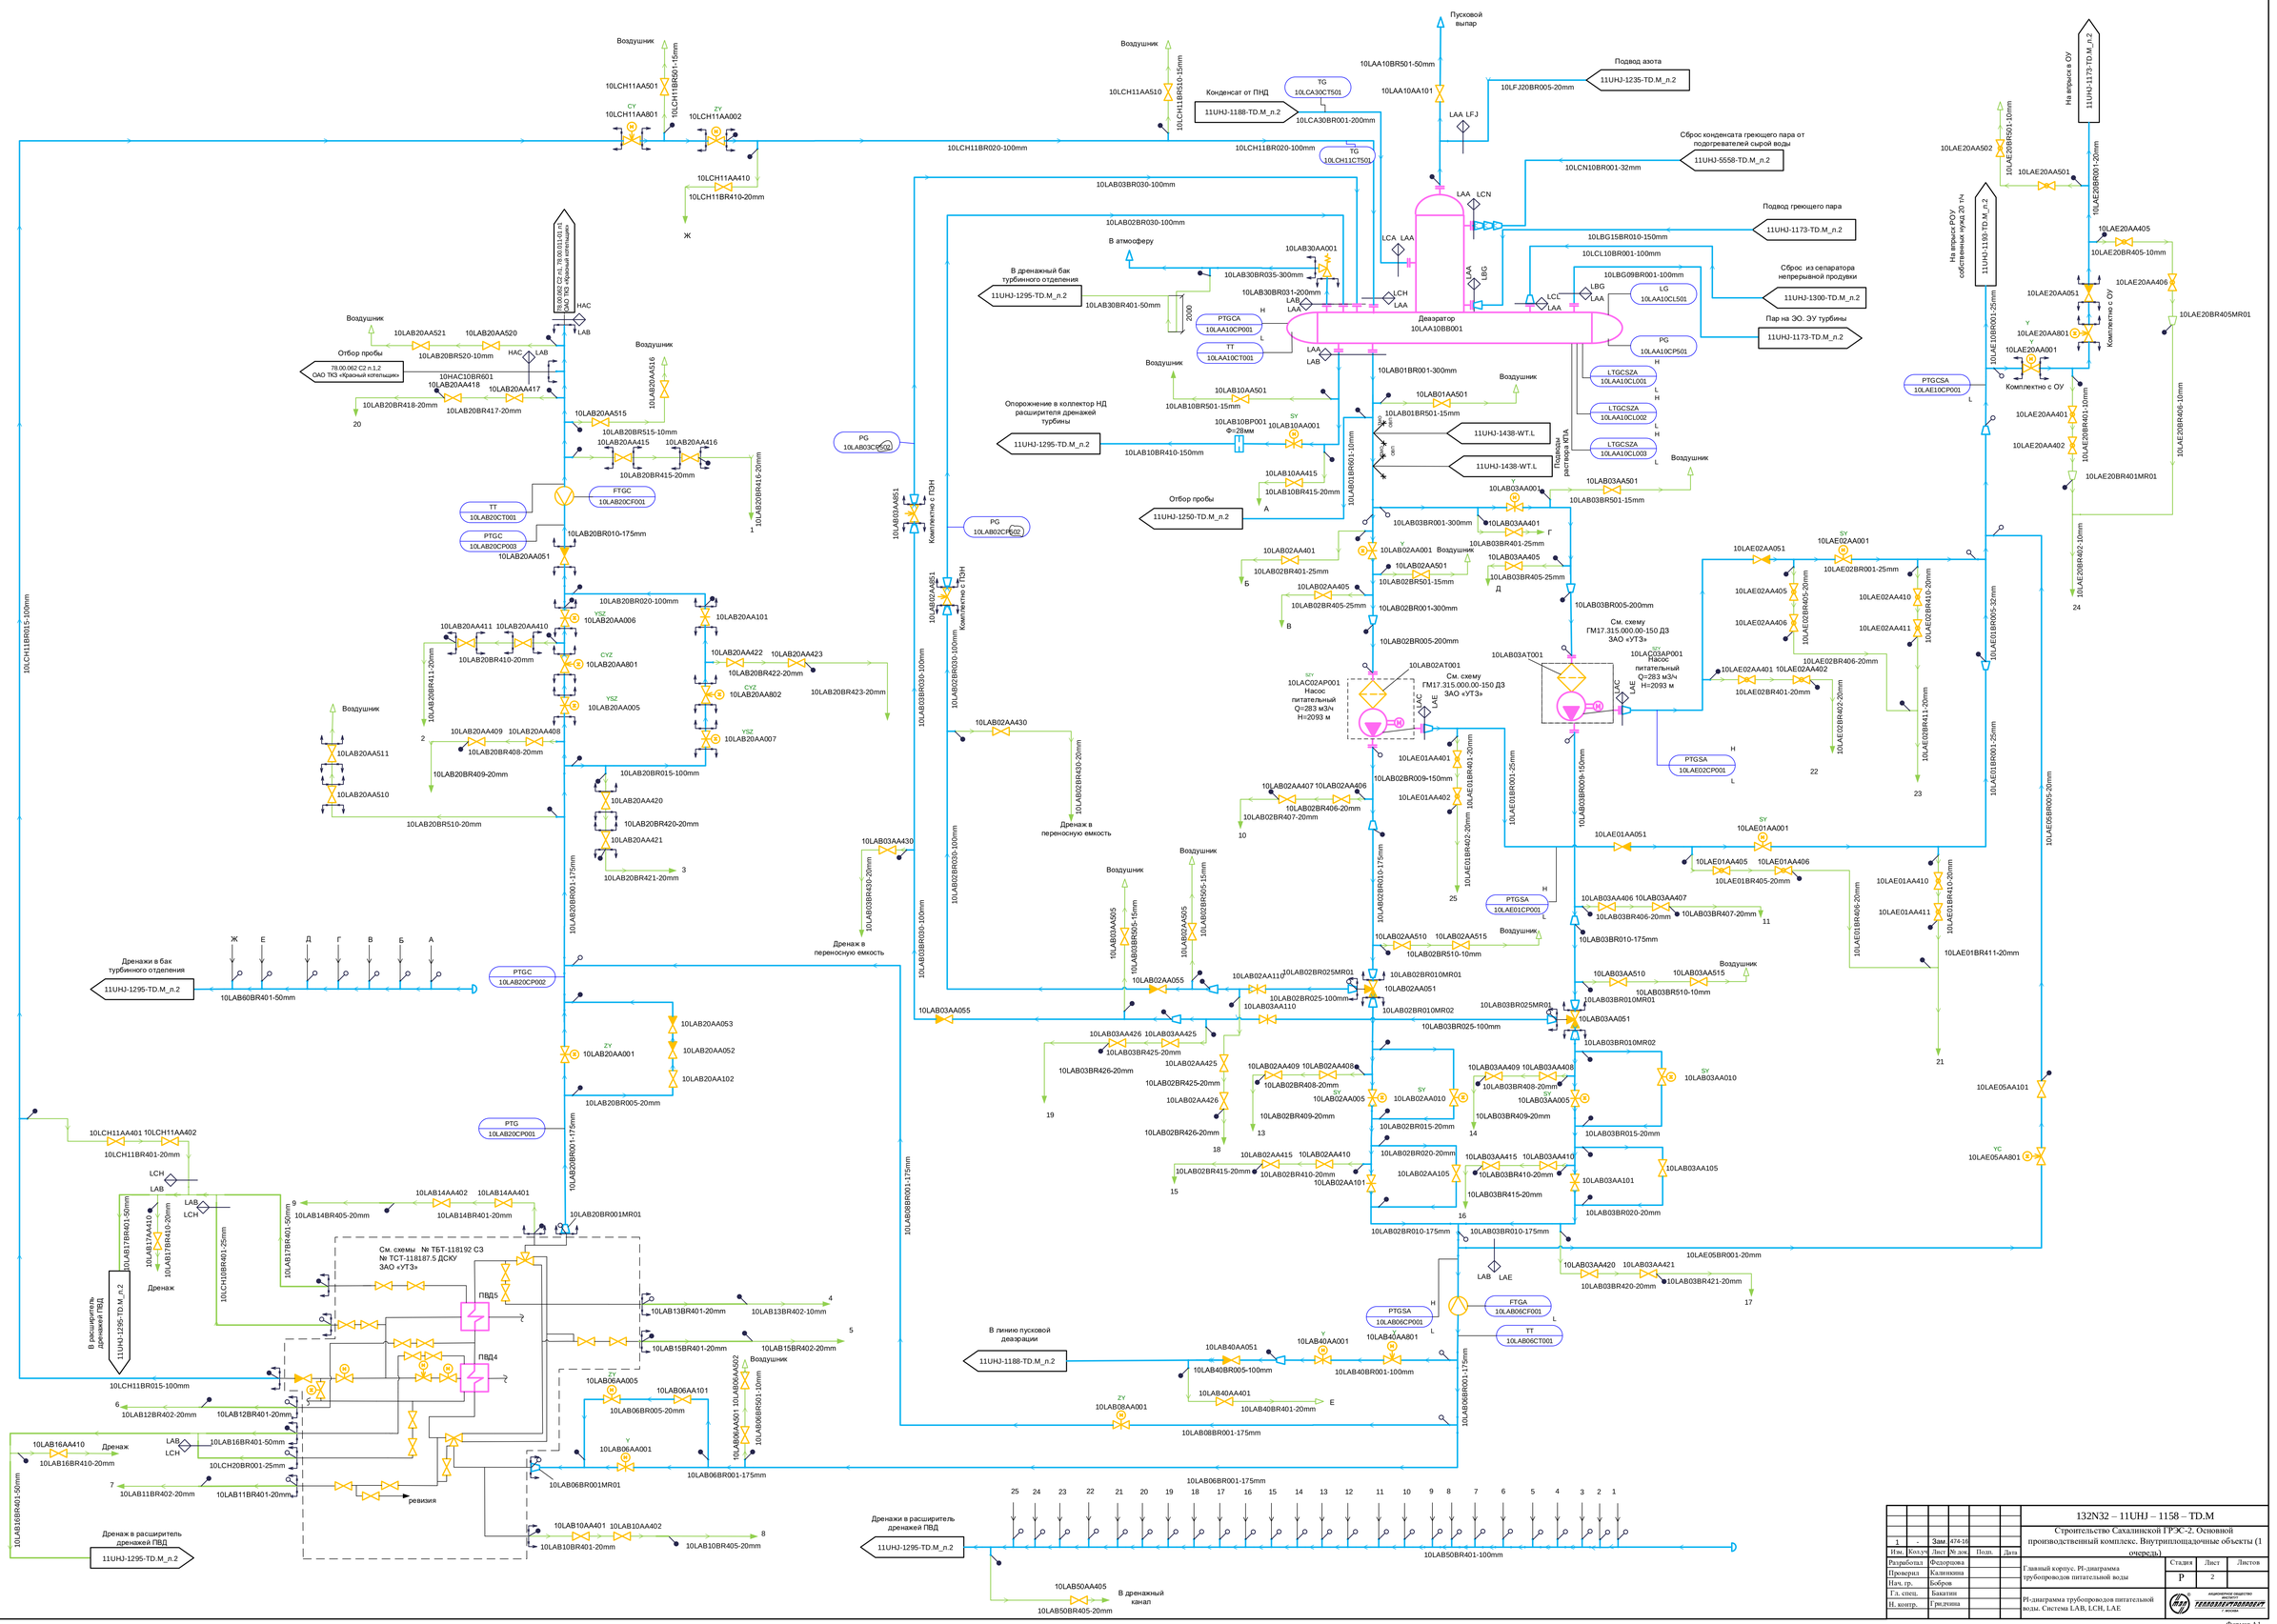

						132N32 – 11UHJ – 1158 – TD.M	
						Строительство Сахалинской ГРЭС-2. Основной производственный комплекс. Внутриплощадочные объекты (1 очередь)	
1	-	Зам	474-16				
Изм.	Кол.уч	Лист	№ док.	Подп.	Дата		
Разработал	Федорцова					Главный корпус. PI-диаграмма трубопроводов питательной воды	Стадия: Р; Лист: 2; Листов:
Проверил	Калинкина						
Нач. гр.	Бобров						
Т.к. спец.	Бакатин					PI-диаграмма трубопроводов питательной воды. Система LAB, LCH, LAE	Акционерное общество Теплоэлектропроект г. Москва
Н. контр.	Гридчина						

Согласовано

Взам. инв. №

Подпись и дата

Инв. № подл.

ОАСУ

Энергоснабжение

Формат А1