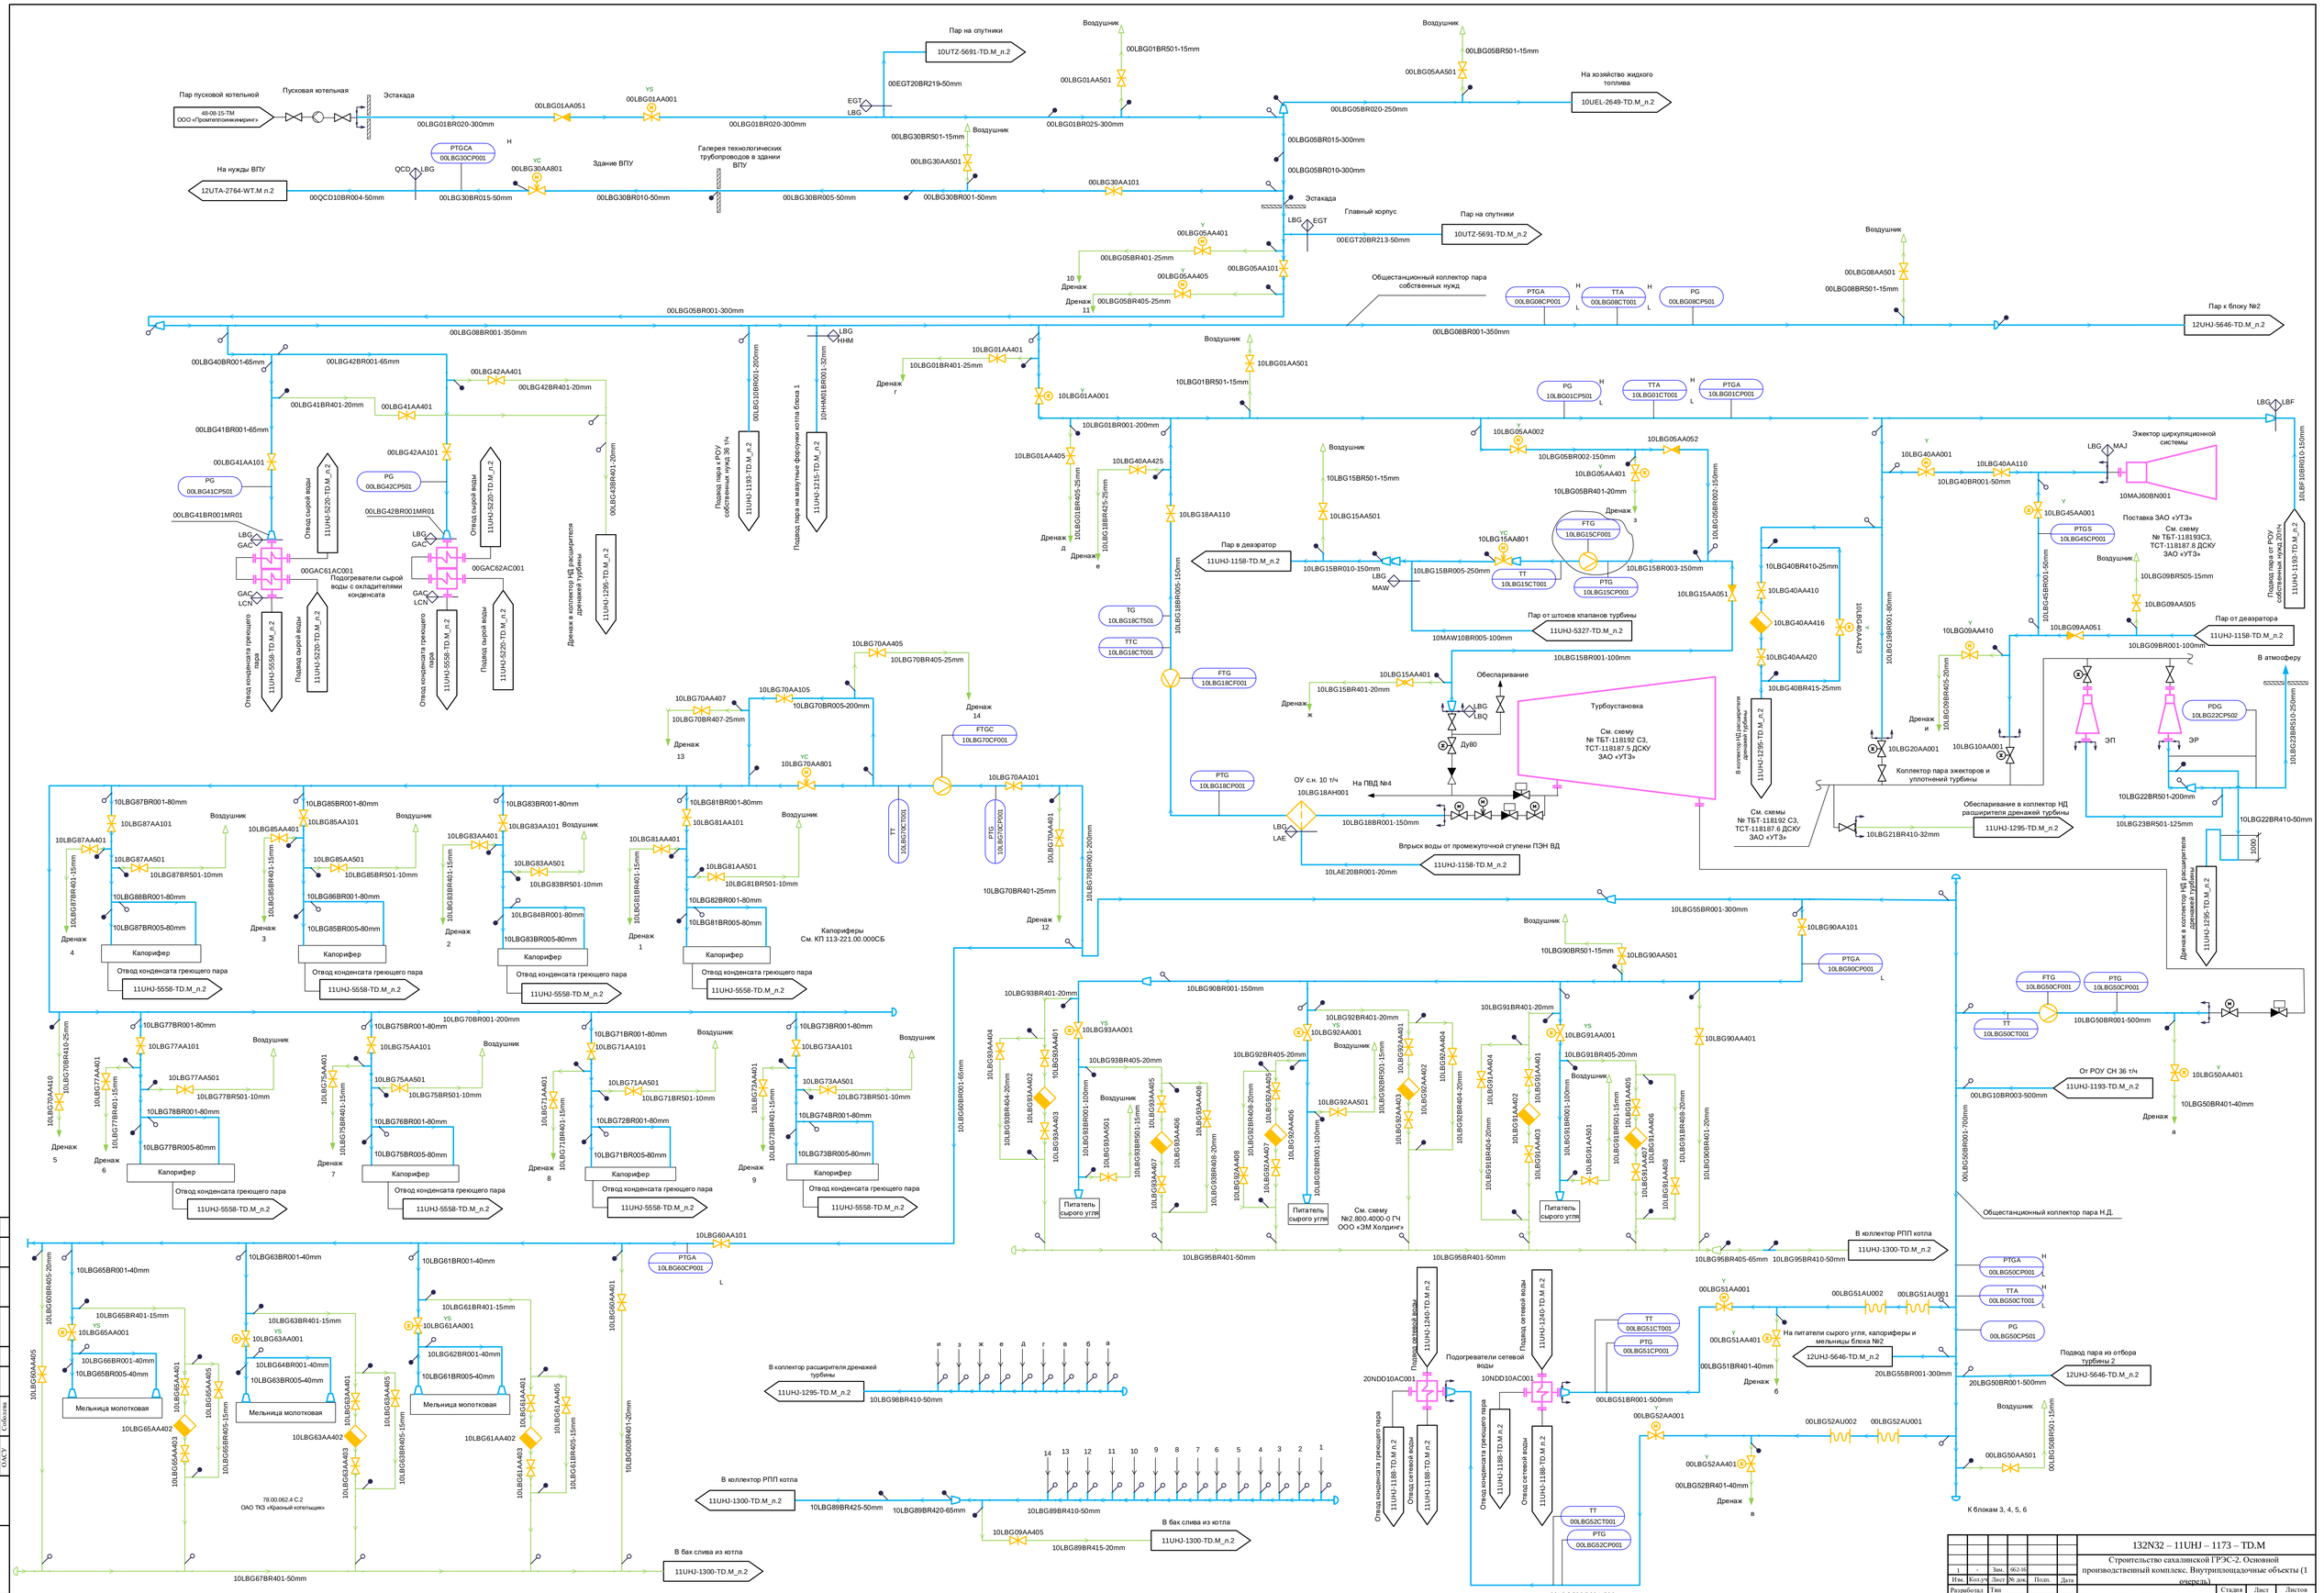

1	-	Зам.	062-16			
Изм.	Кол.уч.	Лист	№ док.	Подп.	Дата	
Разработал		Тян				
Проверил		Калинкина				
Нач. гр.		Бобров				
Гл. спец.		Бакатин				
Н. контр.		Грендгина				

132N32 – 11UHJ – 1173 – TD.M

Строительство сахалинской ГРЭС-2. Основной производственный комплекс. Внутриплощадочные объекты (1 очередь)

Главный корпус. PI-диаграмма трубопроводов пара собственных нужд.

PI-диаграмма трубопроводов пара собственных нужд. Система LBG

Стадия	Лист	Листов
Р	2	

Согласовано

Взам. инв. №

Подпись и дата

Инв. № подл.

Формат А0