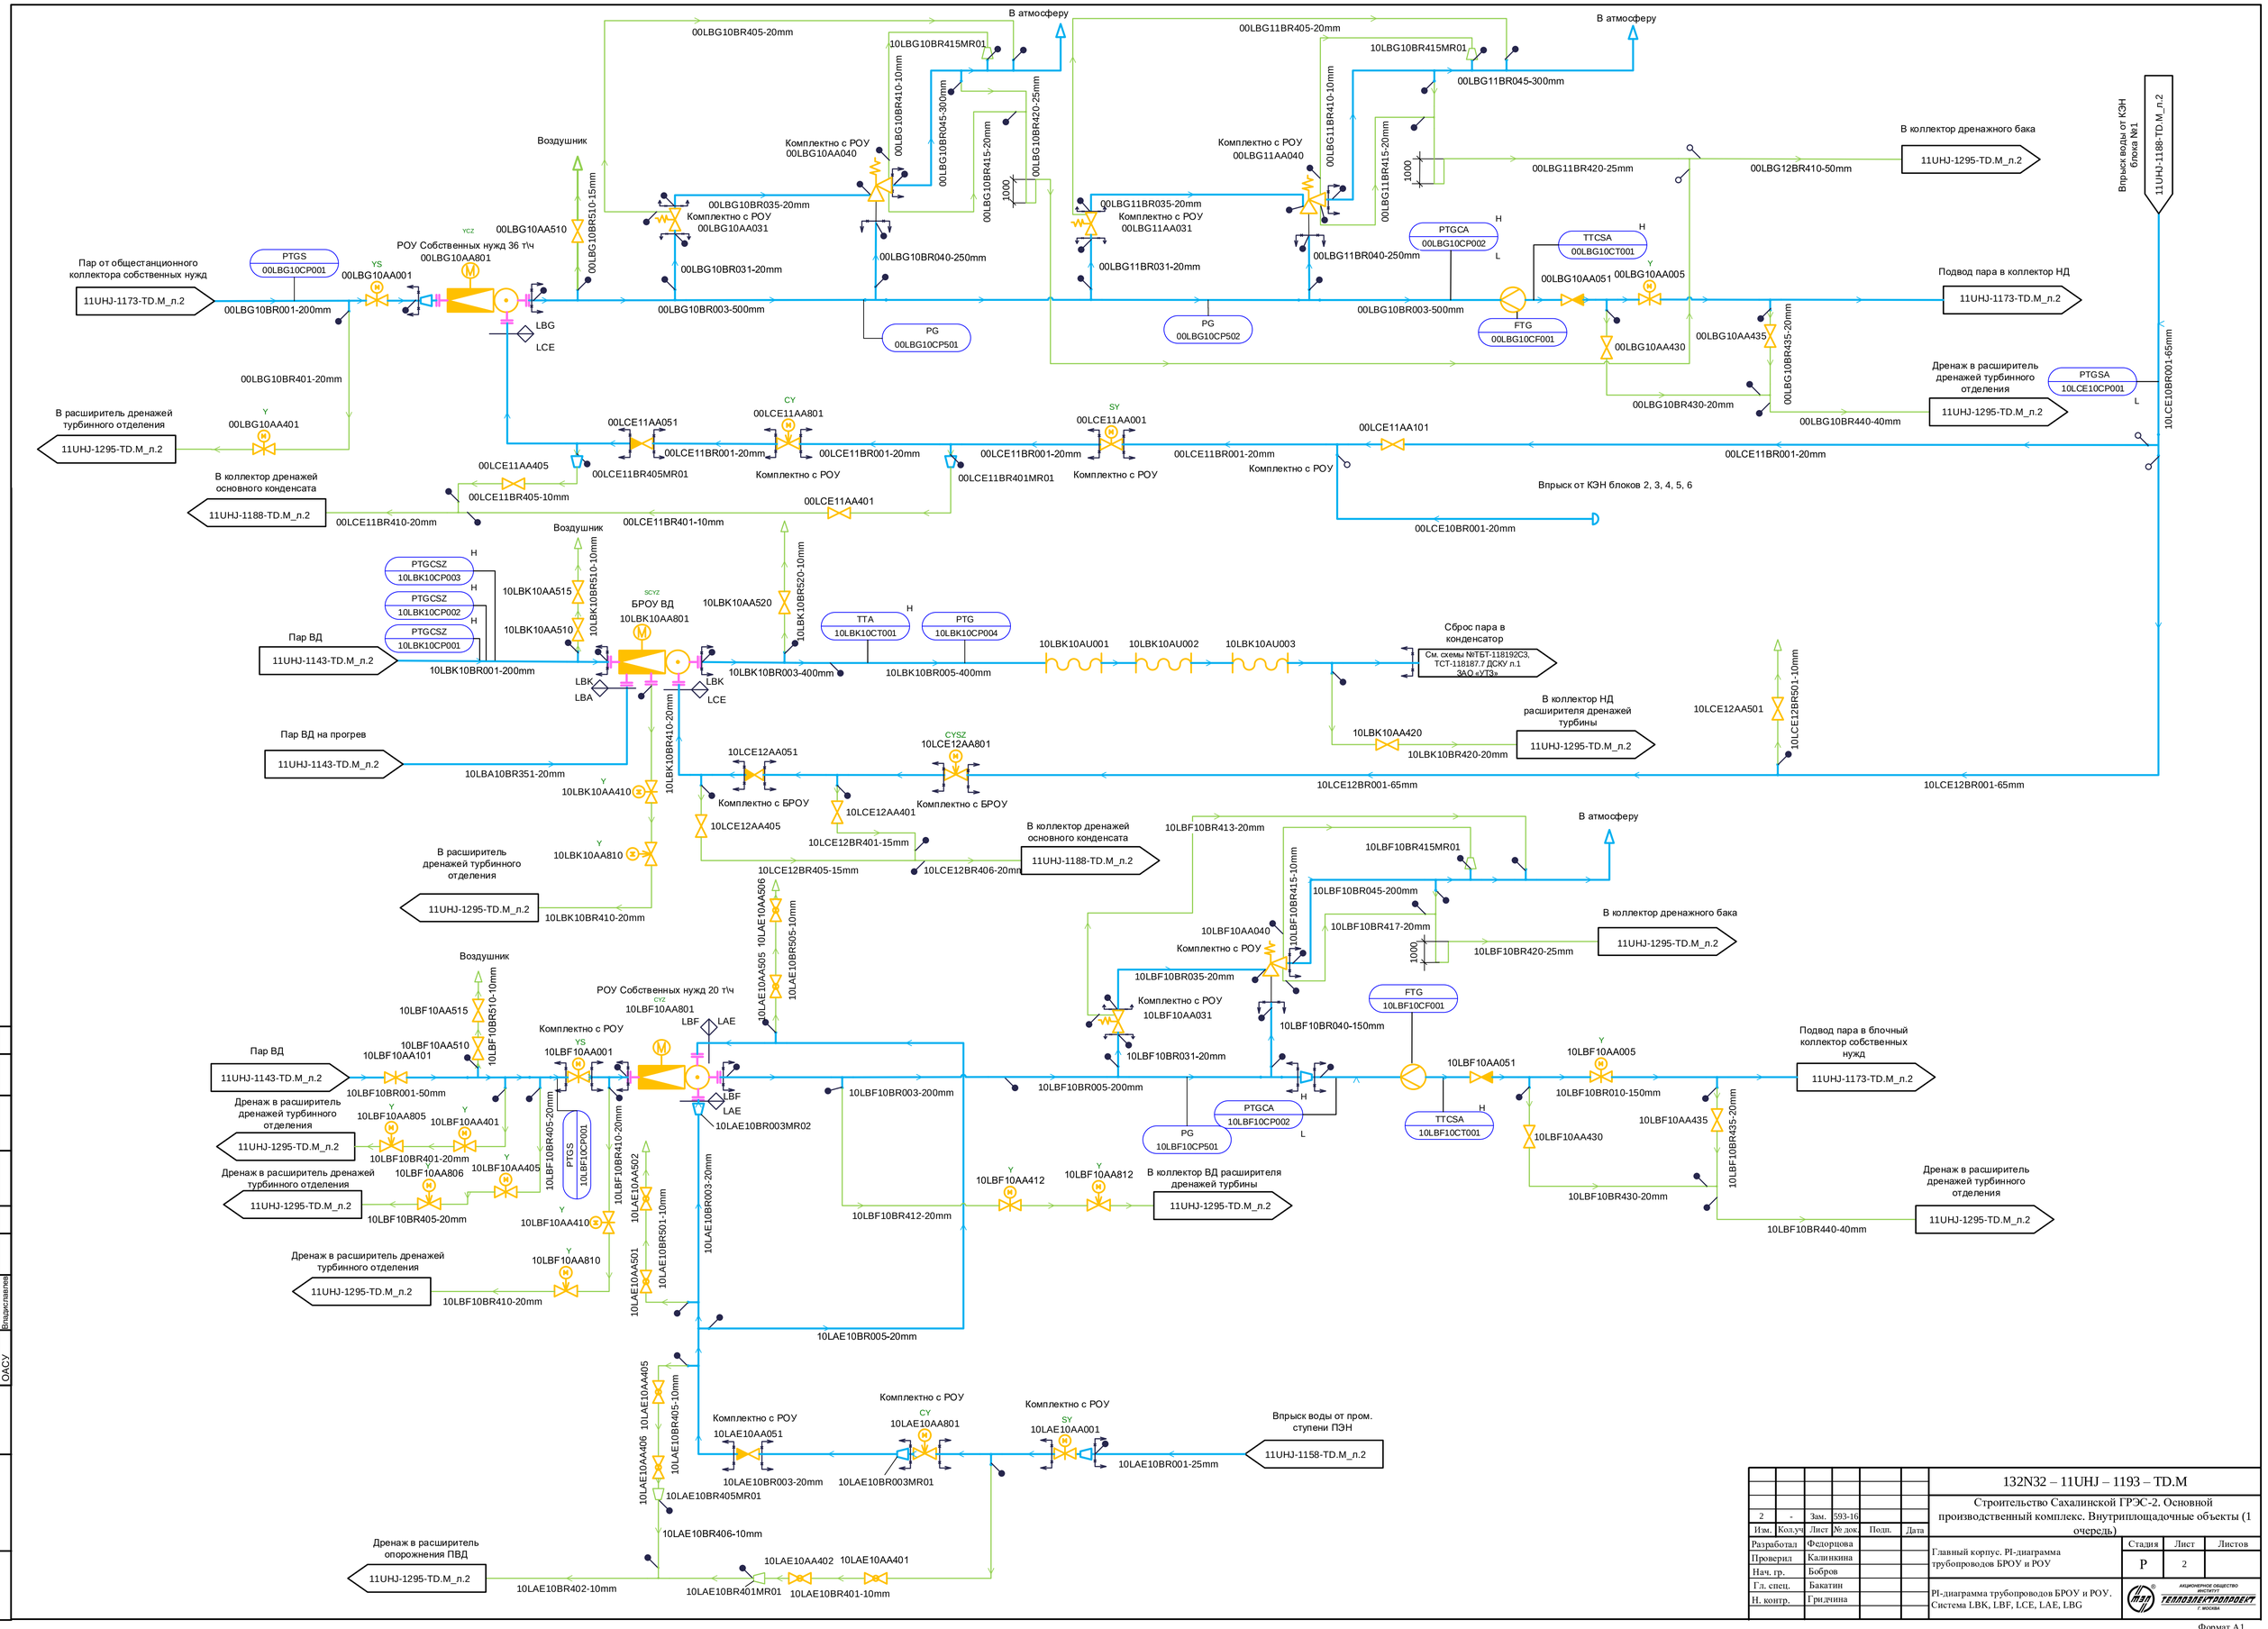

2	-	Зам.	593-16			
Изм.	Кол.уч	Лист	№ док.	Подп.	Дата	
Разработал		Федорцова				
Проверил		Калинкина				
Нач. гр.		Бобров				
Гл. спец.		Бакатин				
Н. контр.		Гридчина				

132N32 – 11UHJ – 1193 – TD.M

Строительство Сахалинской ГРЭС-2. Основной производственный комплекс. Внуриплощадочные объекты (1 очередь)

Главный корпус. PI-диаграмма трубопроводов БРОУ и РОУ

Стадия	Лист	Листов
Р	2	

PI-диаграмма трубопроводов БРОУ и РОУ. Система LBK, LBF, LCE, LAE, LBG

АКЦИОНЕРНОЕ ОБЩЕСТВО ИНСТИТУТ ТЕПЛОЭЛЕКТРОПРОЕКТ г. МОСКВА

Согласовано

ОАСУ

Взам. инв. №

Подпись и дата

Инв. № подл.

Формат А1