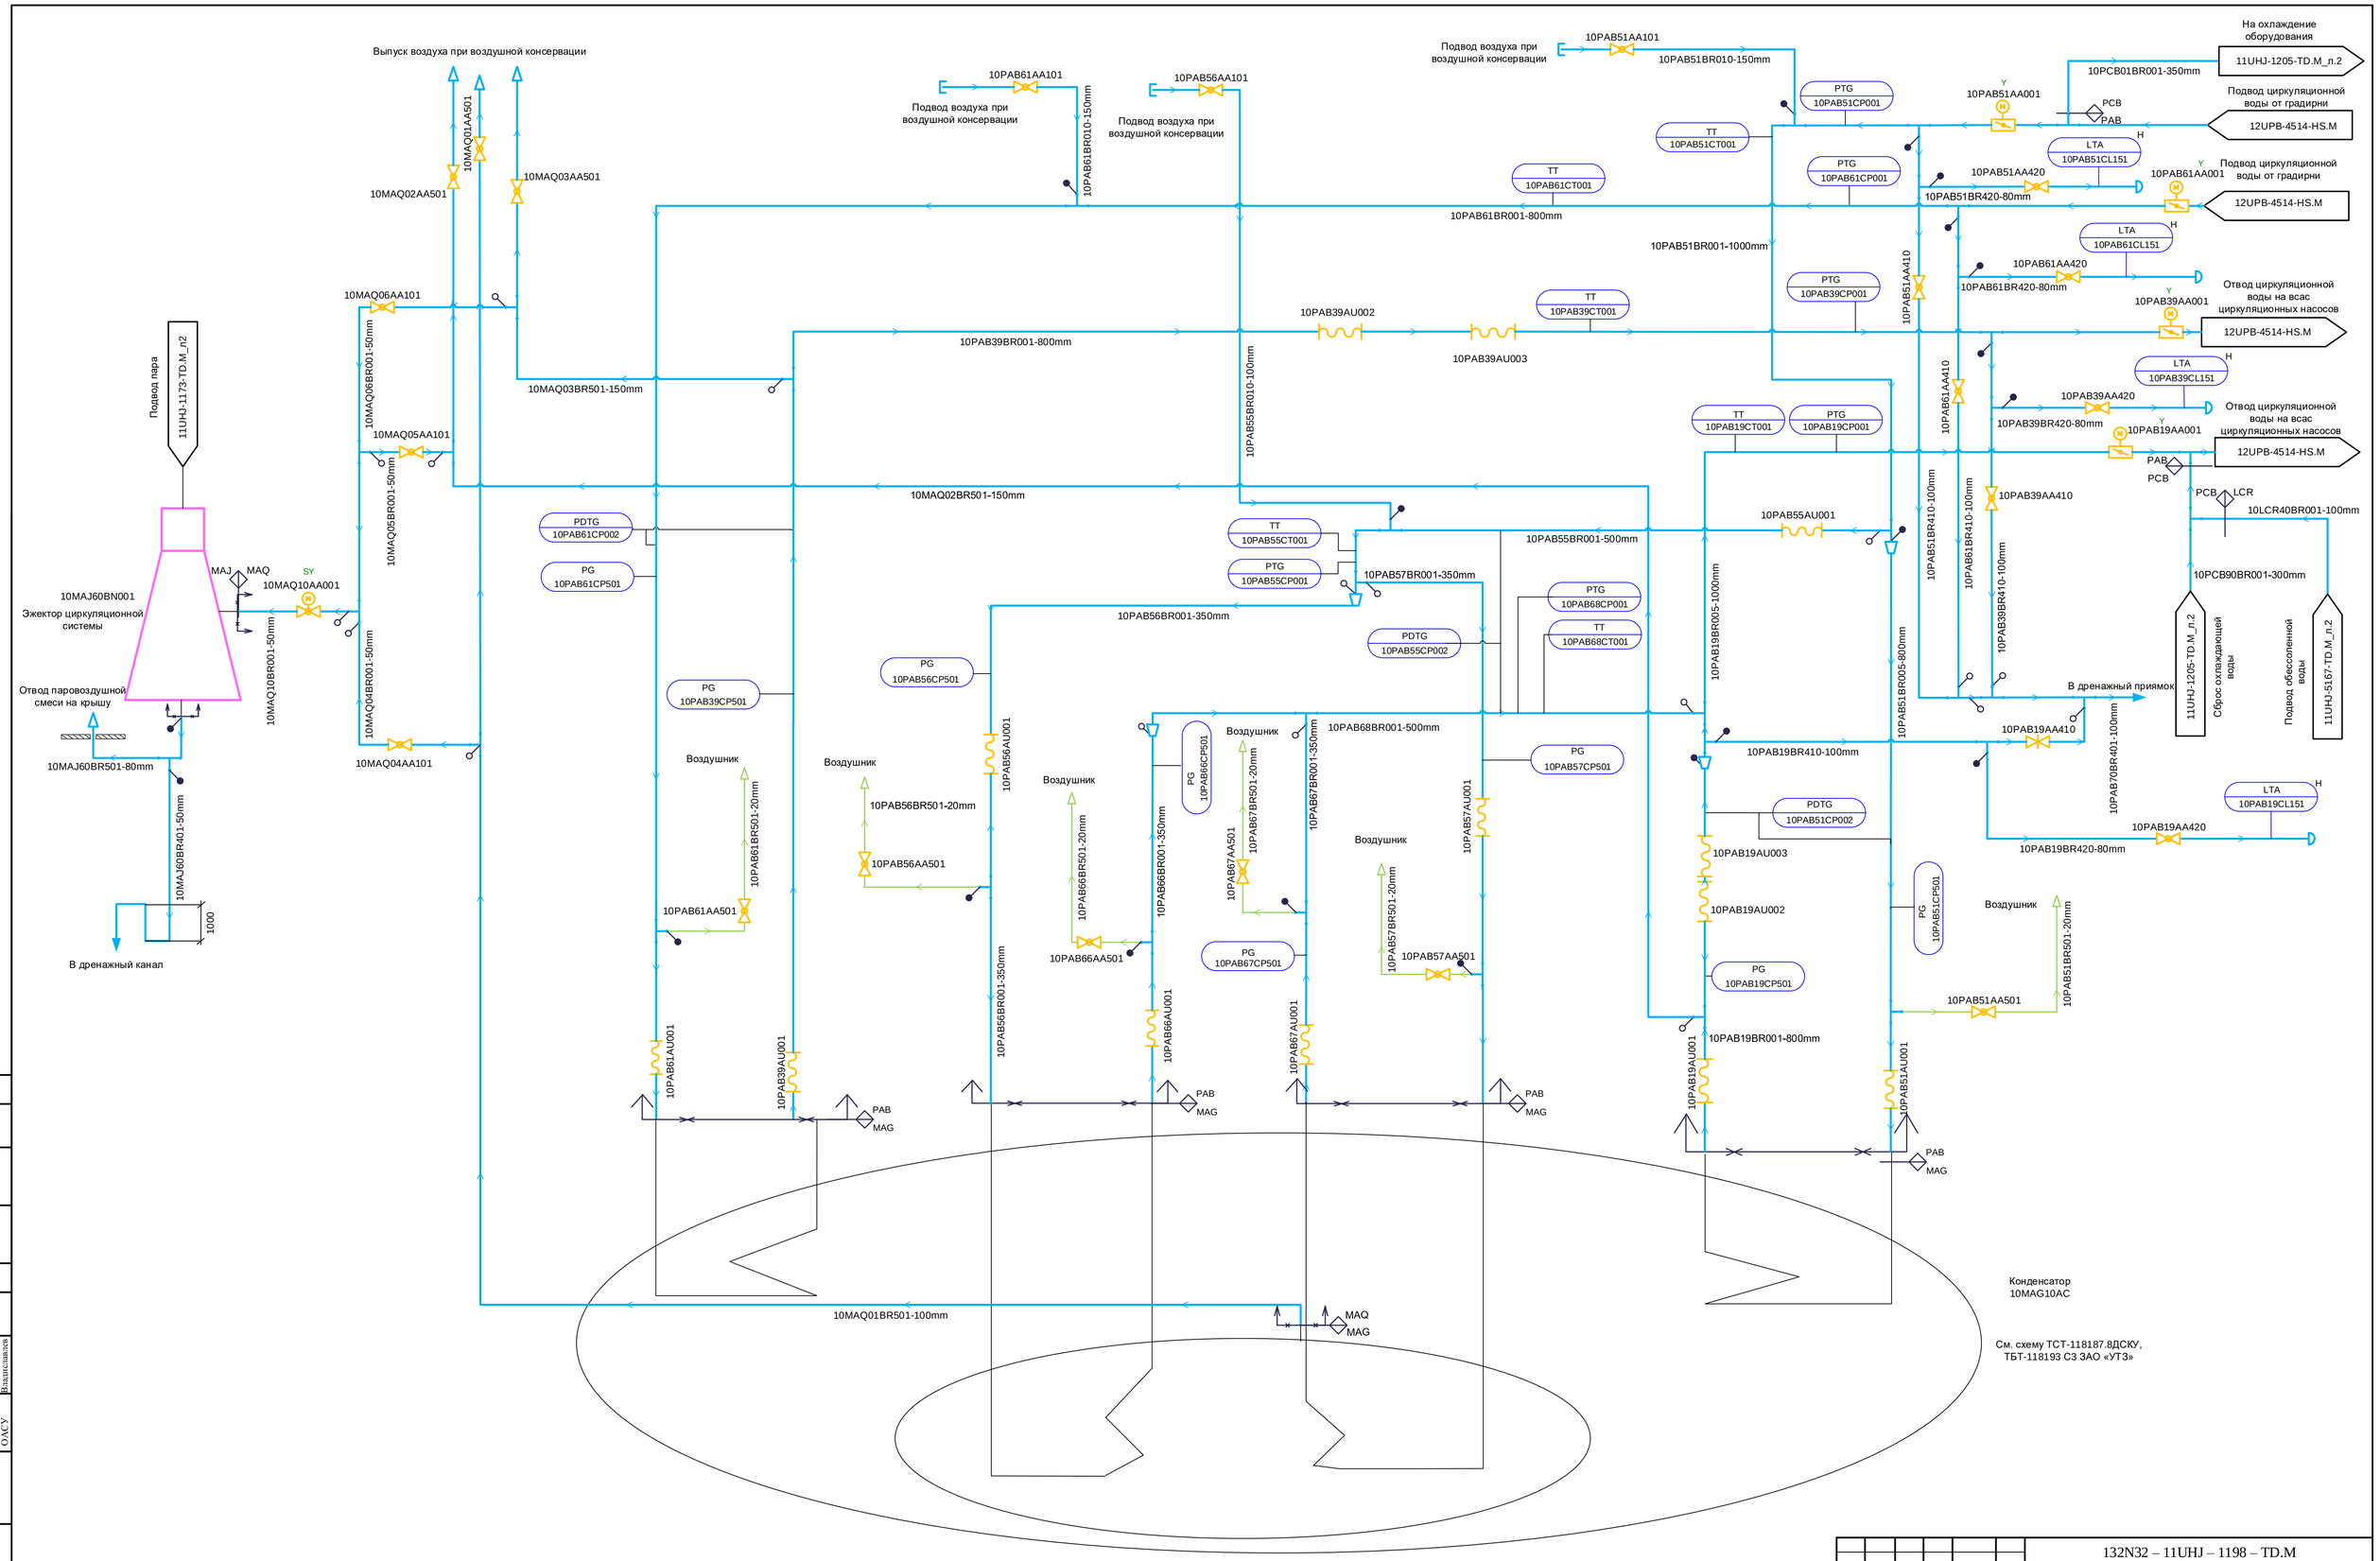

2	-	Зам.	474-16			132N32 – 11UHJ – 1198 – TD.M
Изм.	Кол.уч	Лист	№ док.	Подп.	Дата	Строительство сахалинской ГРЭС-2. Основной производственный комплекс. Внутриплощадочные объекты (1 очередь)
Разработал		Тян				Главный корпус. PI-диаграмма трубопроводов циркуляционной охлаждающей воды
Проверил		Калинкина				Стадия: Р; Лист: 2; Листов:
Нач. гр.		Бобров				
Гл. спец.		Бакатин				PI-диаграмма трубопроводов циркуляционной охлаждающей воды. Система PAB, MAQ.
Н. контр.		Грядчина				АКЦИОНЕРНОЕ ОБЩЕСТВО ИНСТИТУТ ТЕПЛОЭЛЕКТРОПРОЕКТ г. МОСКВА

Согласовано

ОАСУ

Владиславлев

Взам. инв. №

Подпись и дата

Инв. № подл.

Формат А1