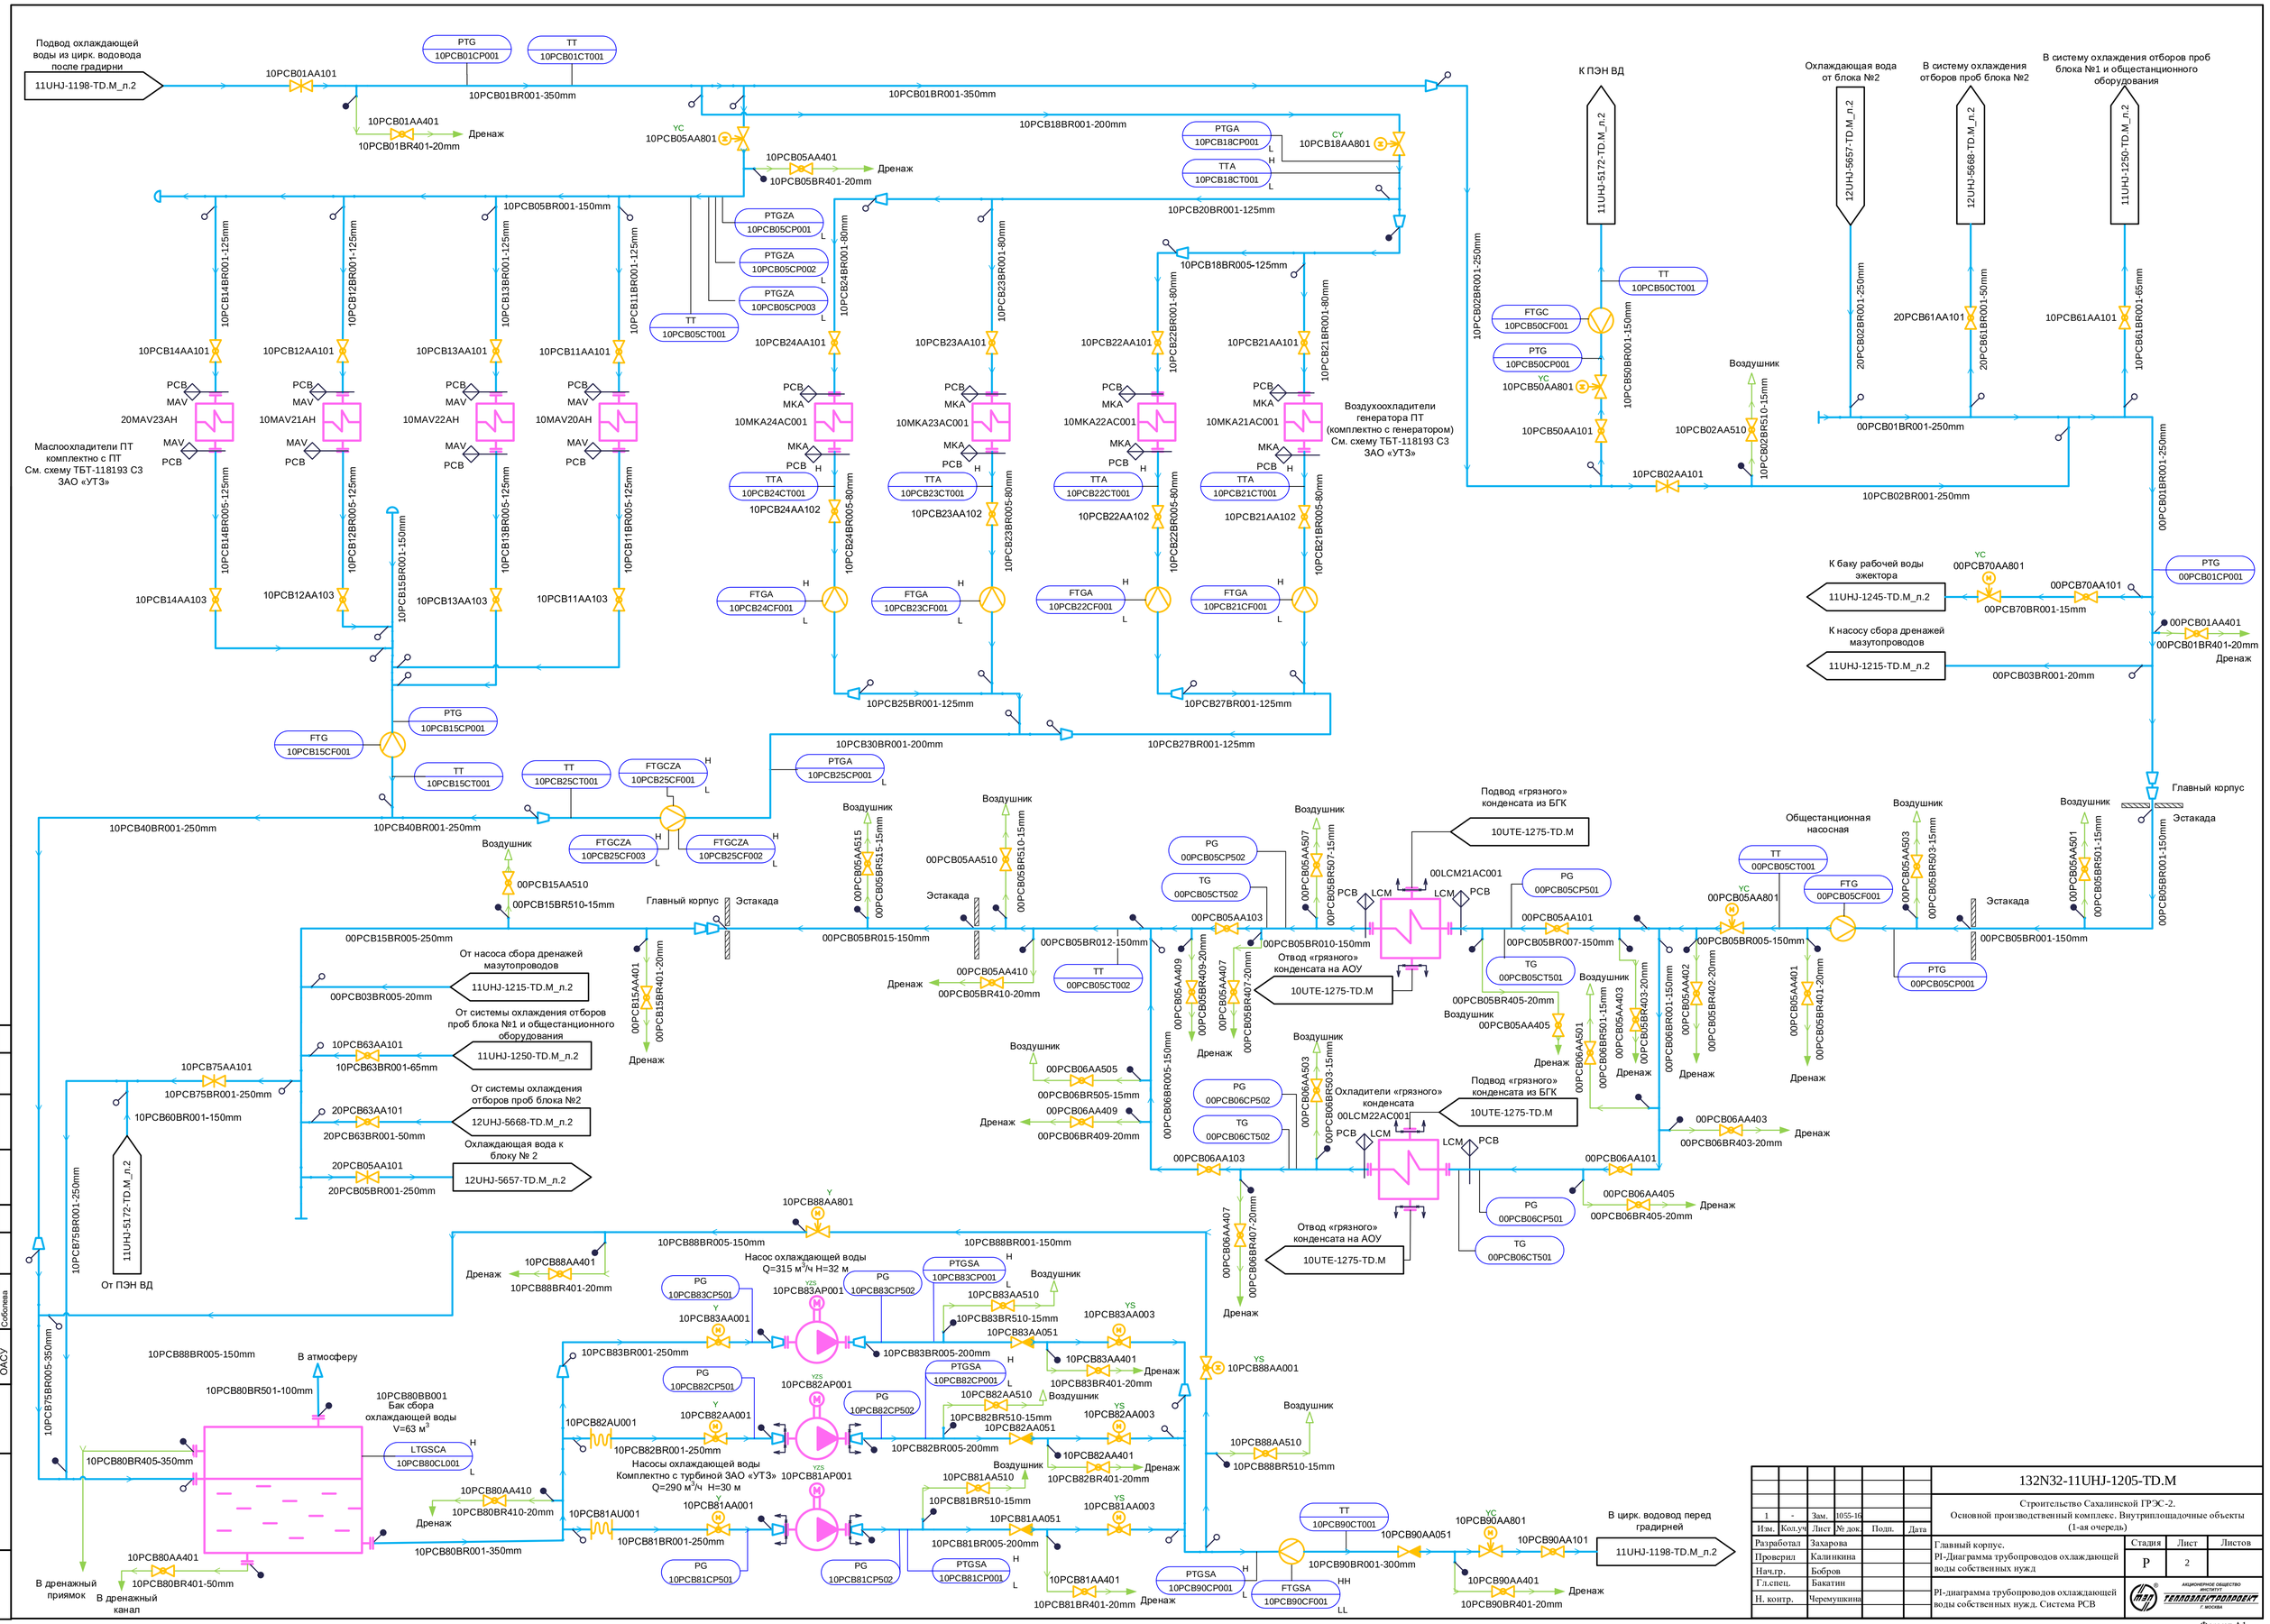
Подвод охлаждающей воды из цирк. водовода после градирни
11UHJ-1198-TD.M_п.2
10PCB01AA101
PTG 10PCB01CP001
TT 10PCB01CT001
10PCB01BR001-350mm
10PCB01AA401
Дренаж
10PCB01BR401-20mm
10PCB05AA801
10PCB05AA401
10PCB05BR401-20mm
10PCB18BR001-200mm
PTGA 10PCB18CP001
TTA 10PCB18CT001
10PCB18AA801
10PCB20BR001-125mm
10PCB05BR001-150mm
PTGZA 10PCB05CP001
PTGZA 10PCB05CP002
PTGZA 10PCB05CP003
TT 10PCB05CT001
10PCB14BR001-125mm
10PCB12BR001-125mm
10PCB13BR001-125mm
10PCB11BR001-125mm
10PCB24BR001-80mm
10PCB23BR001-80mm
10PCB22BR001-80mm
10PCB21BR001-80mm
10PCB18BR005-125mm
10PCB14AA101
10PCB12AA101
10PCB13AA101
10PCB11AA101
10PCB24AA101
10PCB23AA101
10PCB22AA101
10PCB21AA101
PCB
MAV
20MAV23AH
10MAV21AH
10MAV22AH
10MAV20AH
MKA
10MKA24AC001
10MKA23AC001
10MKA22AC001
10MKA21AC001
Маслоохладители ПТ комплектно с ПТ См. схему ТБТ-118193 С3 ЗАО «УТЗ»
Воздухоохладители генератора ПТ (комплектно с генератором) См. схему ТБТ-118193 С3 ЗАО «УТЗ»
TTA 10PCB24CT001
TTA 10PCB23CT001
TTA 10PCB22CT001
TTA 10PCB21CT001
10PCB24AA102
10PCB23AA102
10PCB22AA102
10PCB21AA102
10PCB24BR005-80mm
10PCB23BR005-80mm
10PCB22BR005-80mm
10PCB21BR005-80mm
10PCB14BR005-125mm
10PCB12BR005-125mm
10PCB13BR005-125mm
10PCB11BR005-125mm
10PCB14AA103
10PCB12AA103
10PCB13AA103
10PCB11AA103
10PCB15BR001-150mm
FTGA 10PCB24CF001
FTGA 10PCB23CF001
FTGA 10PCB22CF001
FTGA 10PCB21CF001
10PCB25BR001-125mm
10PCB27BR001-125mm
10PCB30BR001-200mm
PTG 10PCB15CP001
FTG 10PCB15CF001
TT 10PCB15CT001
TT 10PCB25CT001
FTGCZA 10PCB25CF001
PTGA 10PCB25CP001
FTGCZA 10PCB25CF003
FTGCZA 10PCB25CF002
10PCB40BR001-250mm
10PCB40BR001-250mm
Воздушник
10PCB02BR001-250mm
К ПЭН ВД
11UHJ-5172-TD.M_п.2
TT 10PCB50CT001
FTGC 10PCB50CF001
PTG 10PCB50CP001
10PCB50AA801
10PCB50BR001-150mm
10PCB50AA101
10PCB02AA101
10PCB02AA510
10PCB02BR510-15mm
Охлаждающая вода от блока №2
12UHJ-5657-TD.M_п.2
20PCB02BR001-250mm
В систему охлаждения отборов проб блока №2
12UHJ-5668-TD.M_п.2
20PCB61AA101
20PCB61BR001-50mm
В систему охлаждения отборов проб блока №1 и общестанционного оборудования
11UHJ-1250-TD.M_п.2
10PCB61AA101
10PCB61BR001-65mm
00PCB01BR001-250mm
00PCB01BR001-250mm
К баку рабочей воды эжектора
11UHJ-1245-TD.M_п.2
00PCB70AA801
00PCB70AA101
00PCB70BR001-15mm
PTG 00PCB01CP001
К насосу сбора дренажей мазутопроводов
11UHJ-1215-TD.M_п.2
00PCB03BR001-20mm
00PCB01AA401
00PCB01BR401-20mm
Главный корпус
Эстакада
00PCB05BR001-150mm
00PCB15BR005-250mm
00PCB15AA510
00PCB15BR510-15mm
00PCB05BR015-150mm
00PCB05AA515
00PCB05BR515-15mm
00PCB05AA510
00PCB05BR510-15mm
00PCB05AA410
00PCB05BR410-20mm
TT 00PCB05CT002
00PCB05BR012-150mm
00PCB05BR010-150mm
00PCB05AA103
00PCB05AA409
00PCB05BR409-20mm
00PCB05AA407
00PCB05BR407-20mm
Отвод «грязного» конденсата на АОУ
10UTE-1275-TD.M
00PCB05AA507
00PCB05BR507-15mm
PG 00PCB05CP502
TG 00PCB05CT502
00LCM21AC001
LCM
Подвод «грязного» конденсата из БГК
10UTE-1275-TD.M
PG 00PCB05CP501
00PCB05AA101
00PCB05BR007-150mm
TG 00PCB05CT501
00PCB05BR405-20mm
00PCB05AA405
00PCB05AA501
00PCB06BR501-15mm
00PCB05AA403
00PCB05BR403-20mm
00PCB06BR001-150mm
00PCB05AA402
00PCB05BR402-20mm
00PCB05AA401
00PCB05BR401-20mm
00PCB05BR005-150mm
Общестанционная насосная
TT 00PCB05CT001
FTG 00PCB05CF001
00PCB05AA801
00PCB05AA503
00PCB05BR503-15mm
00PCB05AA501
00PCB05BR501-15mm
PTG 00PCB05CP001
00PCB05BR001-150mm
От насоса сбора дренажей мазутопроводов
11UHJ-1215-TD.M_п.2
00PCB03BR005-20mm
От системы охлаждения отборов проб блока №1 и общестанционного оборудования
11UHJ-1250-TD.M_п.2
10PCB63AA101
10PCB63BR001-65mm
10PCB75AA101
10PCB75BR001-250mm
10PCB60BR001-150mm
От системы охлаждения отборов проб блока №2
12UHJ-5668-TD.M_п.2
20PCB63AA101
20PCB63BR001-50mm
Охлаждающая вода к блоку № 2
12UHJ-5657-TD.M_п.2
20PCB05AA101
20PCB05BR001-250mm
11UHJ-5172-TD.M_п.2
От ПЭН ВД
00PCB15AA401
00PCB15BR401-20mm
00PCB06AA505
00PCB06BR505-15mm
00PCB06AA409
00PCB06BR409-20mm
PG 00PCB06CP502
TG 00PCB06CT502
00PCB06AA503
00PCB06BR503-15mm
Охладители «грязного» конденсата
00LCM22AC001
Подвод «грязного» конденсата из БГК
10UTE-1275-TD.M
00PCB06AA403
00PCB06BR403-20mm
00PCB06AA103
00PCB06AA101
00PCB06AA405
00PCB06BR405-20mm
PG 00PCB06CP501
TG 00PCB06CT501
00PCB06AA407
00PCB06BR407-20mm
Отвод «грязного» конденсата на АОУ
10UTE-1275-TD.M
10PCB88AA801
10PCB88BR005-150mm
10PCB88BR001-150mm
10PCB88AA401
10PCB88BR401-20mm
Насос охлаждающей воды Q=315 м³/ч H=32 м
PG 10PCB83CP501
PG 10PCB83CP502
PTGSA 10PCB83CP001
10PCB83AP001
10PCB83AA510
10PCB83BR510-15mm
10PCB83AA051
10PCB83AA003
10PCB83AA001
10PCB83BR001-250mm
10PCB83BR005-200mm
10PCB83AA401
10PCB83BR401-20mm
10PCB88AA001
10PCB88AA510
10PCB88BR510-15mm
10PCB88BR005-150mm
10PCB75BR005-350mm
В атмосферу
10PCB80BR501-100mm
10PCB80BB001 Бак сбора охлаждающей воды V=63 м³
LTGSCA 10PCB80CL001
10PCB80BR405-350mm
10PCB80AA410
10PCB80BR410-20mm
10PCB80BR001-350mm
10PCB80AA401
10PCB80BR401-50mm
В дренажный приямок
В дренажный канал
PG 10PCB82CP501
PG 10PCB82CP502
PTGSA 10PCB82CP001
10PCB82AP001
10PCB82AA510
10PCB82BR510-15mm
10PCB82AA051
10PCB82AA003
10PCB82AA001
10PCB82BR001-250mm
10PCB82BR005-200mm
10PCB82AA401
10PCB82BR401-20mm
10PCB82AU001
Насосы охлаждающей воды Комплектно с турбиной ЗАО «УТЗ» Q=290 м³/ч H=30 м
10PCB81AP001
10PCB81AA510
10PCB81BR510-15mm
10PCB81AA051
10PCB81AA003
10PCB81AA001
10PCB81BR001-250mm
10PCB81BR005-200mm
10PCB81AU001
PG 10PCB81CP501
PG 10PCB81CP502
PTGSA 10PCB81CP001
10PCB81AA401
10PCB81BR401-20mm
TT 10PCB90CT001
10PCB90BR001-300mm
10PCB90AA051
10PCB90AA801
10PCB90AA101
10PCB90AA401
10PCB90BR401-20mm
PTGSA 10PCB90CP001
FTGSA 10PCB90CF001
В цирк. водовод перед градирней
11UHJ-1198-TD.M_п.2
Дренаж
Согласовано
Сабонеа
ОАСУ
Взам. инв. №
Подпись и дата
Инв. № подл.
132N32-11UHJ-1205-TD.M
Строительство Сахалинской ГРЭС-2.
Основной производственный комплекс. Внутриплощадочные объекты
(1-ая очередь)
Изм. Кол.уч Лист № док. Подп. Дата
1 - Зам. 1055-16
Разработал Захарова
Проверил Калинкина
Нач.гр. Бобров
Гл.спец. Бакатин
Н. контр. Черемушкина
Главный корпус.
PI-Диаграмма трубопроводов охлаждающей воды собственных нужд
Стадия Лист Листов
P 2
PI-диаграмма трубопроводов охлаждающей воды собственных нужд. Система PCB
АКЦИОНЕРНОЕ ОБЩЕСТВО ВНИИГИНО
ТЕПЛОЭЛЕКТРОПРОЕКТ
Г. МОСКВА
Формат А1