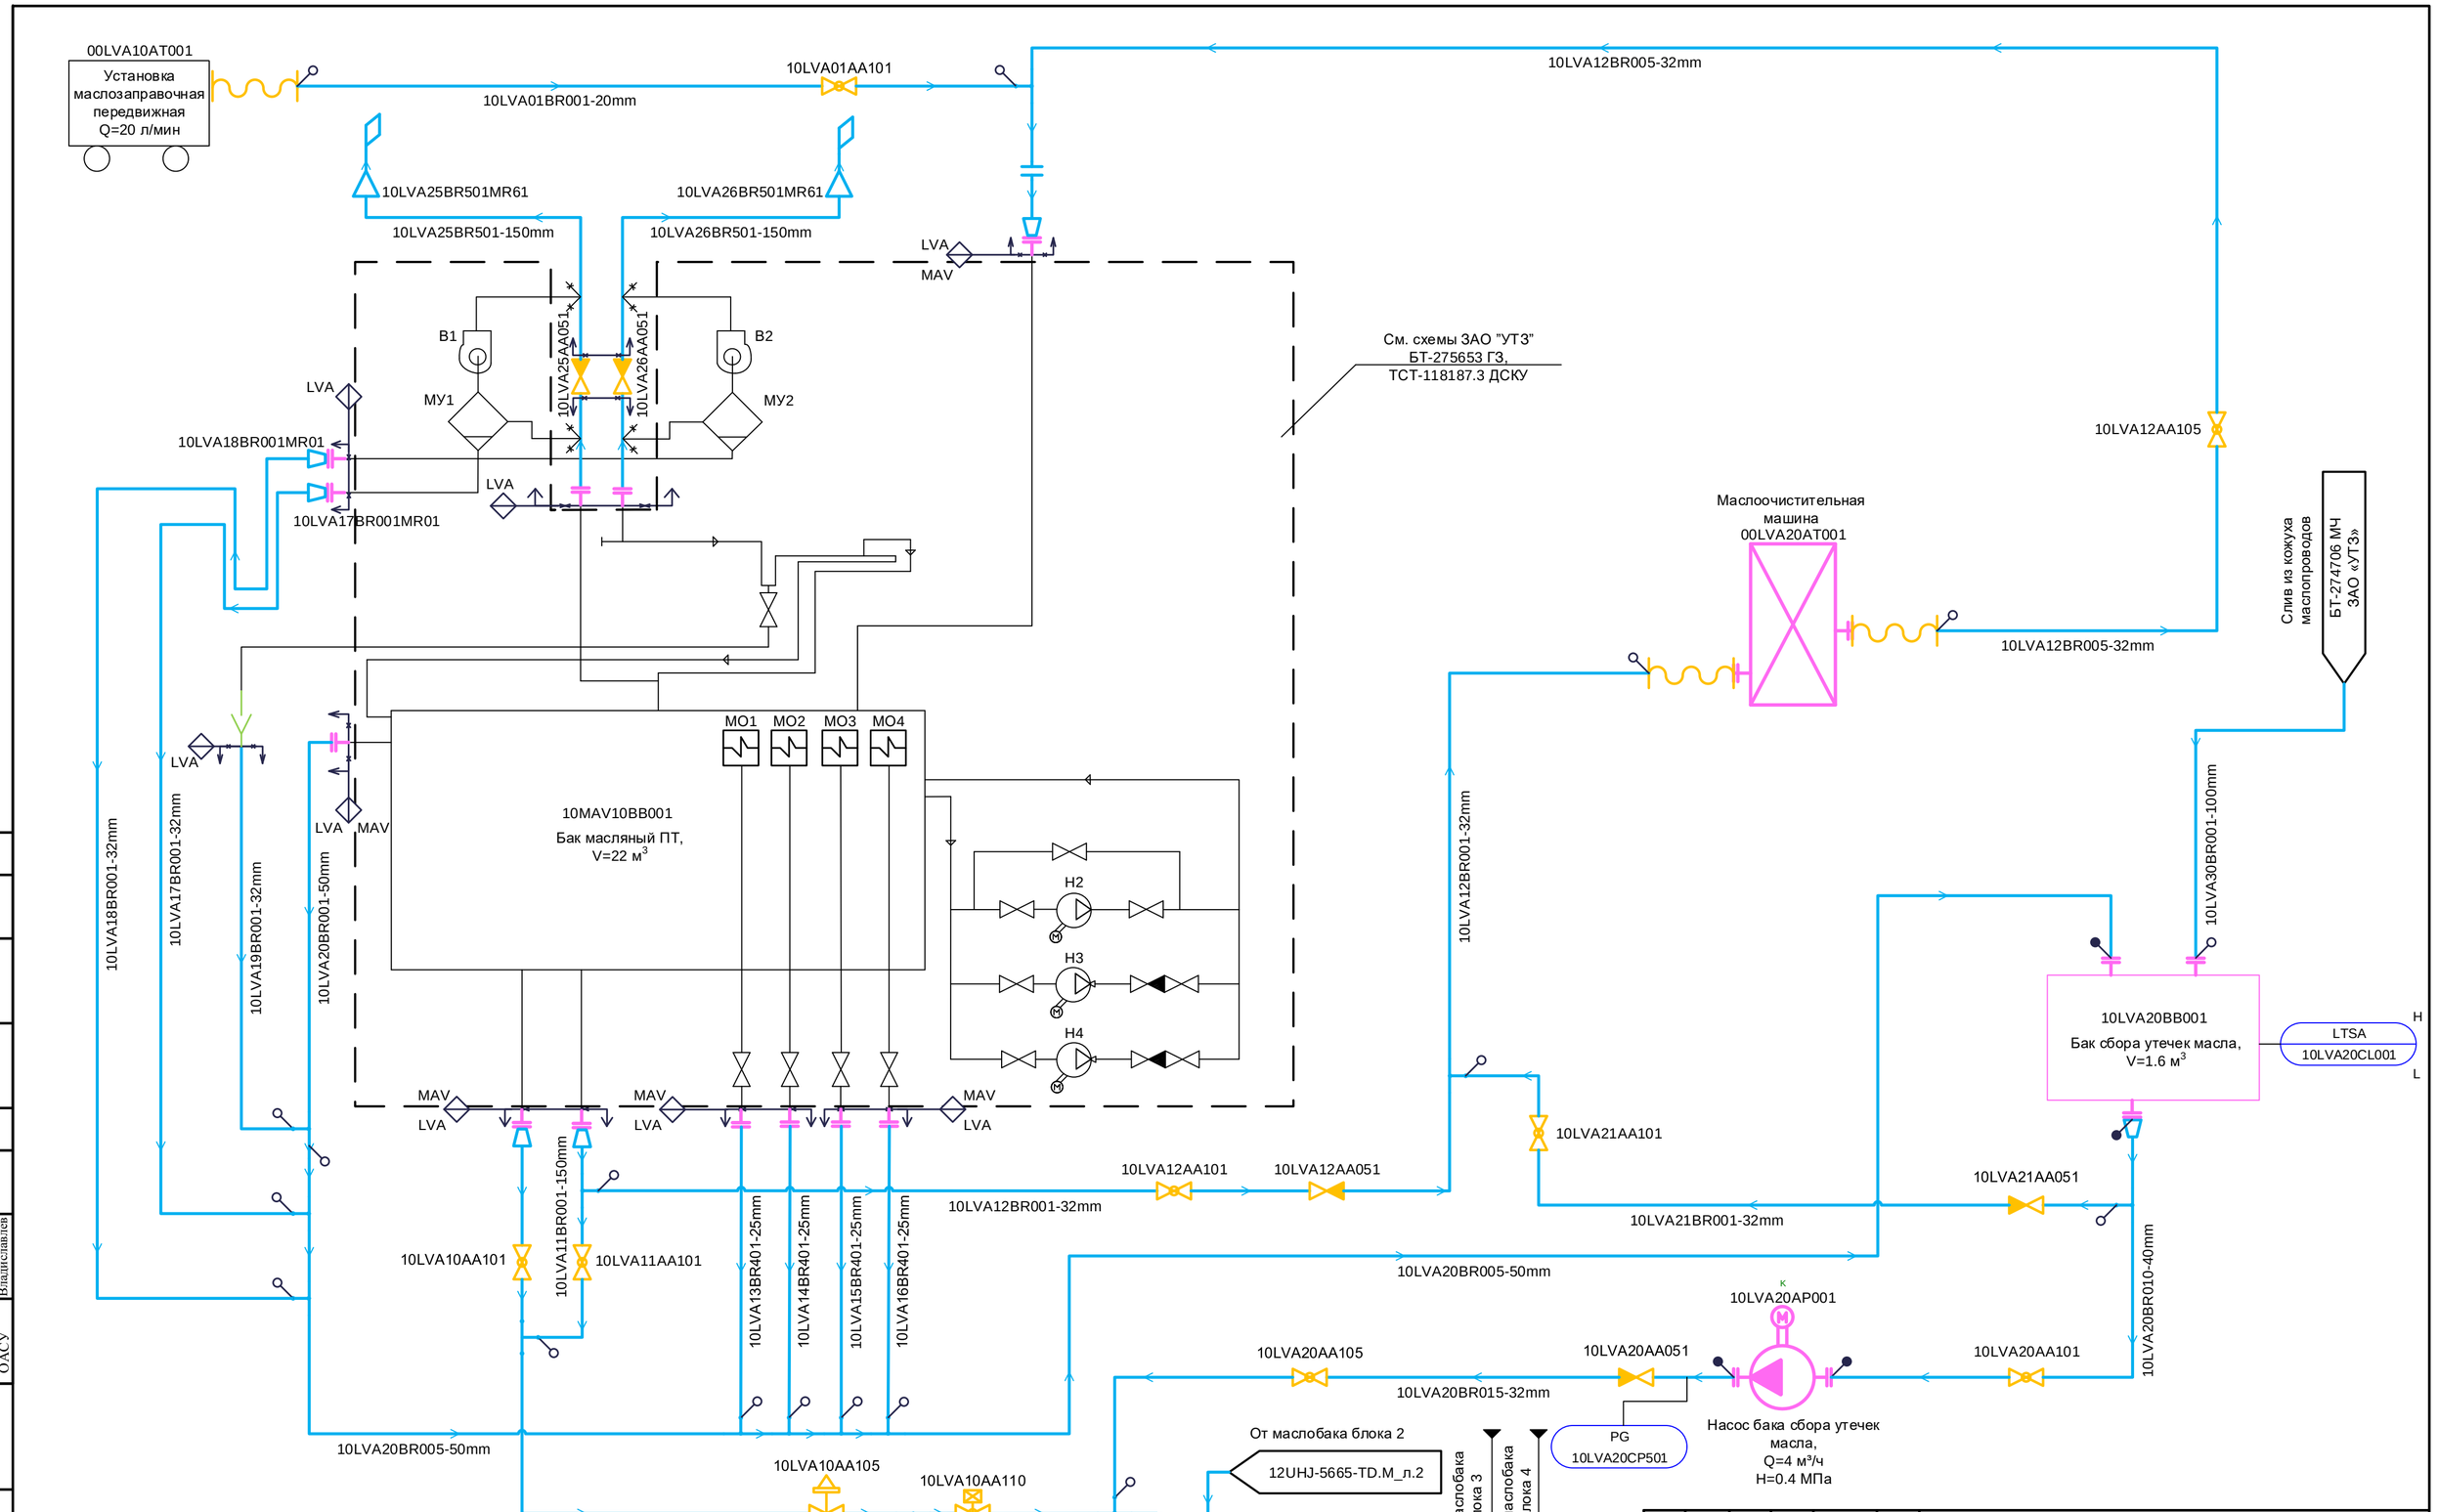

Примечание:
1. Управление насосом 10LVA20AP001 по месту.
2. При снижении уровня в баке сбора утечек масла 10LVA20BB001 до min значения отключение насоса 10LVA20AP001.
3. Сигнализация высокого уровня в баке сбора утечек масла 10LVA20BB001.
4. Задвижка 10LVA10AA105 оснащена колонковым приводом.
5. Задвижка 10LVA10AA110 оснащена замковым устройством.

Изм.	Кол.уч	Лист	№ док.	Подп.	Дата
1	-	Зам.	692-16		

Разработал	Брылева	
Проверил	Калинкина	
Нач. гр.	Бобров	
Гл. спец.	Бакатин	
Н. контр.	Гридчина	

132N32 – 11UHJ – 1210 – TD.M

Строительство Сахалинской ГРЭС-2. Основной производственный комплекс. Внутриплощадочные объекты (1очередь)

Главный корпус. PI-диаграмма трубопроводов маслосистемы

Стадия	Лист	Листов
Р	2	

PI-диаграмма трубопроводов маслосистемы. Система LVA

АКЦИОНЕРНОЕ ОБЩЕСТВО ИНСТИТУТ ТЕПЛОЭЛЕКТРОПРОЕКТ г. МОСКВА

Согласовано
ОАСУ Владиславлев
Взам. инв. №
Подпись и дата
Инв. № подл.

Формат А2