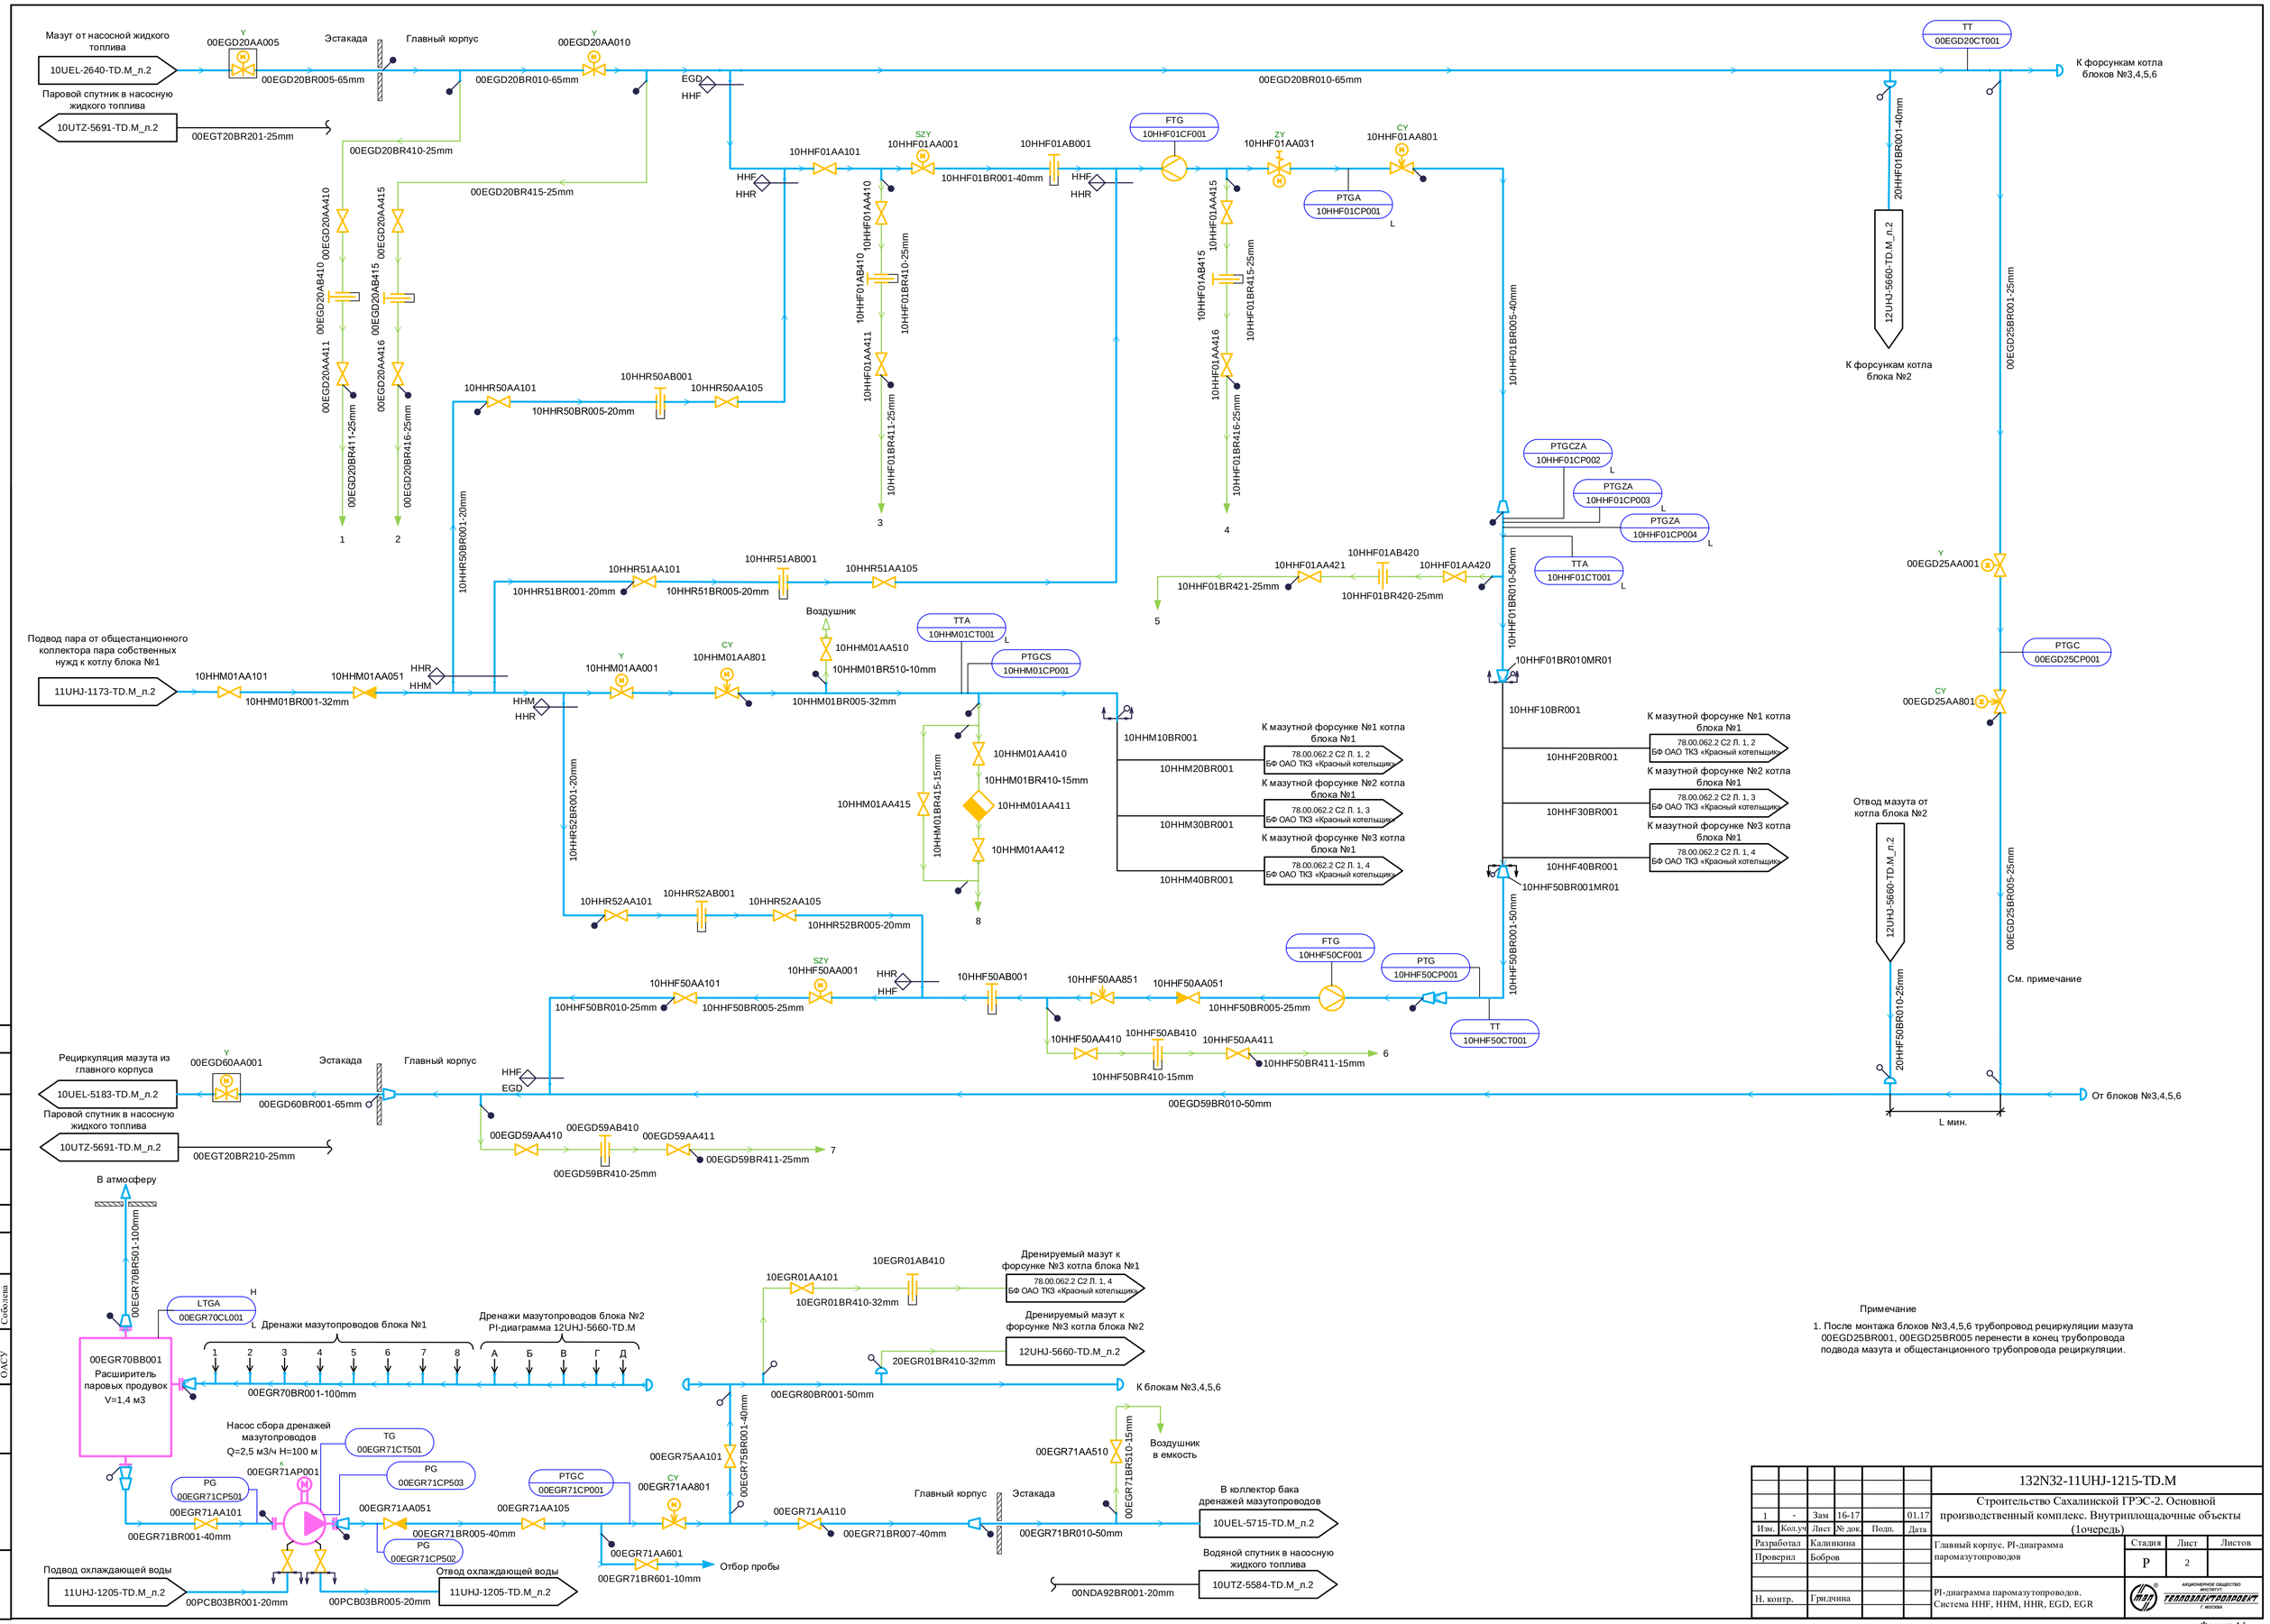

Примечание

1. После монтажа блоков №3,4,5,6 трубопровод рециркуляции мазута 00EGD25BR001, 00EGD25BR005 перенести в конец трубопровода подвода мазута и общестанционного трубопровода рециркуляции.

						132N32-11UHJ-1215-TD.M		
						Строительство Сахалинской ГРЭС-2. Основной производственный комплекс. Внутриплощадочные объекты (1очередь)		
1	-	Зам	16-17		01.17			
Изм.	Кол.уч	Лист	№ док.	Подп.	Дата			
Разработал		Калинкина				Главный корпус. PI-диаграмма паромазутопроводов	Стадия	Лист	Листов
Проверил		Бобров					Р	2	
Н. контр.		Гридчина				PI-диаграмма паромазутопроводов. Система HHF, HHM, HHR, EGD, EGR	АКЦИОНЕРНОЕ ОБЩЕСТВО ИНСТИТУТ ТЕПЛОЭЛЕКТРОПРОЕКТ Г. МОСКВА	

Согласовано

ОАСУ Соболева

Взам. инв. №

Подпись и дата

Инв. № подл.

Формат А1