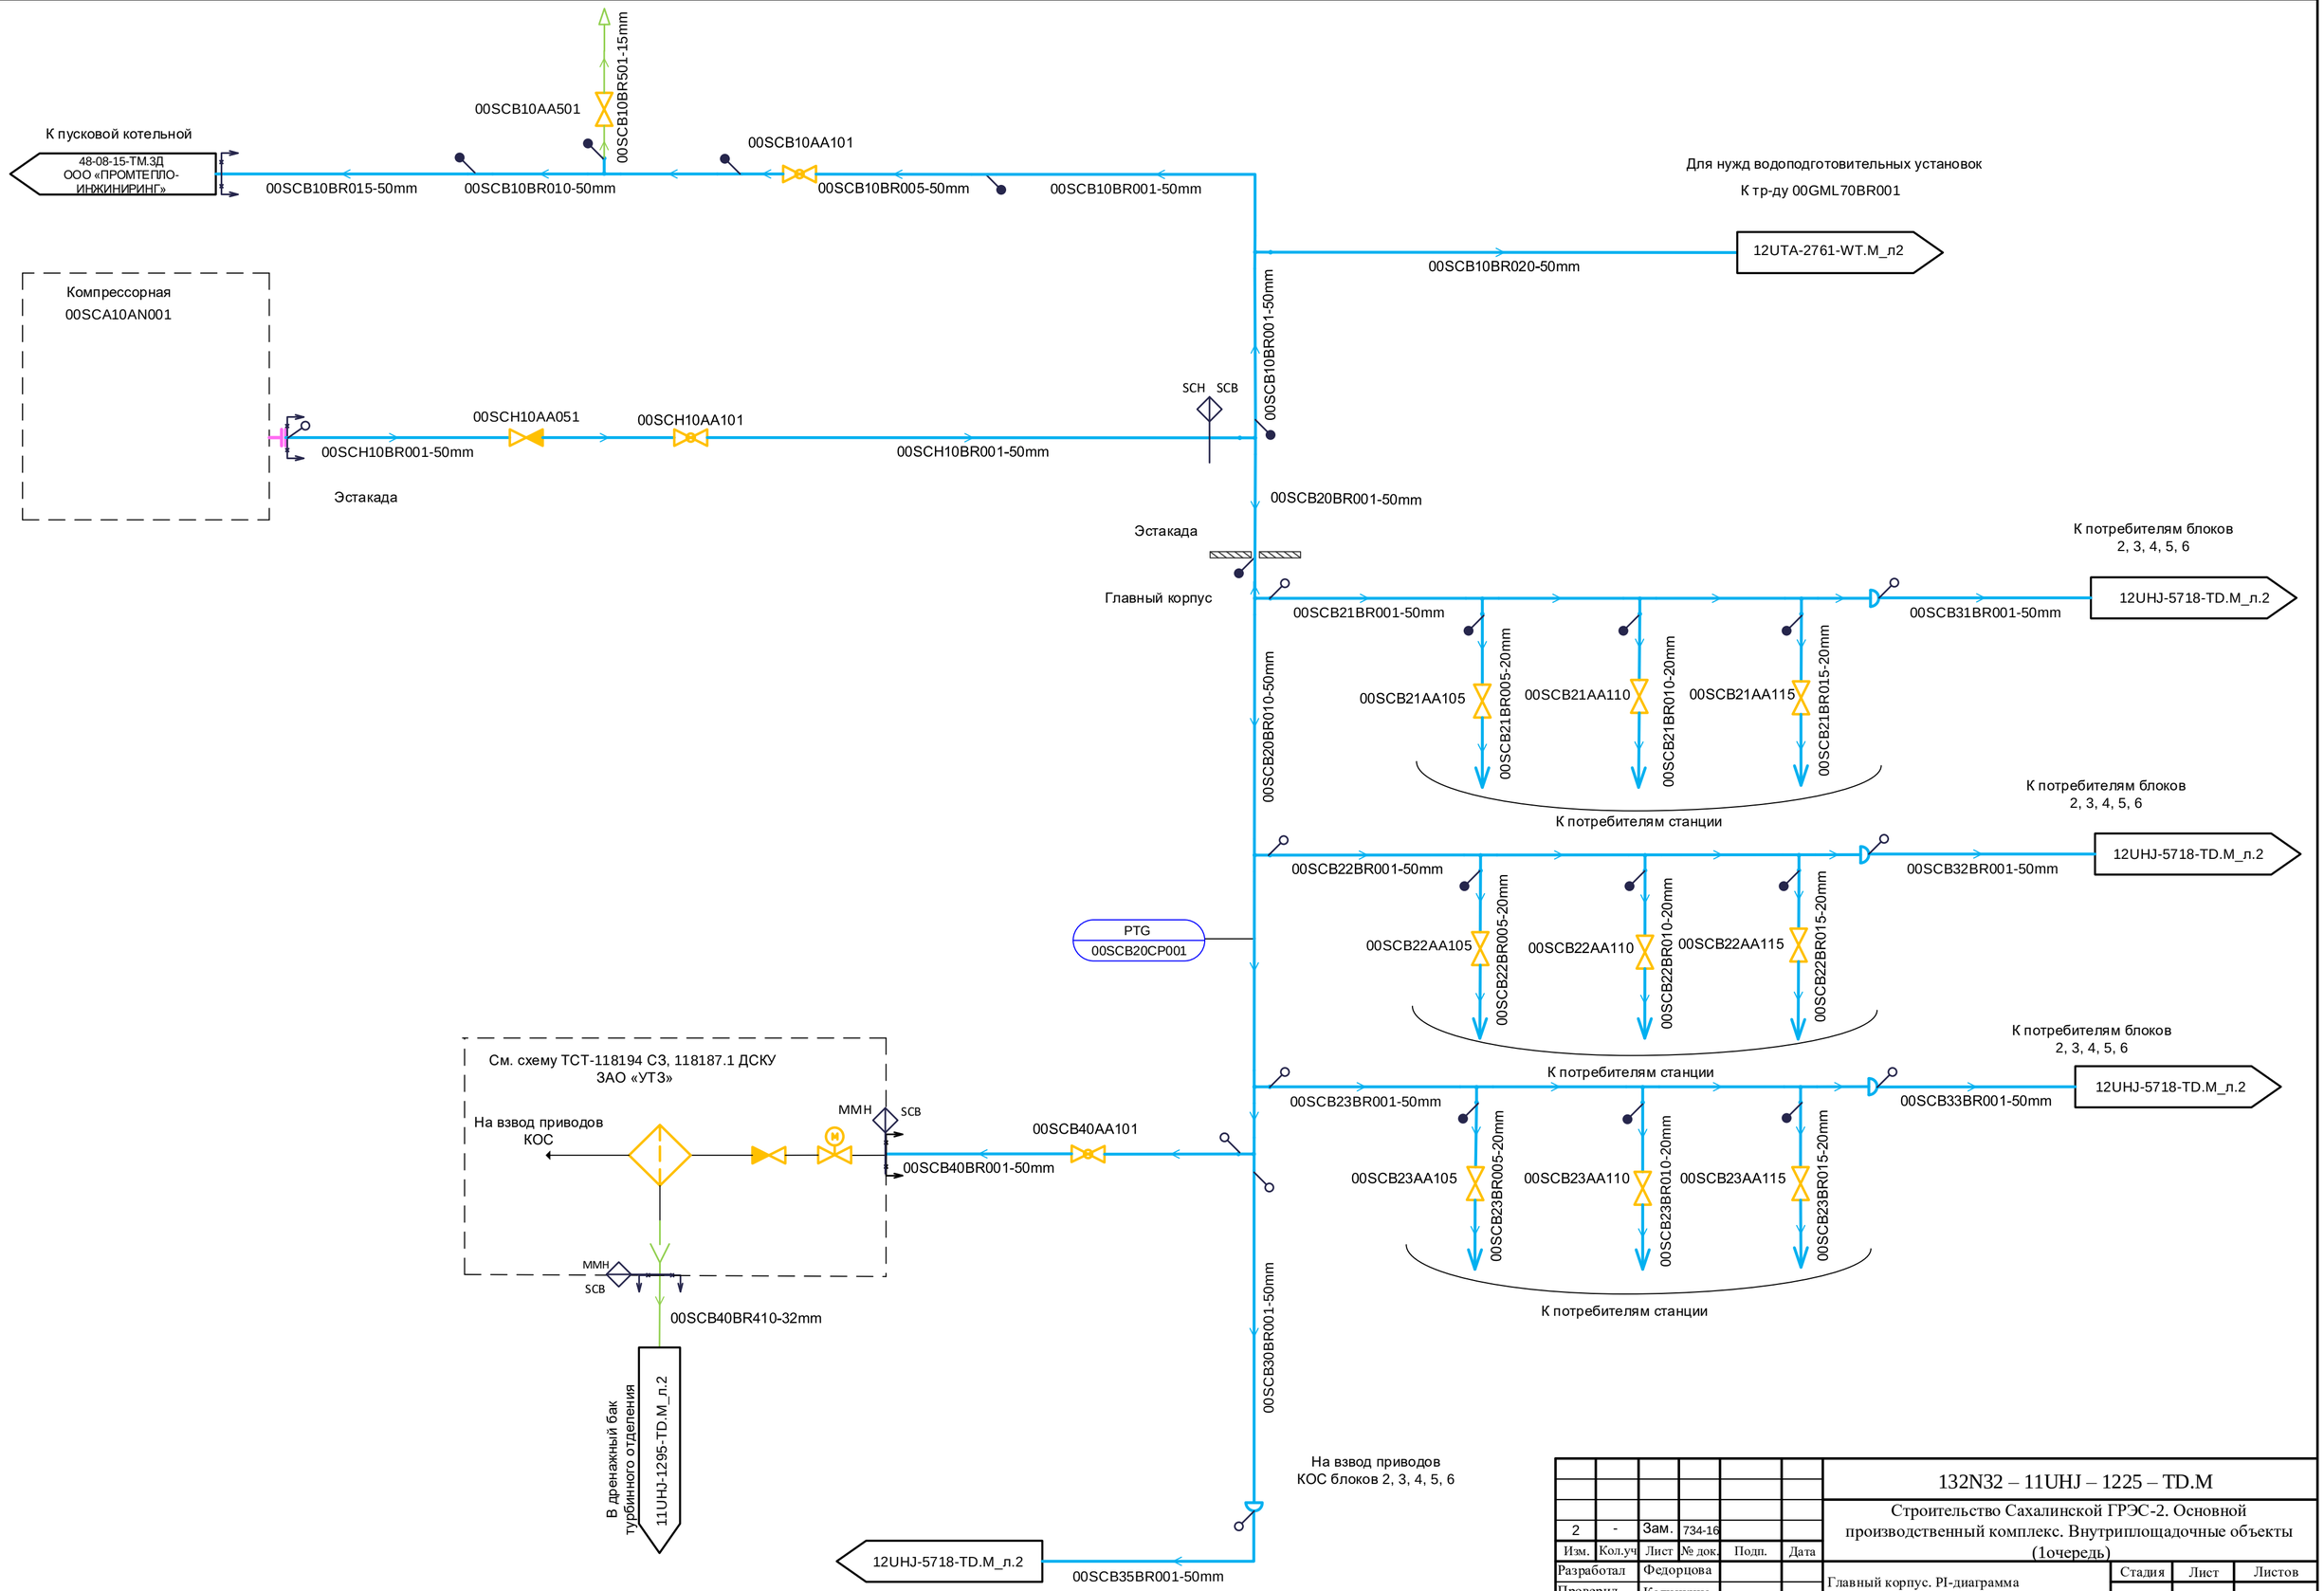

2	-	Зам.	734-16			
Изм.	Кол.уч	Лист	№ док.	Подп.	Дата	
Разработал		Федорцова				
Проверил		Калинкина				
Нач.гр.		Бобров				
Гл.спец.		Бакатин				
Н. контр.		Гридчина				

132N32 – 11UHJ – 1225 – TD.M

Строительство Сахалинской ГРЭС-2. Основной производственный комплекс. Внутриплощадочные объекты (1очередь)

Главный корпус. PI-диаграмма трубопроводов сжатого воздуха

Стадия	Лист	Листов
Р	2	

PI-диаграмма трубопроводов сжатого воздуха. Система SCH, SCB

ОТКРЫТОЕ АКЦИОНЕРНОЕ ОБЩЕСТВО ИНСТИТУТ ТЕПЛОЭЛЕКТРОПРОЕКТ МОСКВА

Согласовано

ОАСУ Владиславлев

Взам. инв. №

Подпись и дата

Инв. № подл.

Формат А2