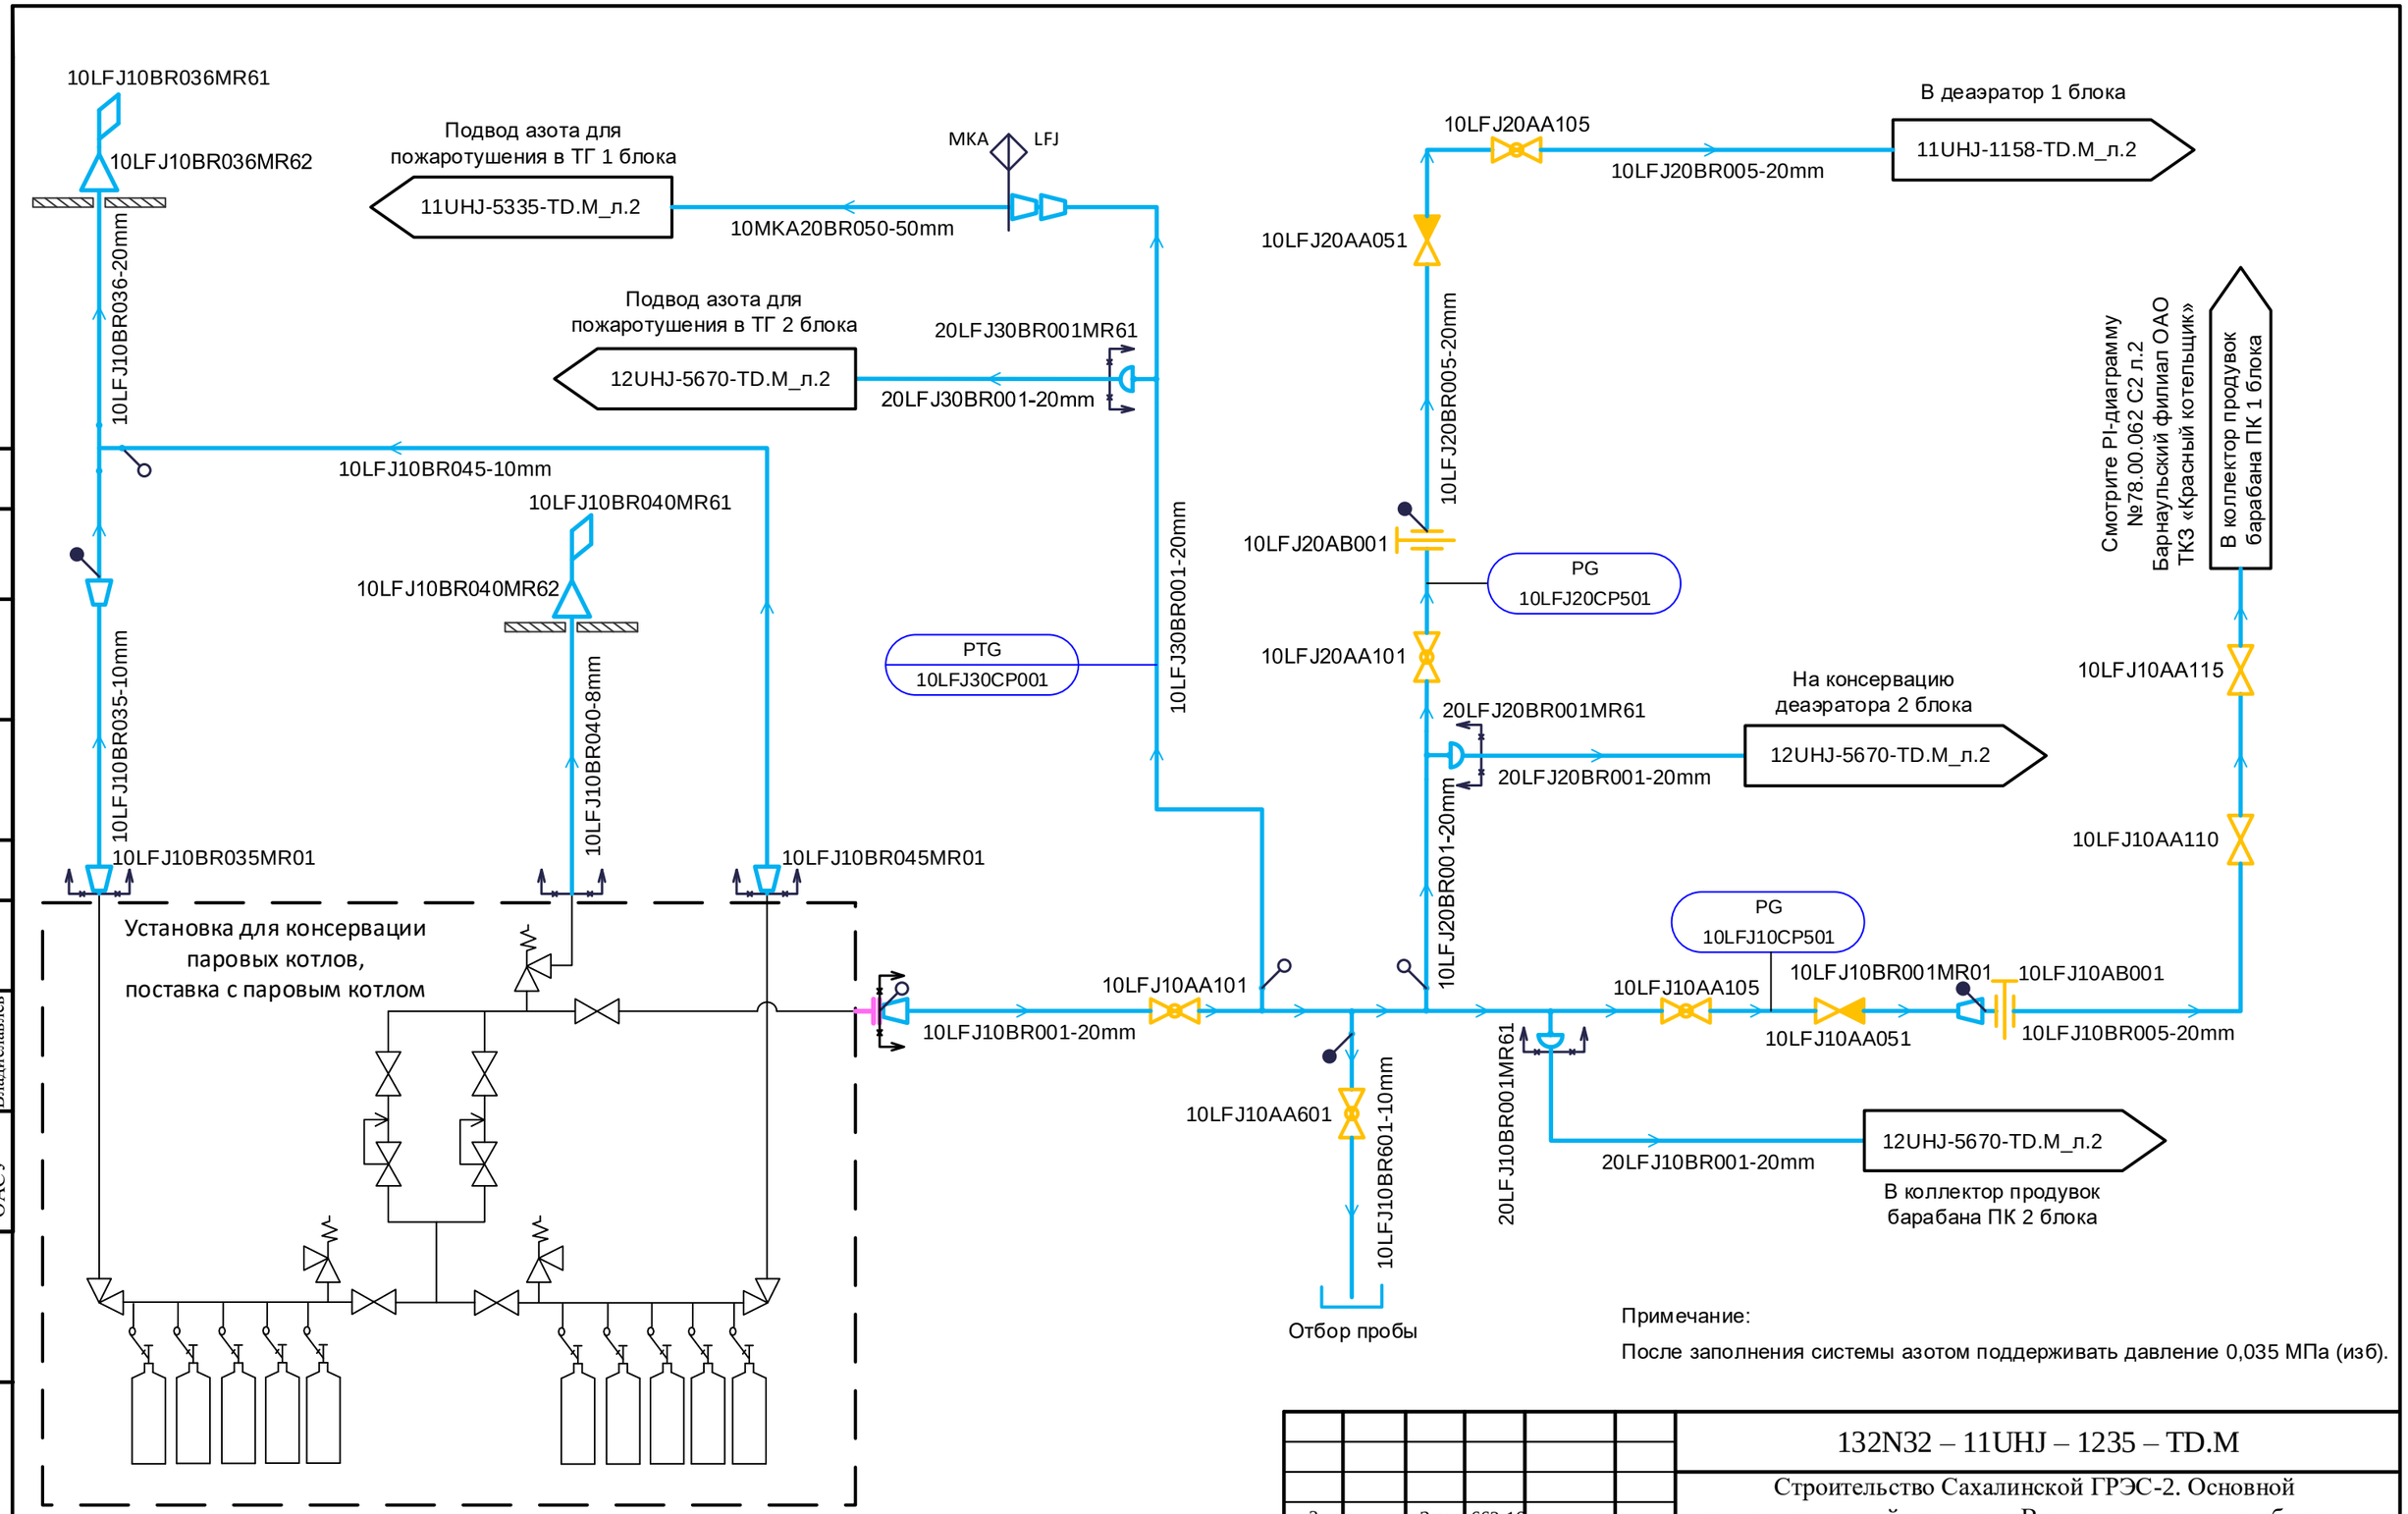

Примечание:

После заполнения системы азотом поддерживать давление 0,035 МПа (изб).

						132N32 – 11UHJ – 1235 – TD.M		
						Строительство Сахалинской ГРЭС-2. Основной производственный комплекс. Внутриплощадочные объекты (1очередь)		
2	-	Зам.	662-16					
Изм.	Кол.уч	Лист	№ док.	Подп.	Дата			
Разработал		Брылева				Главный корпус. PI-диаграмма трубопроводов азотной консервации	Стадия	Лист	Листов
Проверил		Калинкина					Р	2	
Нач. гр.		Бобров							
Гл. спец.		Бакатин				PI-диаграмма трубопроводов азотной консервации. Система LFJ	АКЦИОНЕРНОЕ ОБЩЕСТВО ИНСТИТУТ ТЕПЛОЭЛЕКТРОПРОЕКТ Г. МОСКВА		
Н. контр.		Гридчина							

Согласовано

ОАСУ Владиславлев

Взам. инв. №

Подпись и дата

Инв. № подл.

Формат А3