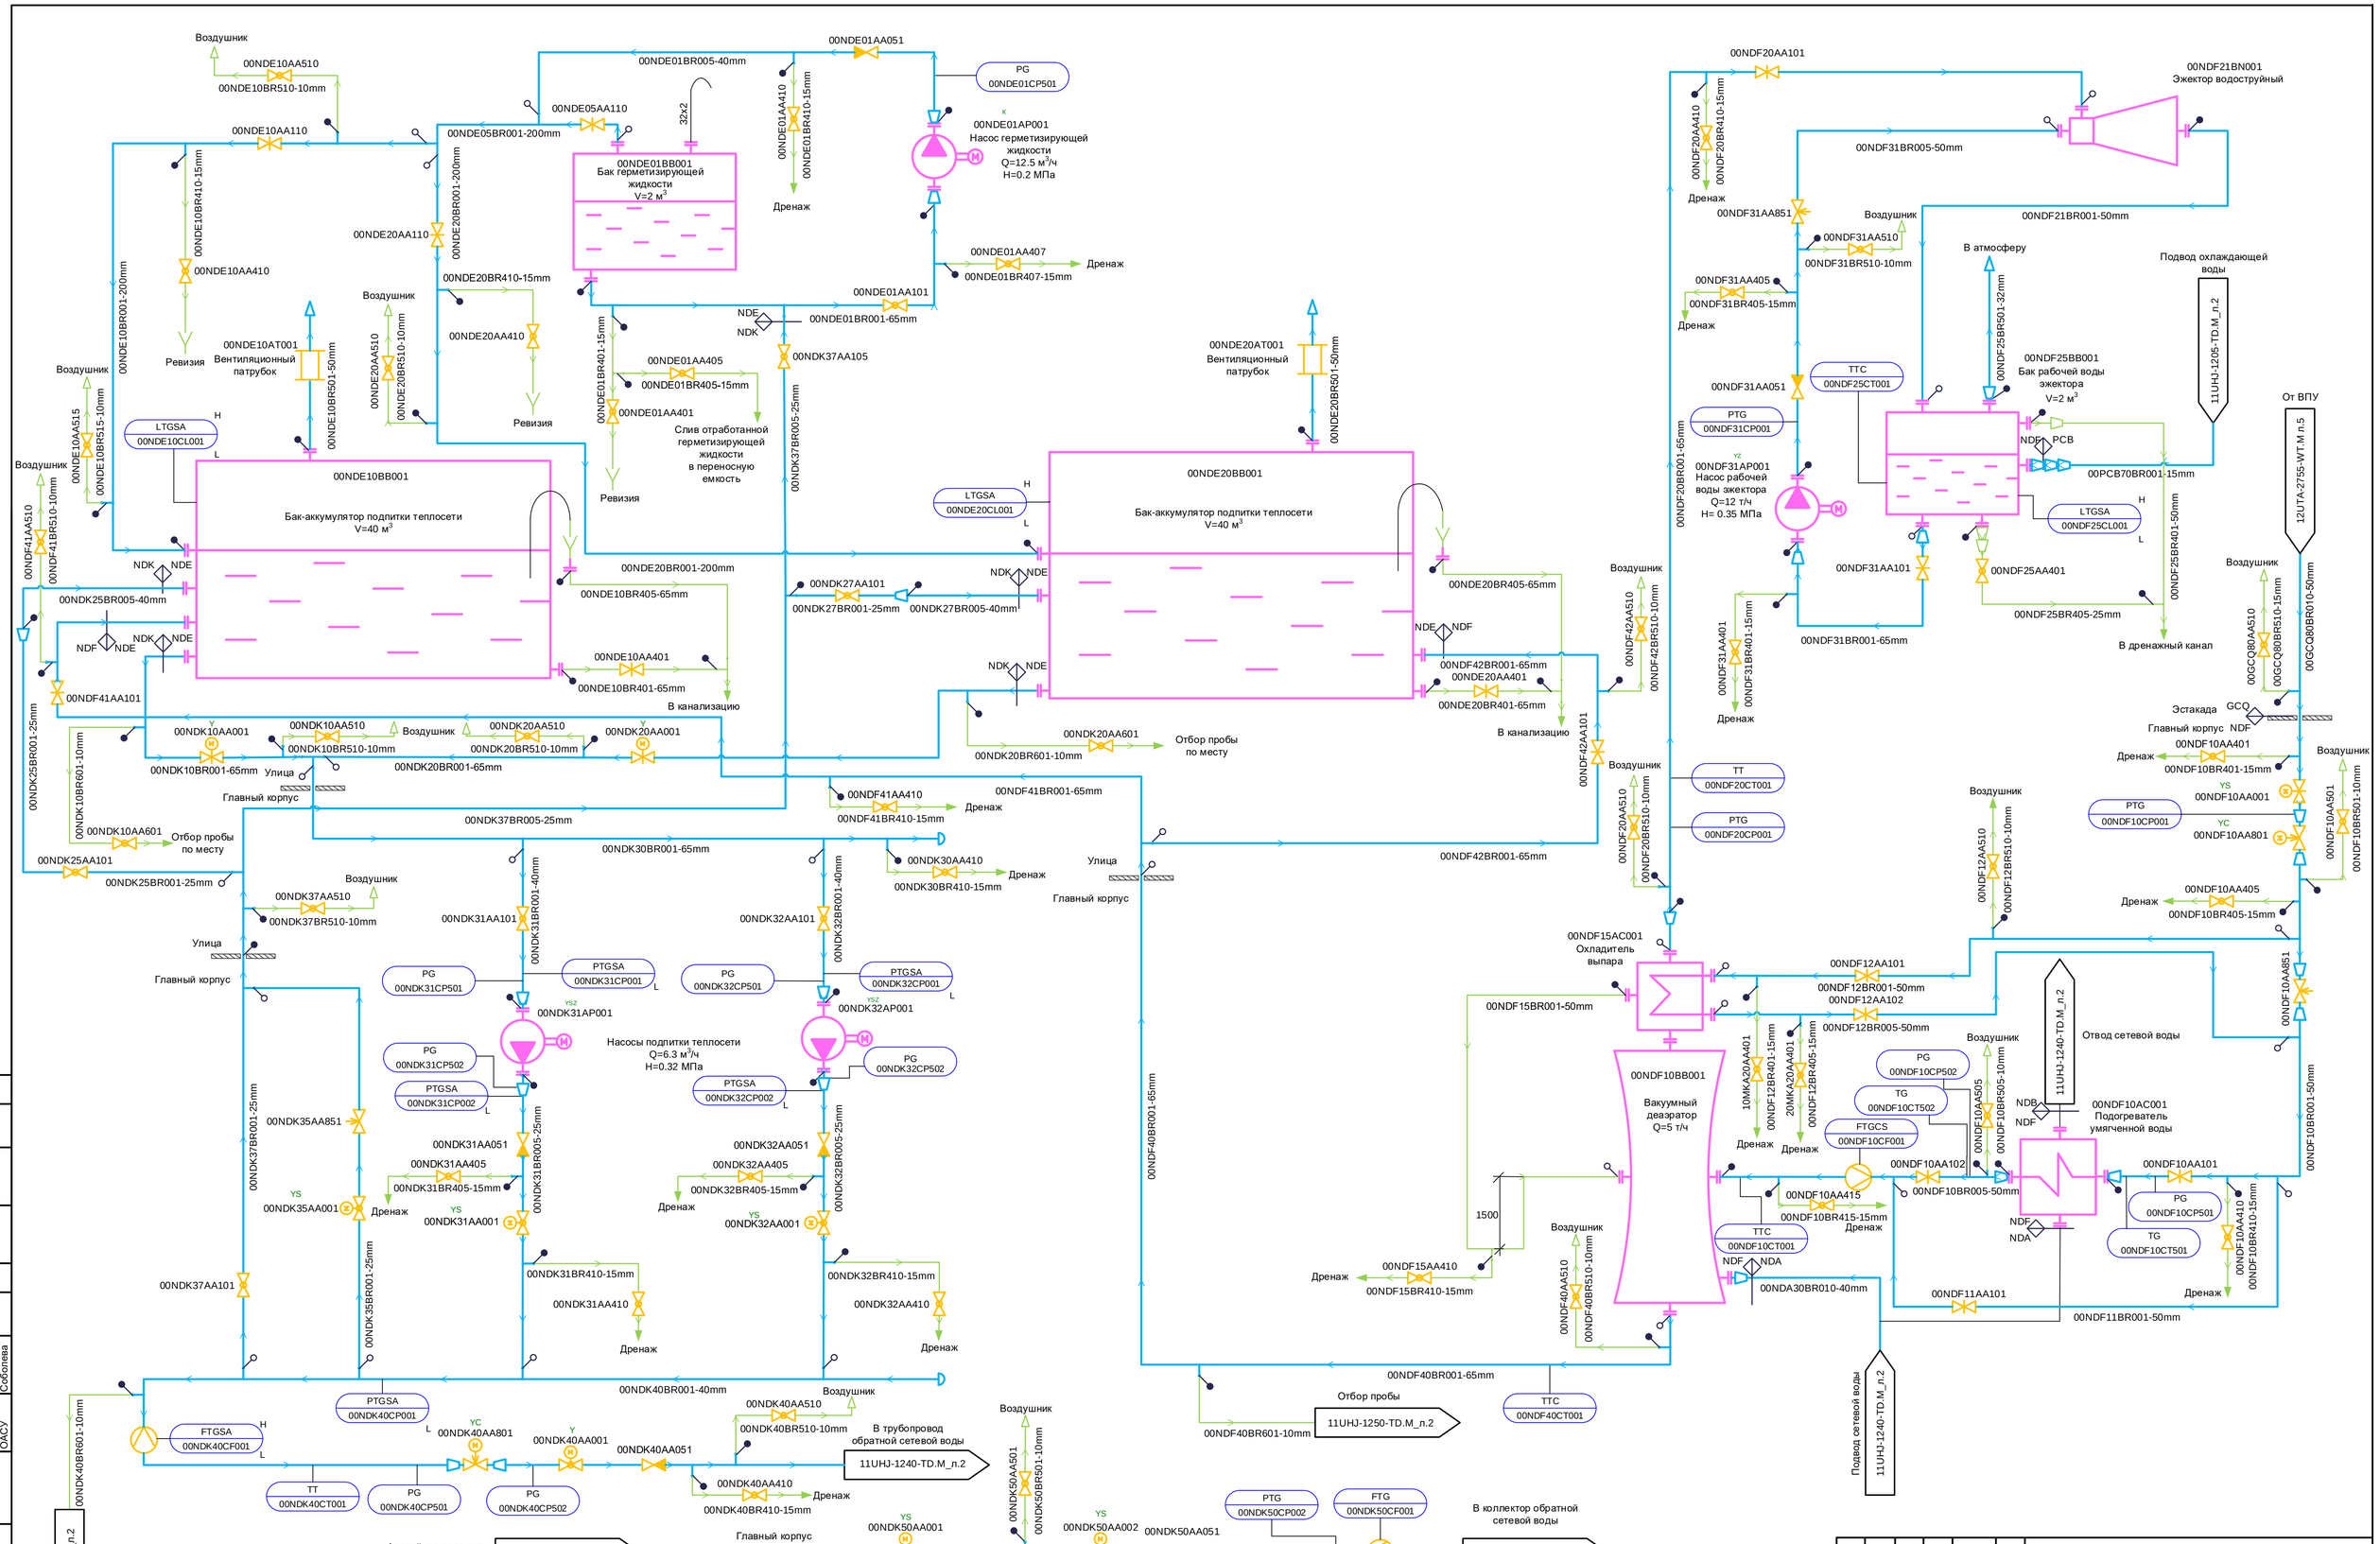

1	-	Зам.	1042-16		12.16	132N32-11UHJ-1245-TD.M
Изм.	Кол.уч	Лист	№ док.	Подп.	Дата	Строительство Сахалинской ГРЭС-2. Основной производственный комплекс. Внутриплощадочные объекты (1-ая очередь)
Разработал		Захарова				Главный корпус. PI-диаграмма трубопроводов подпитки теплосети
Проверил		Калинкина				Стадия: Р; Лист: 2; Листов:
Нач.группы		Бобров				
Гл.спец.		Бакатин				PI-диаграмма трубопроводов подпитки теплосети. Система NDE, NDK, NDF.
Н. контр.		Черемушкина				АКЦИОНЕРНОЕ ОБЩЕСТВО ИНСТИТУТ ТЕПЛОЭЛЕКТРОПРОЕКТ г. МОСКВА

Согласовано: ОАСУ Соболева

Взам. инв. №

Подпись и дата

Инв. № подл.

Формат А1