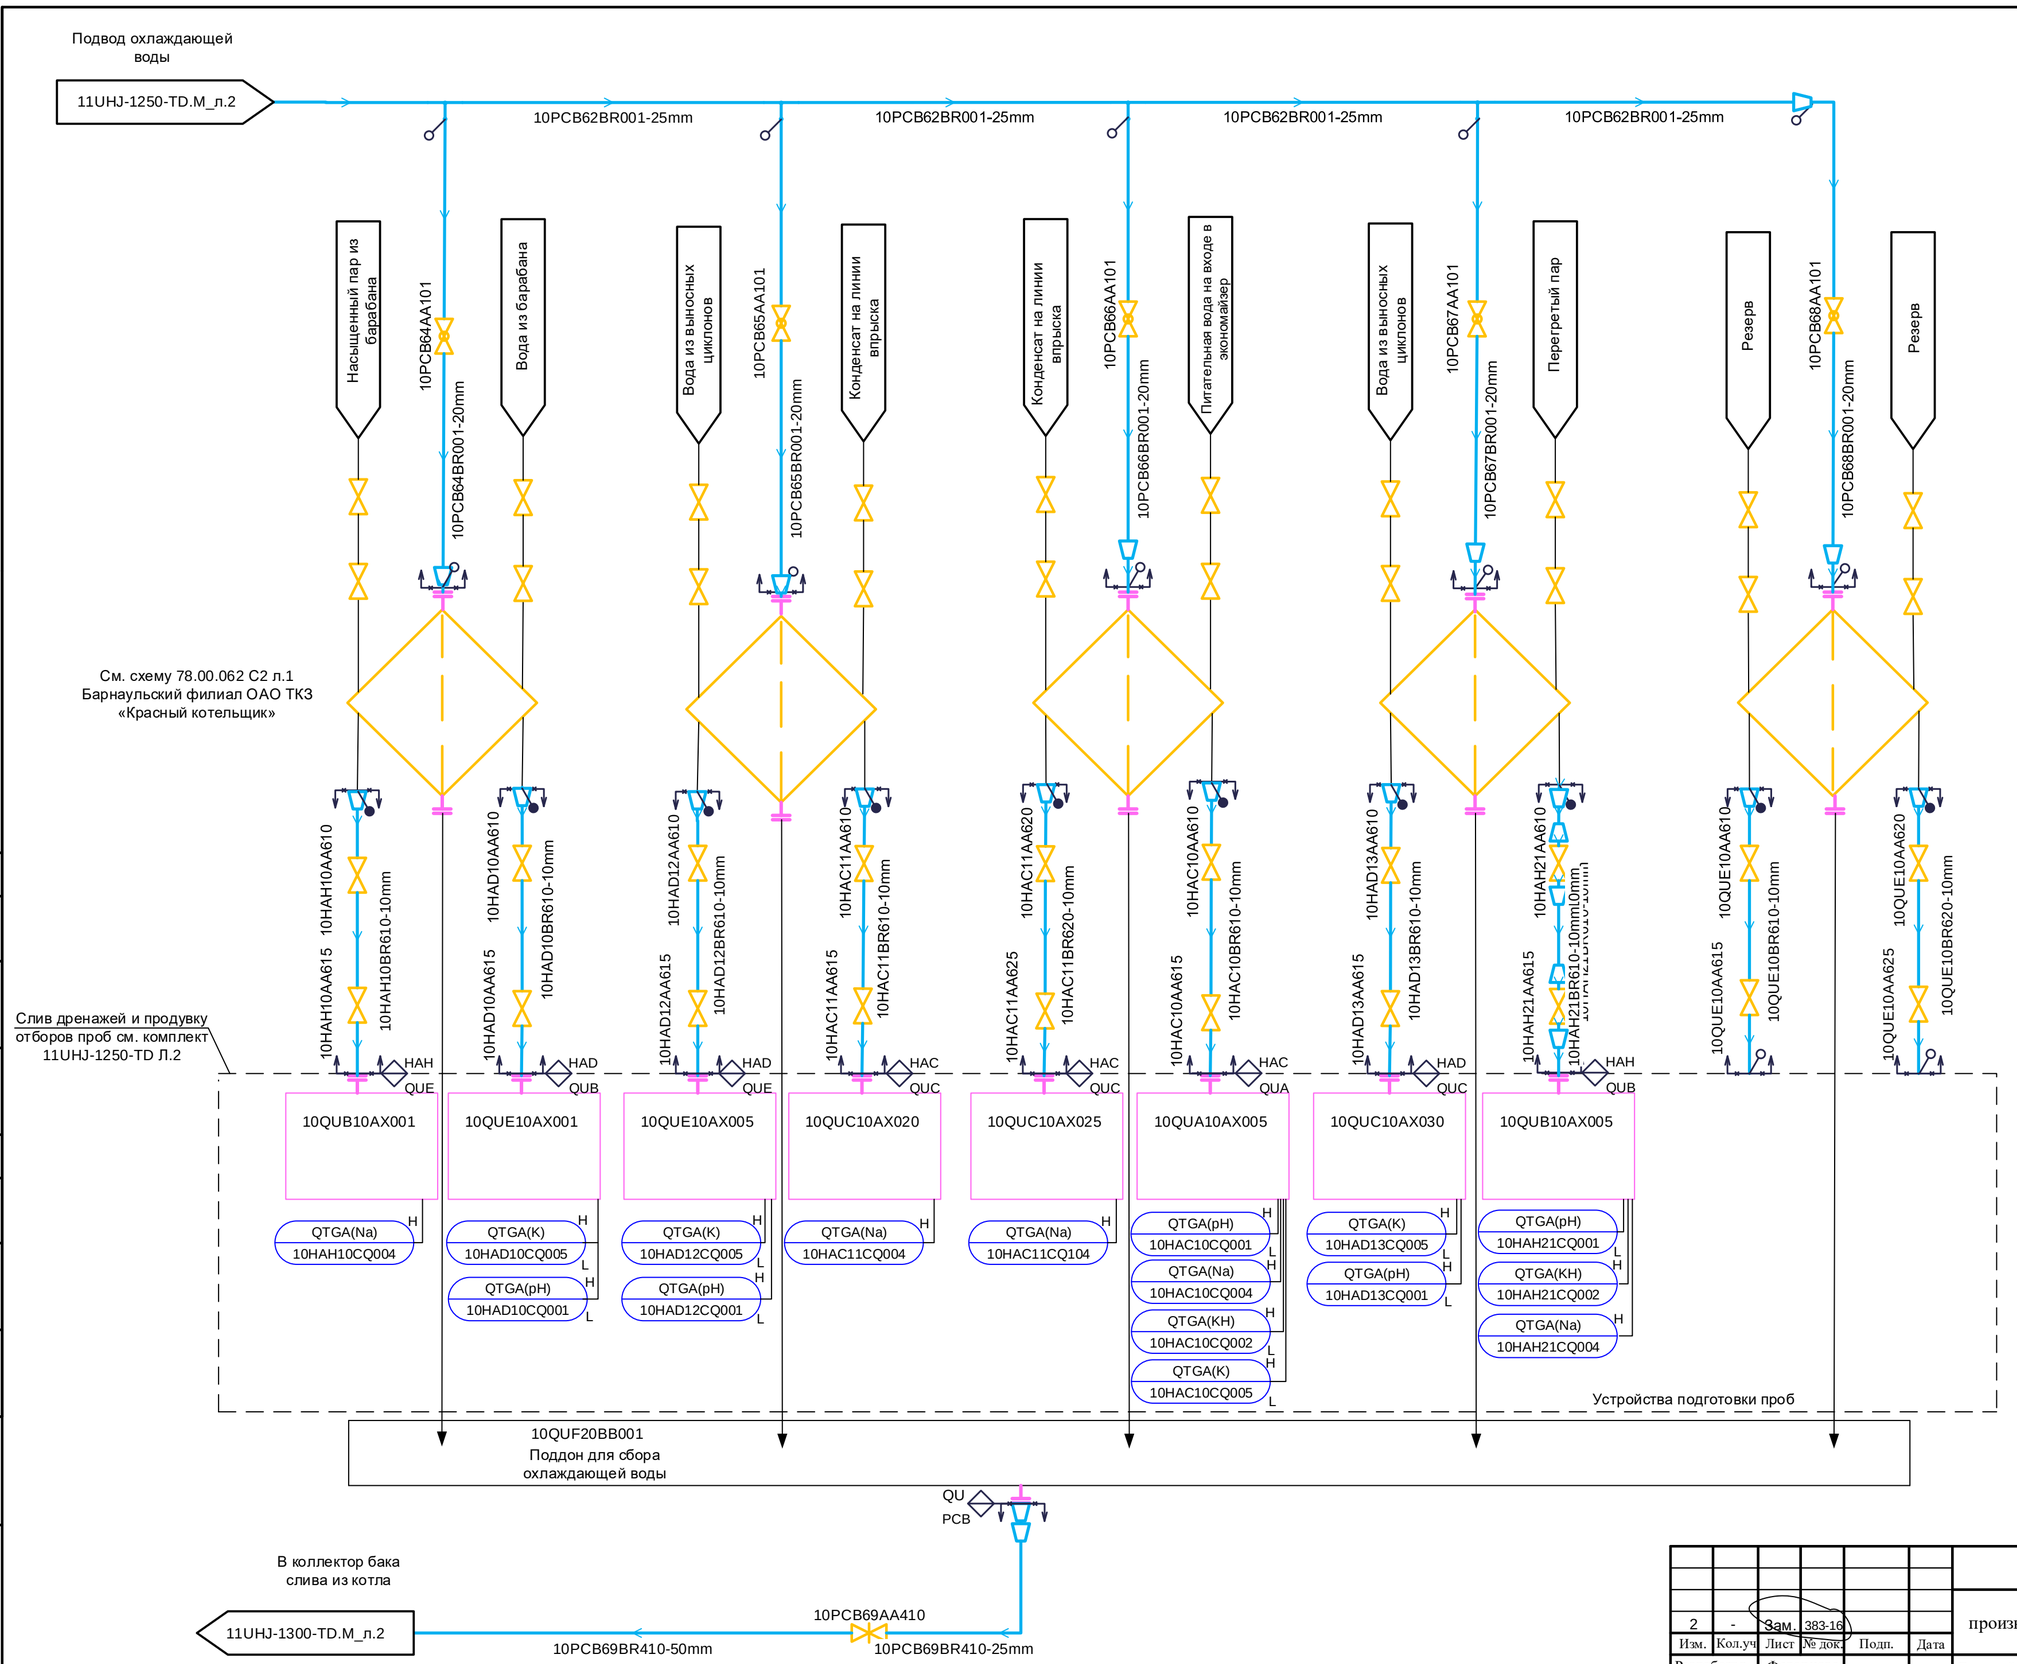

2	-	Зам.	383-16			
Изм.	Кол.уч	Лист	№ док.	Подп.	Дата	
Разработал		Федорцова				
Проверил		Калинкина				
Нач.гр.		Попова				
Гл.спец.		Бакатин				
Н. контр.		Гридчина				

132N32 – 11UHJ – 1250 – TD.M

Строительство Сахалинской ГРЭС-2. Основной производственный комплекс. Внутриплощадочные объекты (1 очередь)

Главный корпус. PI-диаграмма трубопроводов отборов проб пара и воды котла

Стадия	Лист	Листов
Р	3	

PI-диаграмма трубопроводов отборов проб пара и воды котла. Системы QUC, QUA, QUE, QUB, PCB

АКЦИОНЕРНОЕ ОБЩЕСТВО ИНСТИТУТ ТЕПЛОЭЛЕКТРОПРОЕКТ Г. МОСКВА

Согласовано

Владиславлев

ОАСУ

Взам. инв. №

Подпись и дата

Инв. № подл.

Формат А2