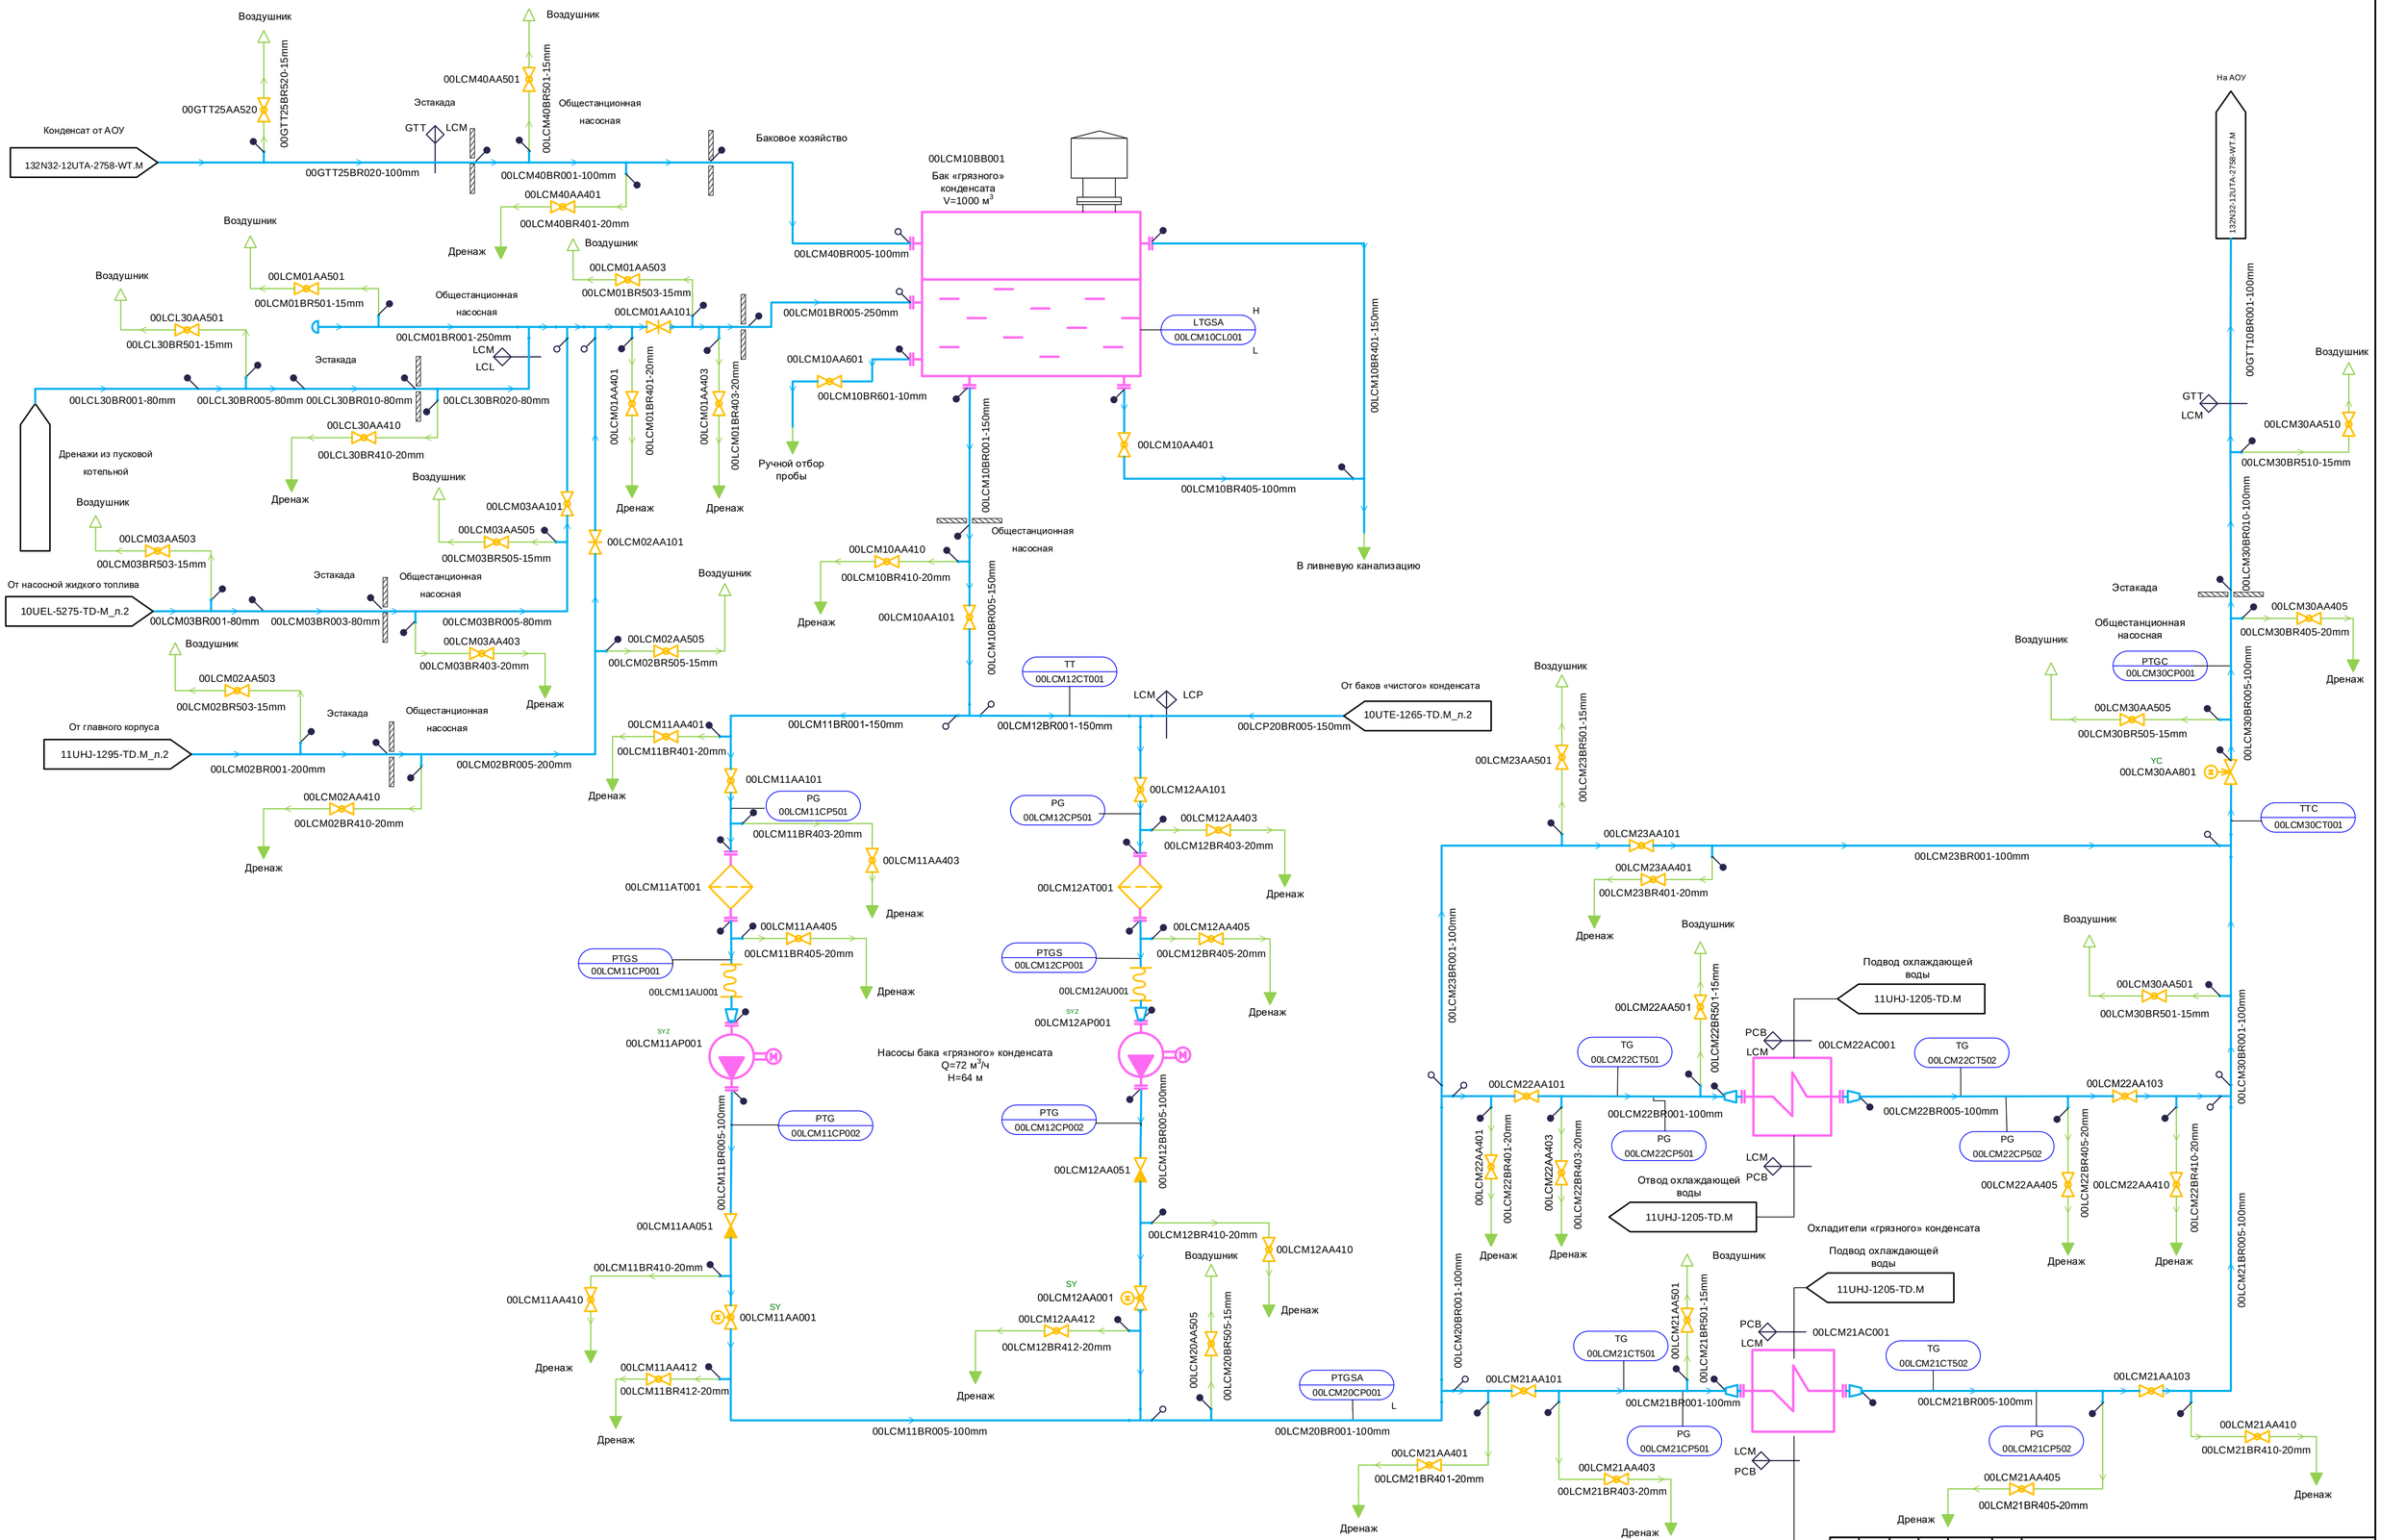

1	-	Зам.	681-16			
Изм.	Кол.уч	Лист	№ док.	Подп.	Дата	
Разработал		Захарова				
Проверил		Калинкина				
Гл.спец.		Бакатин				
Н. контр.		Черемушкина				

132N32-10UTE-1275-TD.M

Строительство Сахалинской ГРЭС-2.
Основной производственный комплекс. Внутриплощадочные объекты
(1-ая очередь)

Общестанционная насосная с баковым хозяйством.
PI-диаграмма трубопроводов «грязного» конденсата.

PI-диаграмма трубопроводов «грязного» конденсата. Система LCM, LCP

Стадия	Лист	Листов
Р	2	

АКЦИОНЕРНОЕ ОБЩЕСТВО ИНСТИТУТ ТЕПЛОЭЛЕКТРОПРОЕКТ г. МОСКВА

Согласовано
ОАСУ Соболева
Взам. инв. №
Подпись и дата
Инв. № подл.

Формат А1