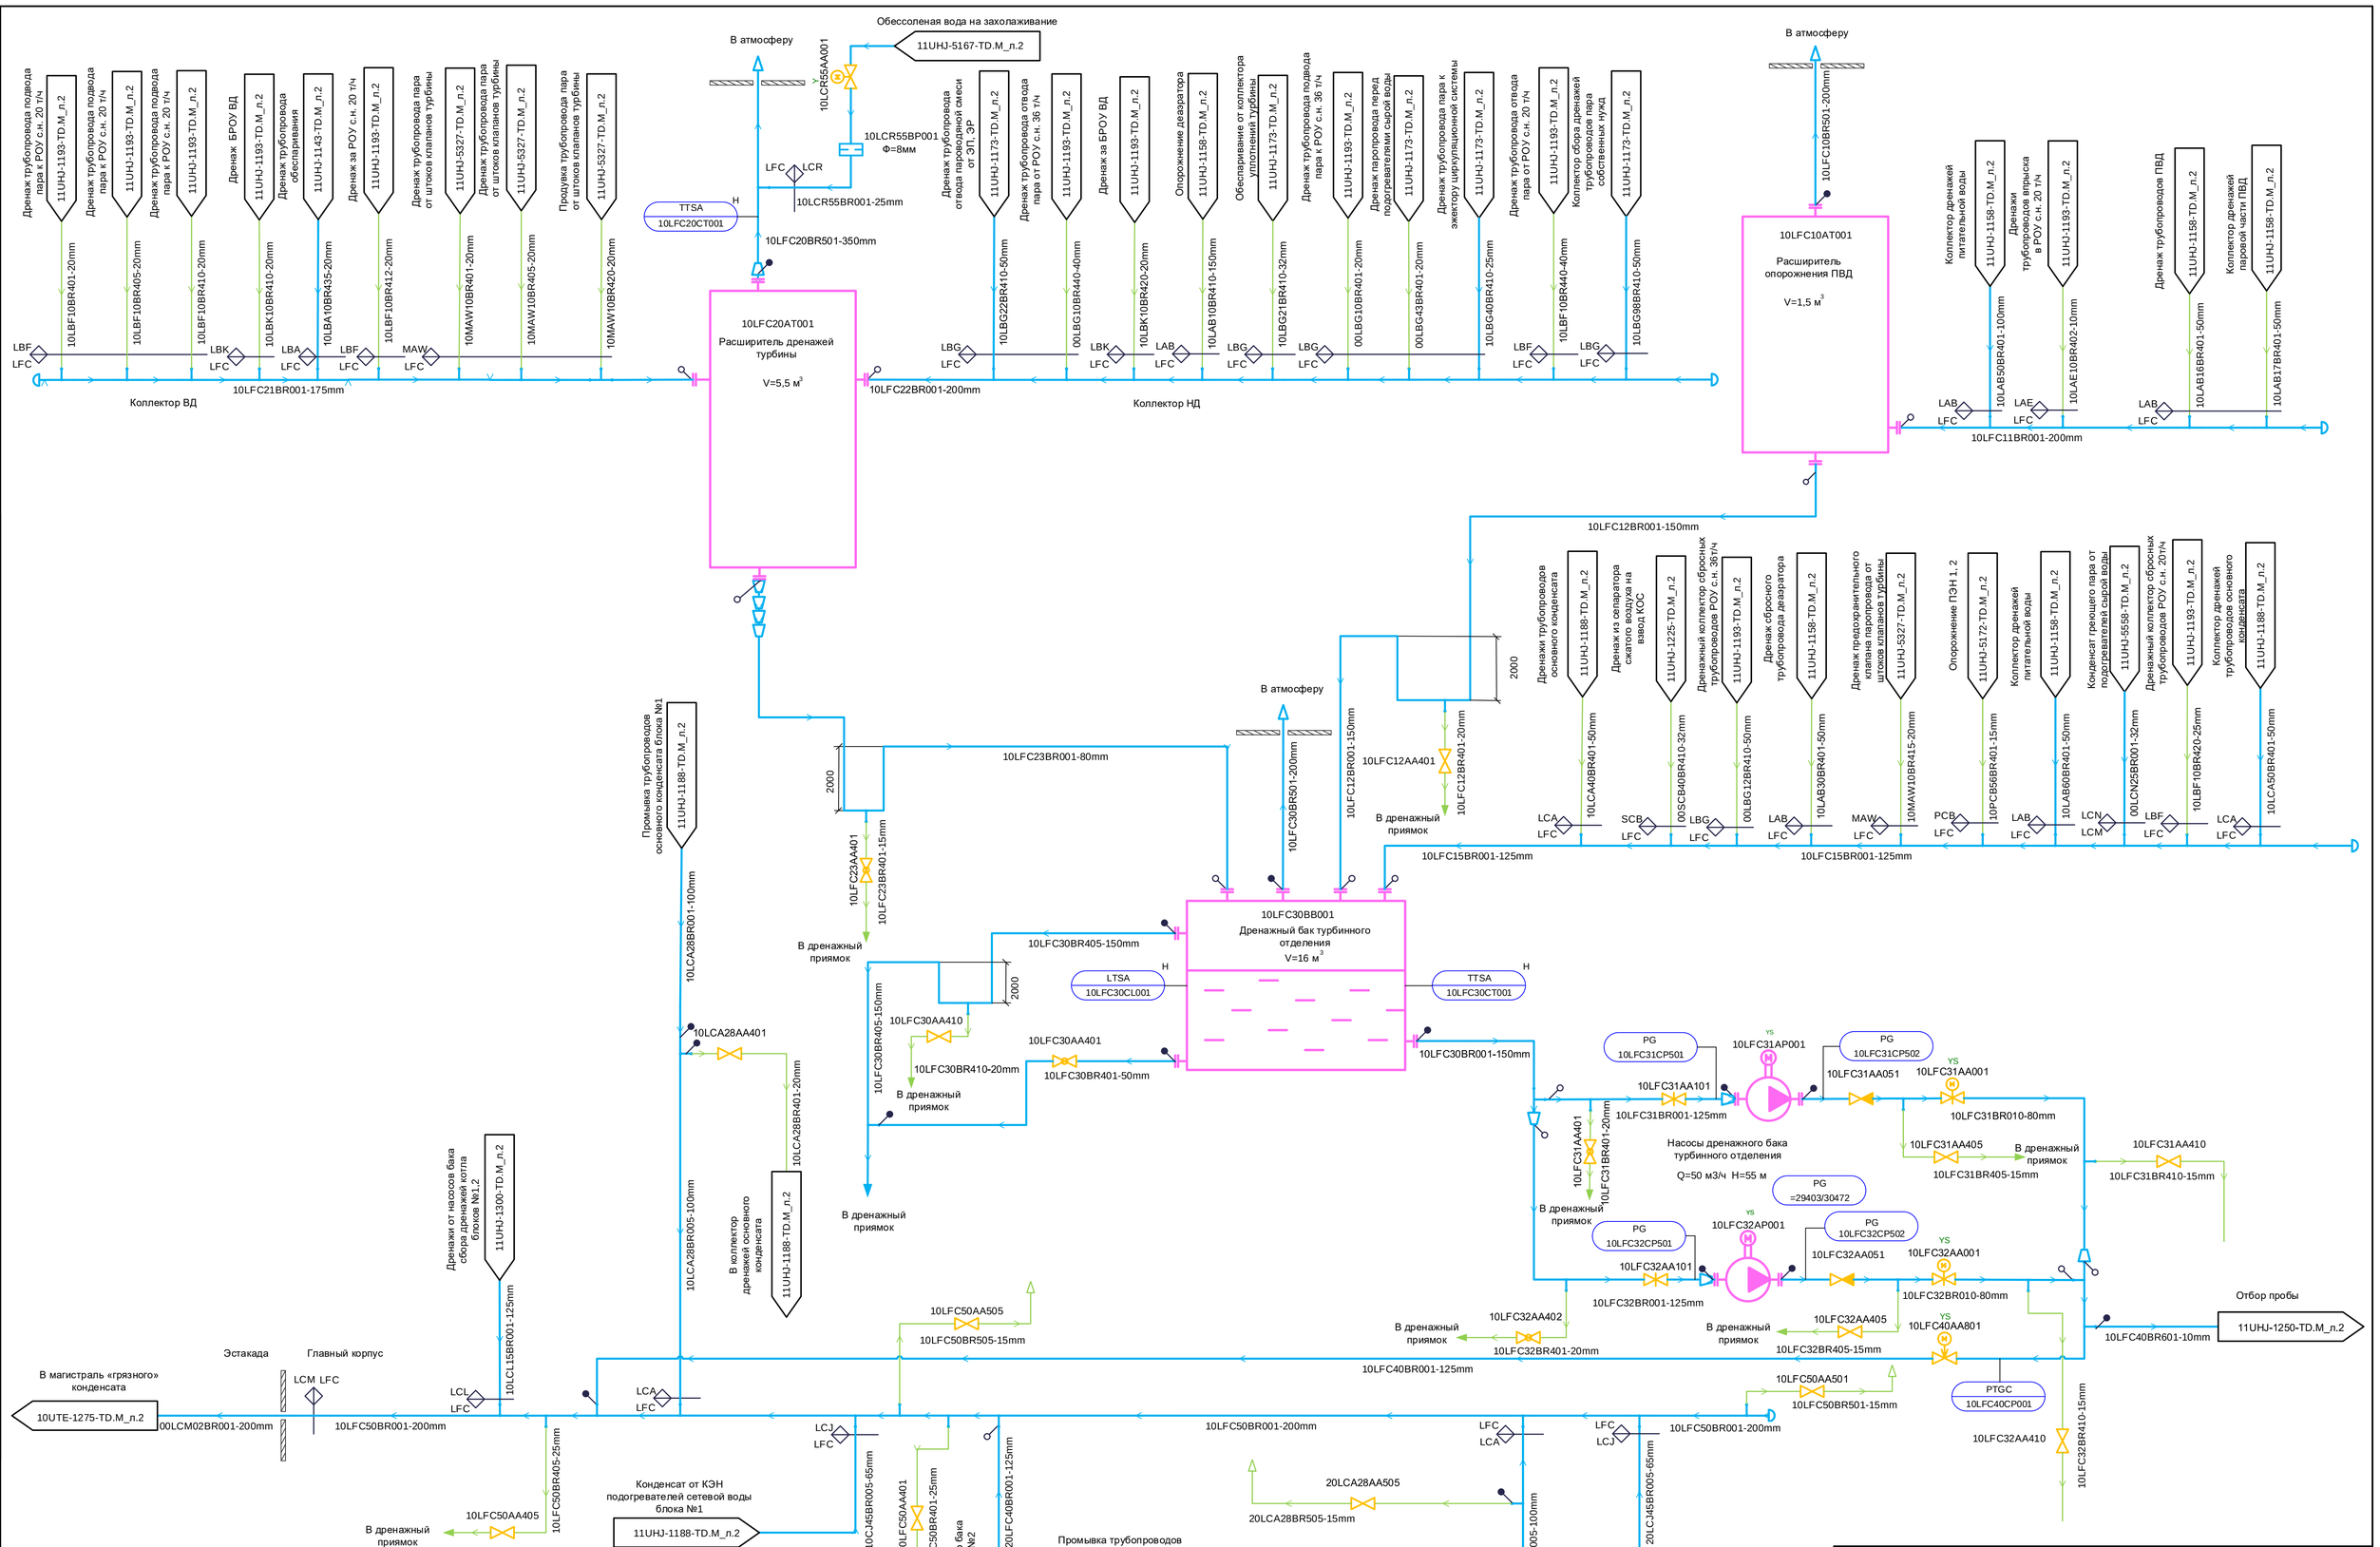


| | | | | | | | |
|---|---|---|---|---|---|---|---|
| 1 | - | Зам. | 627-16 | | | | |
| Изм. | Кол.уч | Лист | № док. | Подп. | Дата | | |
| Разработал | | Федорцова | | | | Главный корпус. PI-диаграмма трубопроводов дренажей турбинного отделения | Стадия: Р; Лист: 2; Листов: |
| Проверил | | Калинкина | | | | PI-диаграмма трубопроводов дренажей турбинного отделения. Система LFC , LCM | АКЦИОНЕРНОЕ ОБЩЕСТВО ВНИИГИНО ТЕПЛОЭЛЕКТРОПРОЕКТ Г. МОСКВА |
| Нач.гр. | | Бобров | | | | | |
| Гл.спец. | | Бакатин | | | | | |
| Н. контр. | | Гридчина | | | | | |

132N32 – 11UHJ – 1295 – TD.M

Строительство Сахалинской ГРЭС-2. Основной производственный комплекс. Внутриплощадочные объекты (1очередь)

Согласовано: ОАСУ Соболева

Взам. инв. №

Подпись и дата

Инв. № подл.

Формат А1