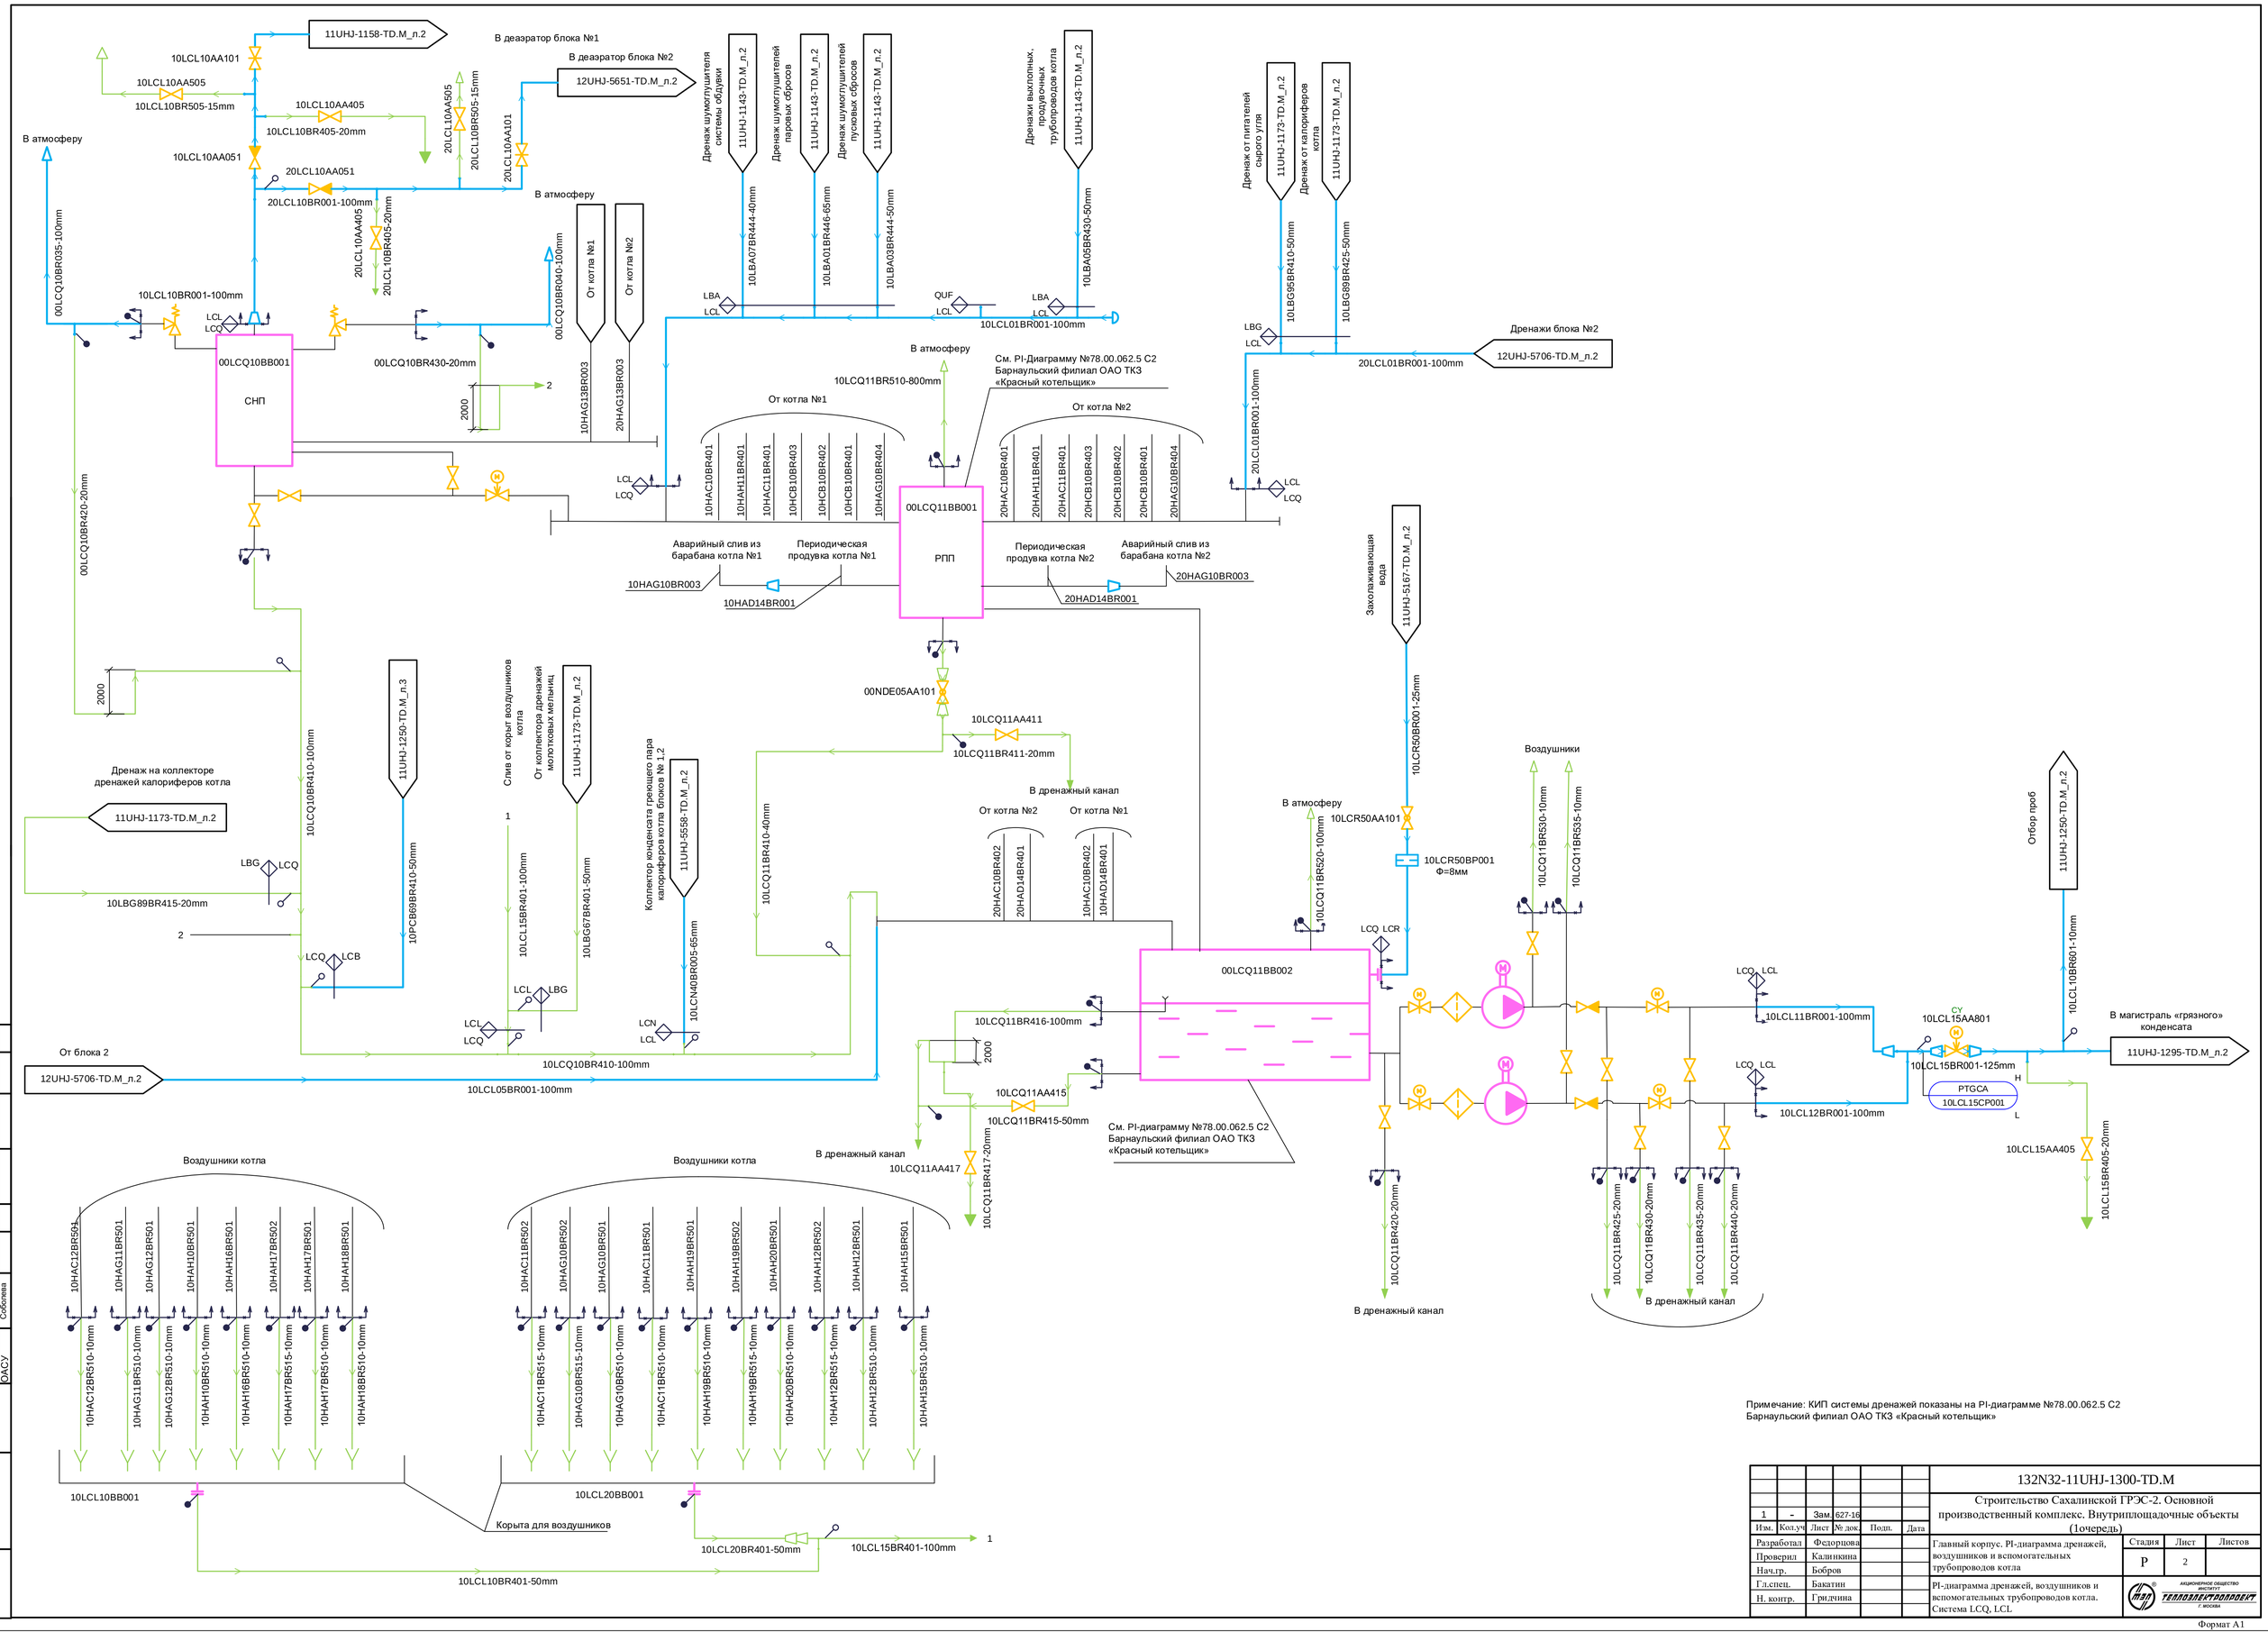

Примечание: КИП системы дренажей показаны на PI-диаграмме №78.00.062.5 С2
Барнаульский филиал ОАО ТК3 «Красный котельщик»

						132N32-11UHJ-1300-TD.M			
						Строительство Сахалинской ГРЭС-2. Основной производственный комплекс. Внутриплощадочные объекты (1очередь)			
1	-	Зам.	627-16						
Изм.	Кол.уч	Лист	№ док.	Подп.	Дата				
Разработал		Федорцова				Главный корпус. PI-диаграмма дренажей, воздушников и вспомогательных трубопроводов котла	Стадия	Лист	Листов
Проверил		Калинкина					Р	2	
Нач.гр.		Бобров							
Гл.спец.		Бакатин				PI-диаграмма дренажей, воздушников и вспомогательных трубопроводов котла. Система LCQ, LCL	АКЦИОНЕРНОЕ ОБЩЕСТВО ИНСТИТУТ ТЕПЛОЭЛЕКТРОПРОЕКТ Г. МОСКВА		
Н. контр.		Гридчина							

Согласовано

ОАСУ	Соболева

Взам. инв. №

Подпись и дата

Инв. № подл.

Формат А1