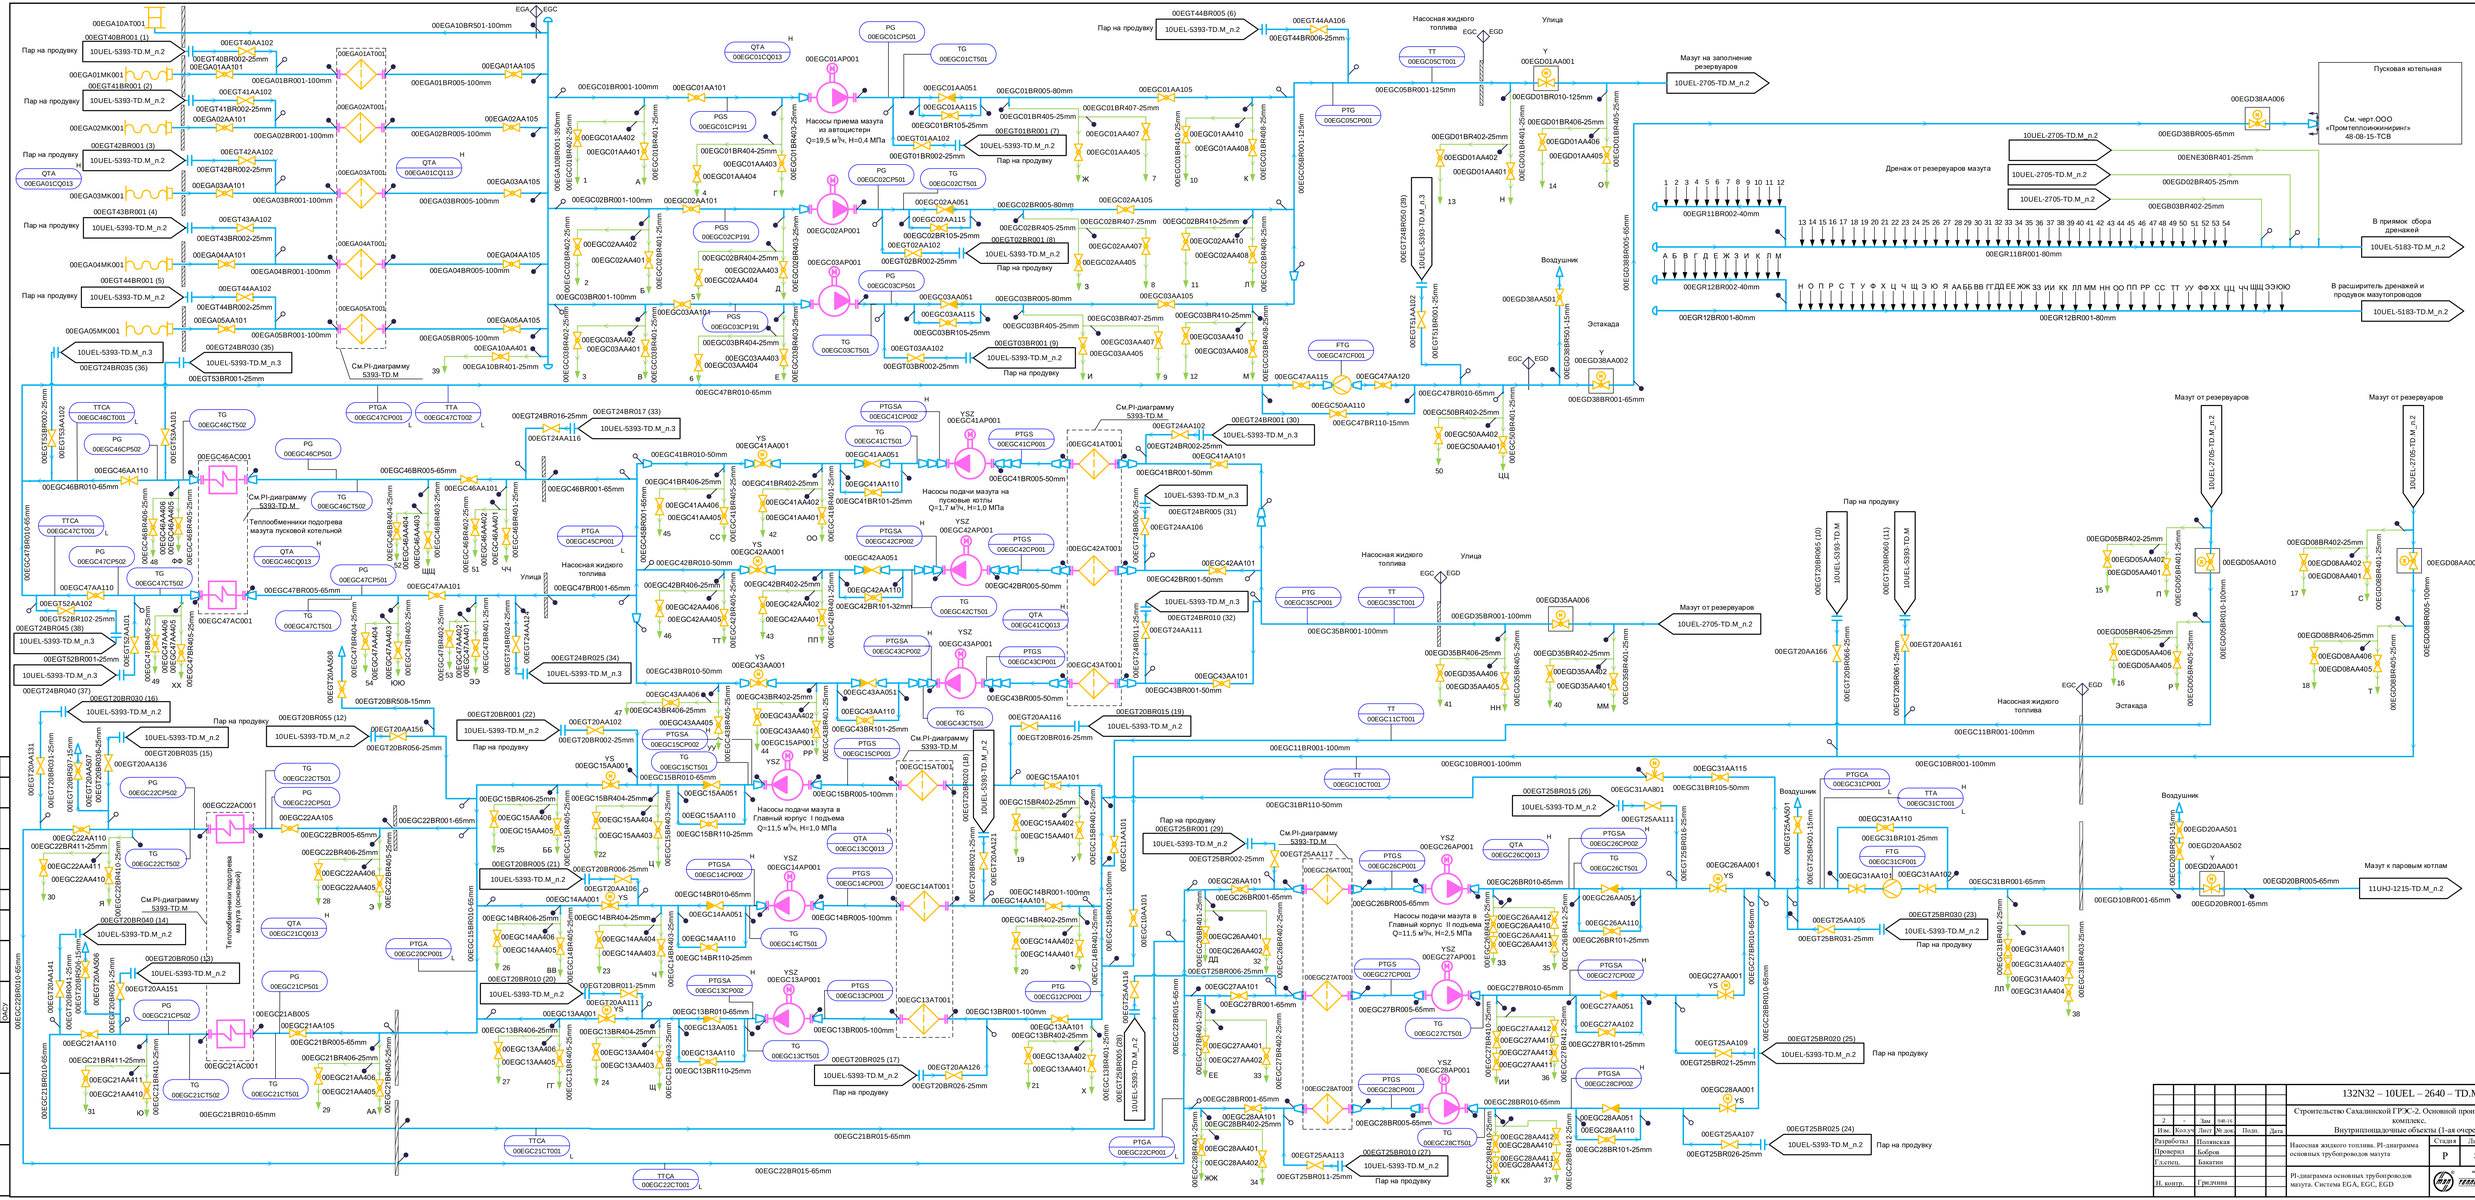

							132N32 – 10UEL – 2640 – TD.M
2	-	Зам	348-16				Строительство Сахалинской ГРЭС-2. Основной производственный комплекс.
Изм.	Кол.уч	Лист	№ док.	Подп.	Дата		Внутриплощадочные объекты (1-ая очередь)
Разработал		Полянская					Насосная жидкого топлива. PI-диаграмма основных трубопроводов мазута
Проверил		Бобров					Стадия: Р; Лист: 2; Листов:
Гл.спец.		Бакатин					
Н. контр.		Гредина					PI-диаграмма основных трубопроводов мазута. Системы EGA, EGC, EGD

Согласовано

Взам. инв. №

Подпись и дата

Инв. № подл.

Формат А2х3