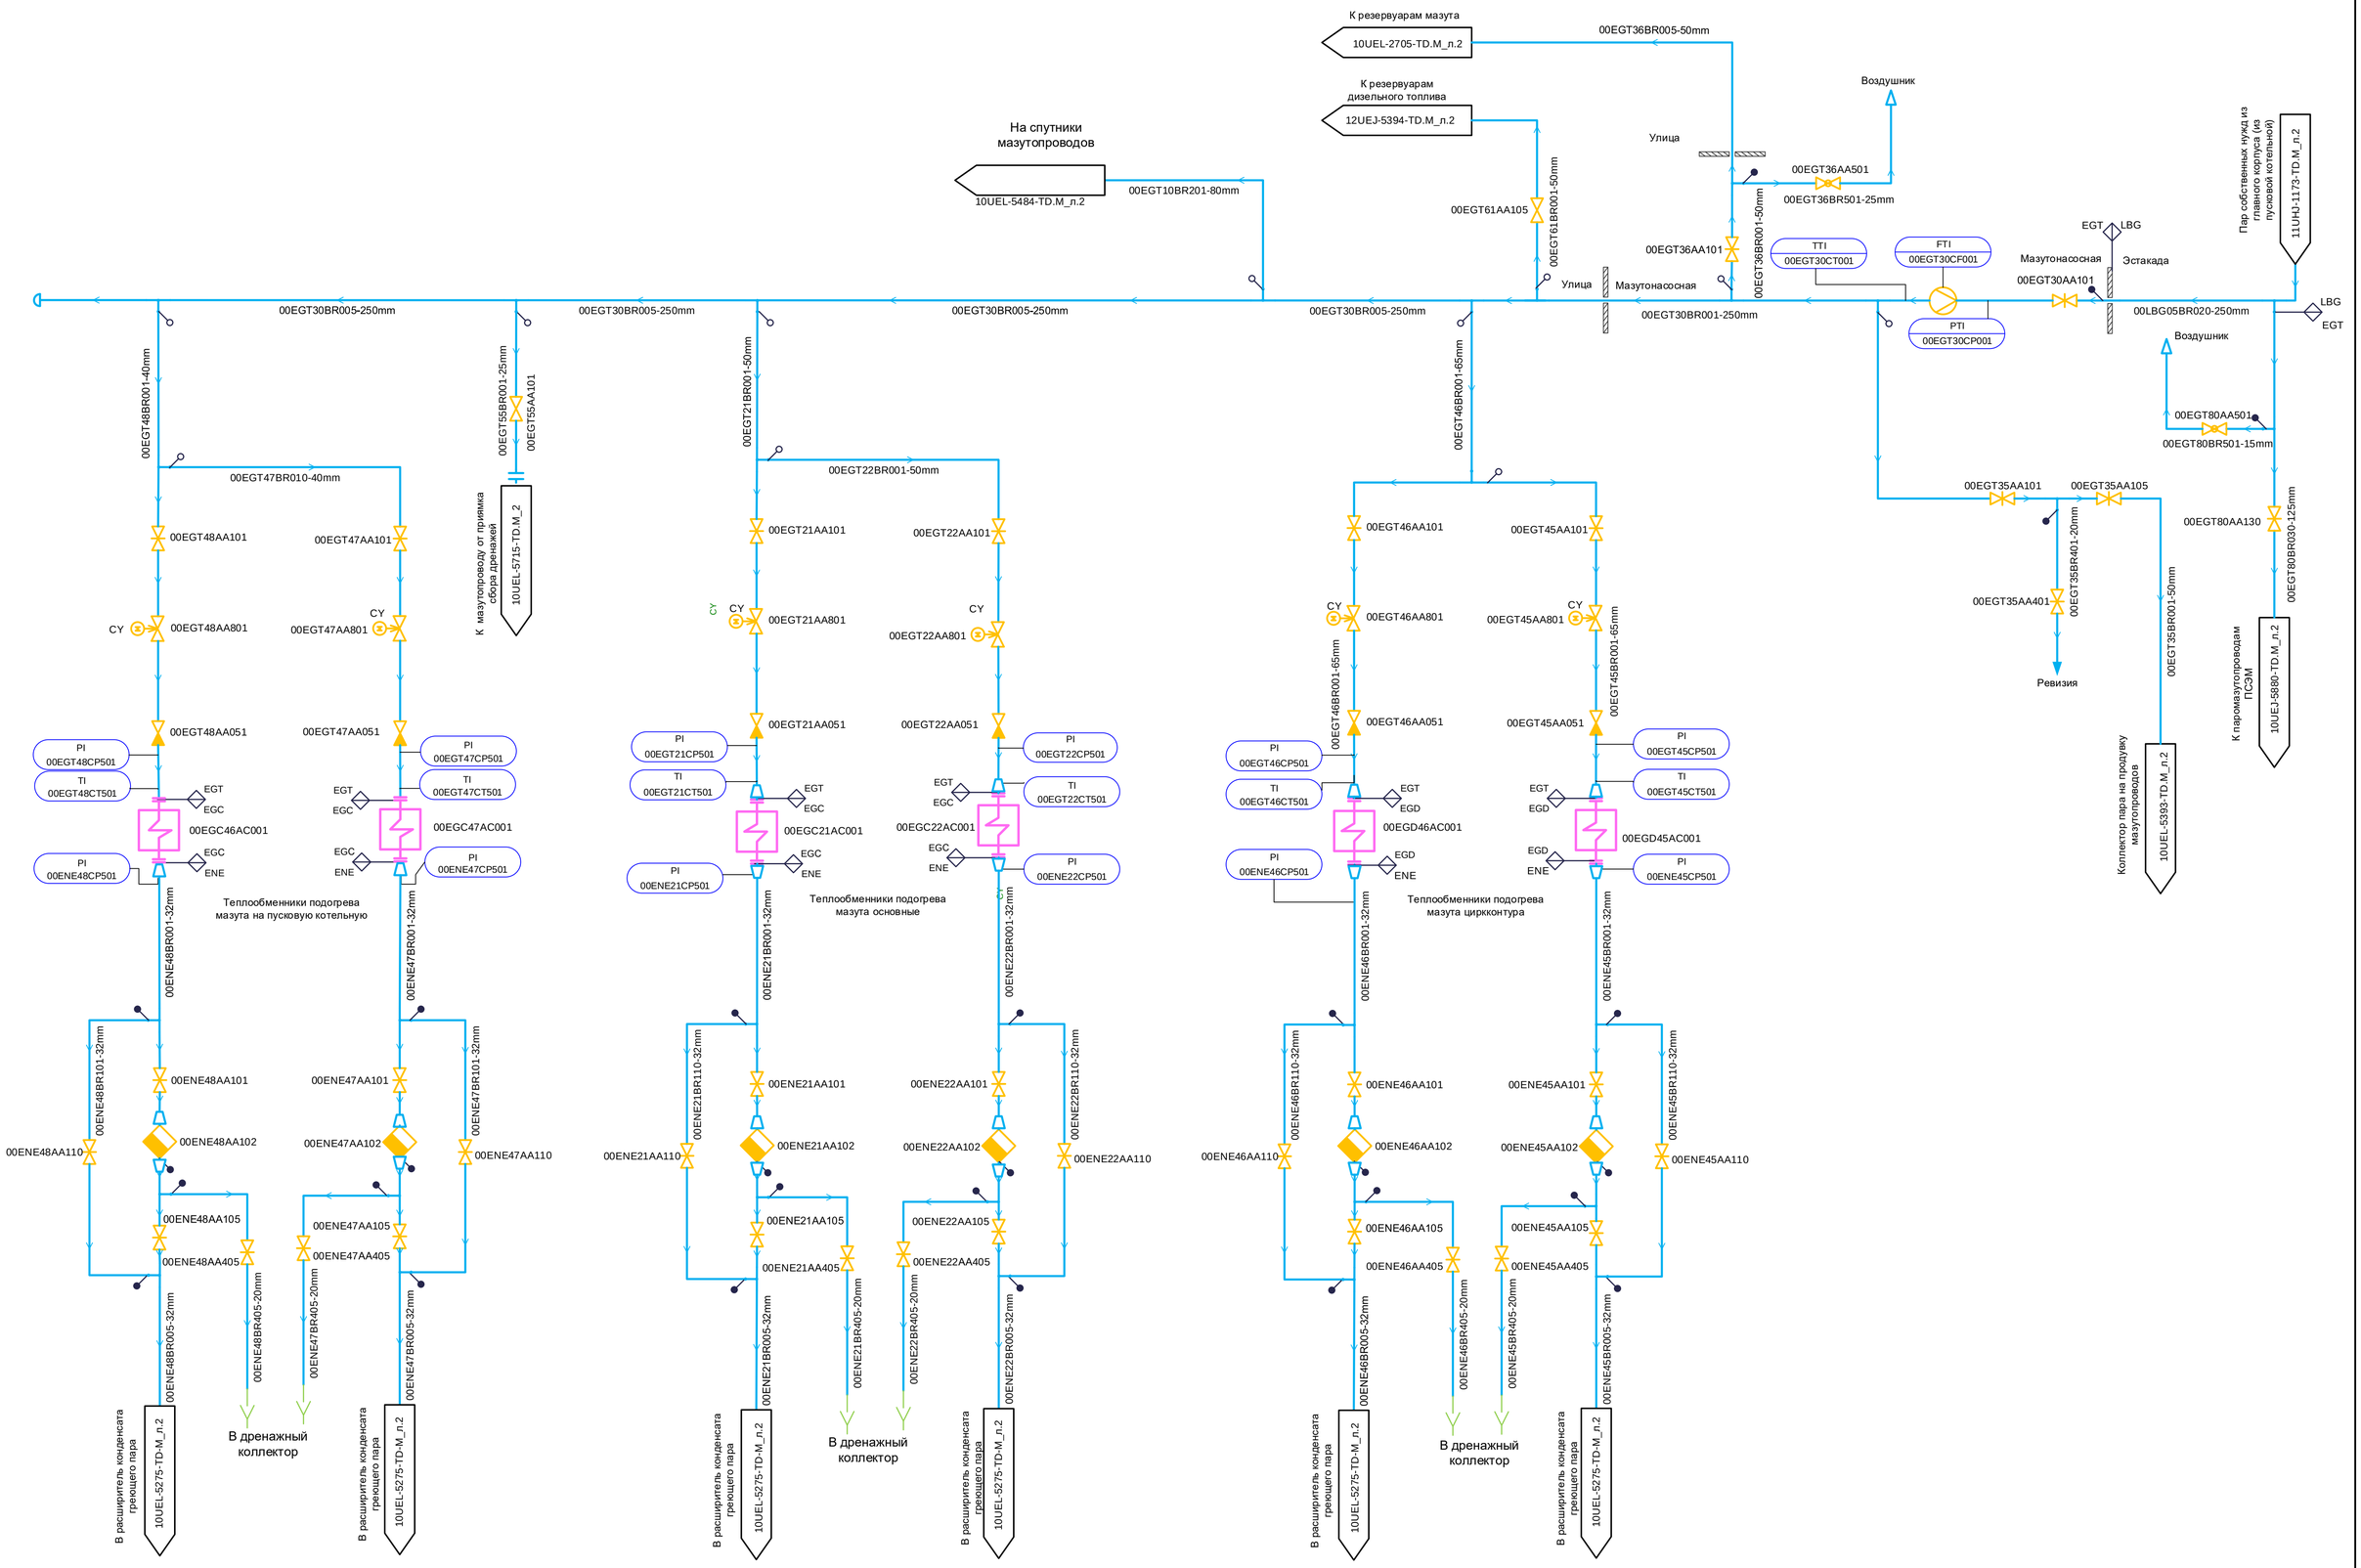

1	-	Зам	74-17			
Изм.	Кол.уч	Лист	№ док.	Подп.	Дата	

132N32 – 10UEL – 2649 – TD.M

Строительство Сахалинской ГРЭС-2. Основной производственный комплекс.
Внутриплощадочные объекты (1-ая очередь)

Разработал	Полянская	
Проверил	Бобров	
Гл.спец.	Егоров	
Н. контр.	Грядчина	

Насосная жидкого топлива.
PI-диаграмма паропроводов мазутного хозяйства

PI-диаграмма паропроводов мазутного хозяйства. Система EGT, ENE.

Стадия	Лист	Листов
Р	2	

АКЦИОНЕРНОЕ ОБЩЕСТВО ИНСТИТУТ ТЕПЛОЭЛЕКТРОПРОЕКТ г. МОСКВА

Согласовано

ОАСУ

Взам. инв. №

Подпись и дата

Инв. № подл.

Формат А1