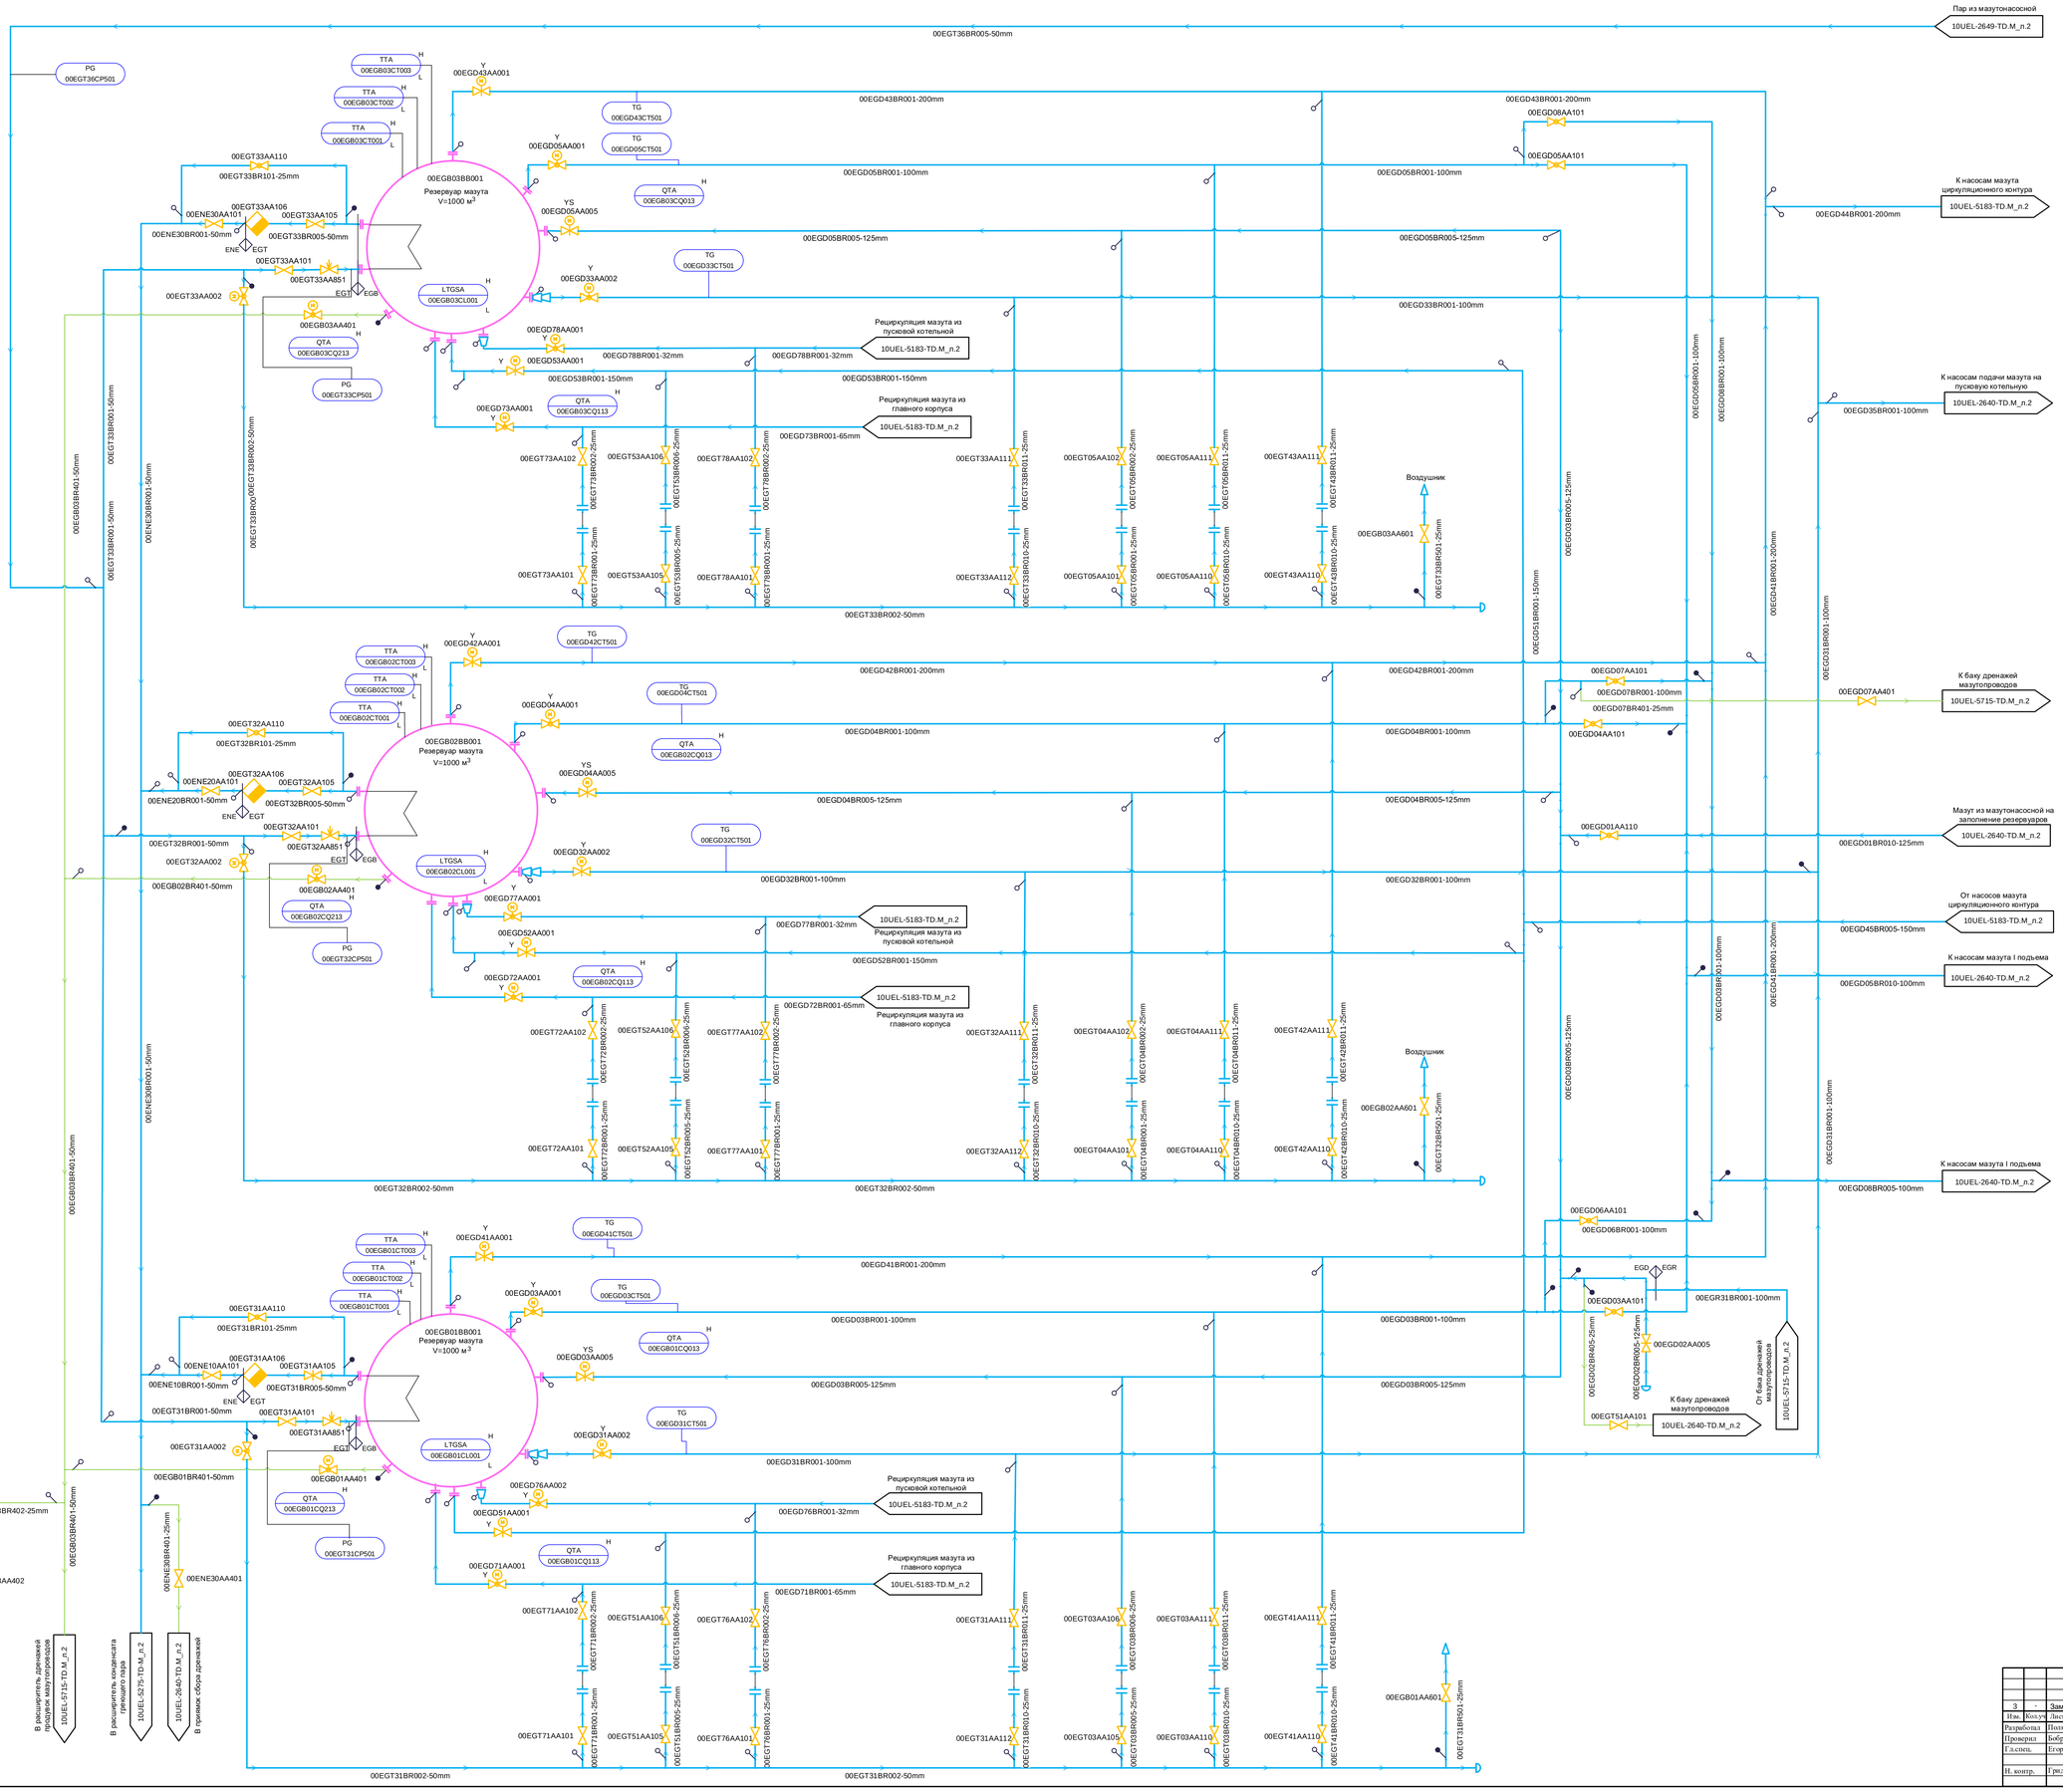


| | | | | | | | |
|---|---|---|---|---|---|---|---|
| | | | | | | 132N32 – 10UEJ – 2705 – TD.M | |
| 3 | - | Зам | 16-17 | | | Строительство Сахалинской ГРЭС-2. Основной производственный комплекс. Внутриплощадочные объекты (1-ая очередь) | |
| Изм. | Кол.уч. | Лист | № док. | Подп. | Дата | | |
| Разработал | | Полянская | | | | Склад мазута. PI-диаграмма трубопроводов обвязки резервуаров мазута. | Стадия: Р; Лист: 2; Листов: |
| Проверил | | Бобров | | | | | |
| Гл.спец. | | Егоров | | | | | |
| Н. контр. | | Грядунова | | | | PI-диаграмма трубопроводов обвязки резервуаров мазута. | АКЦИОНЕРНОЕ ОБЩЕСТВО ИНСТИТУТ ТЕПЛОЭЛЕКТРОПРОЕКТ ГРУППА |

Согласовано

ОАСУ

Взам. инв. №

Подпись и дата

Инв. № подл.

Формат А0