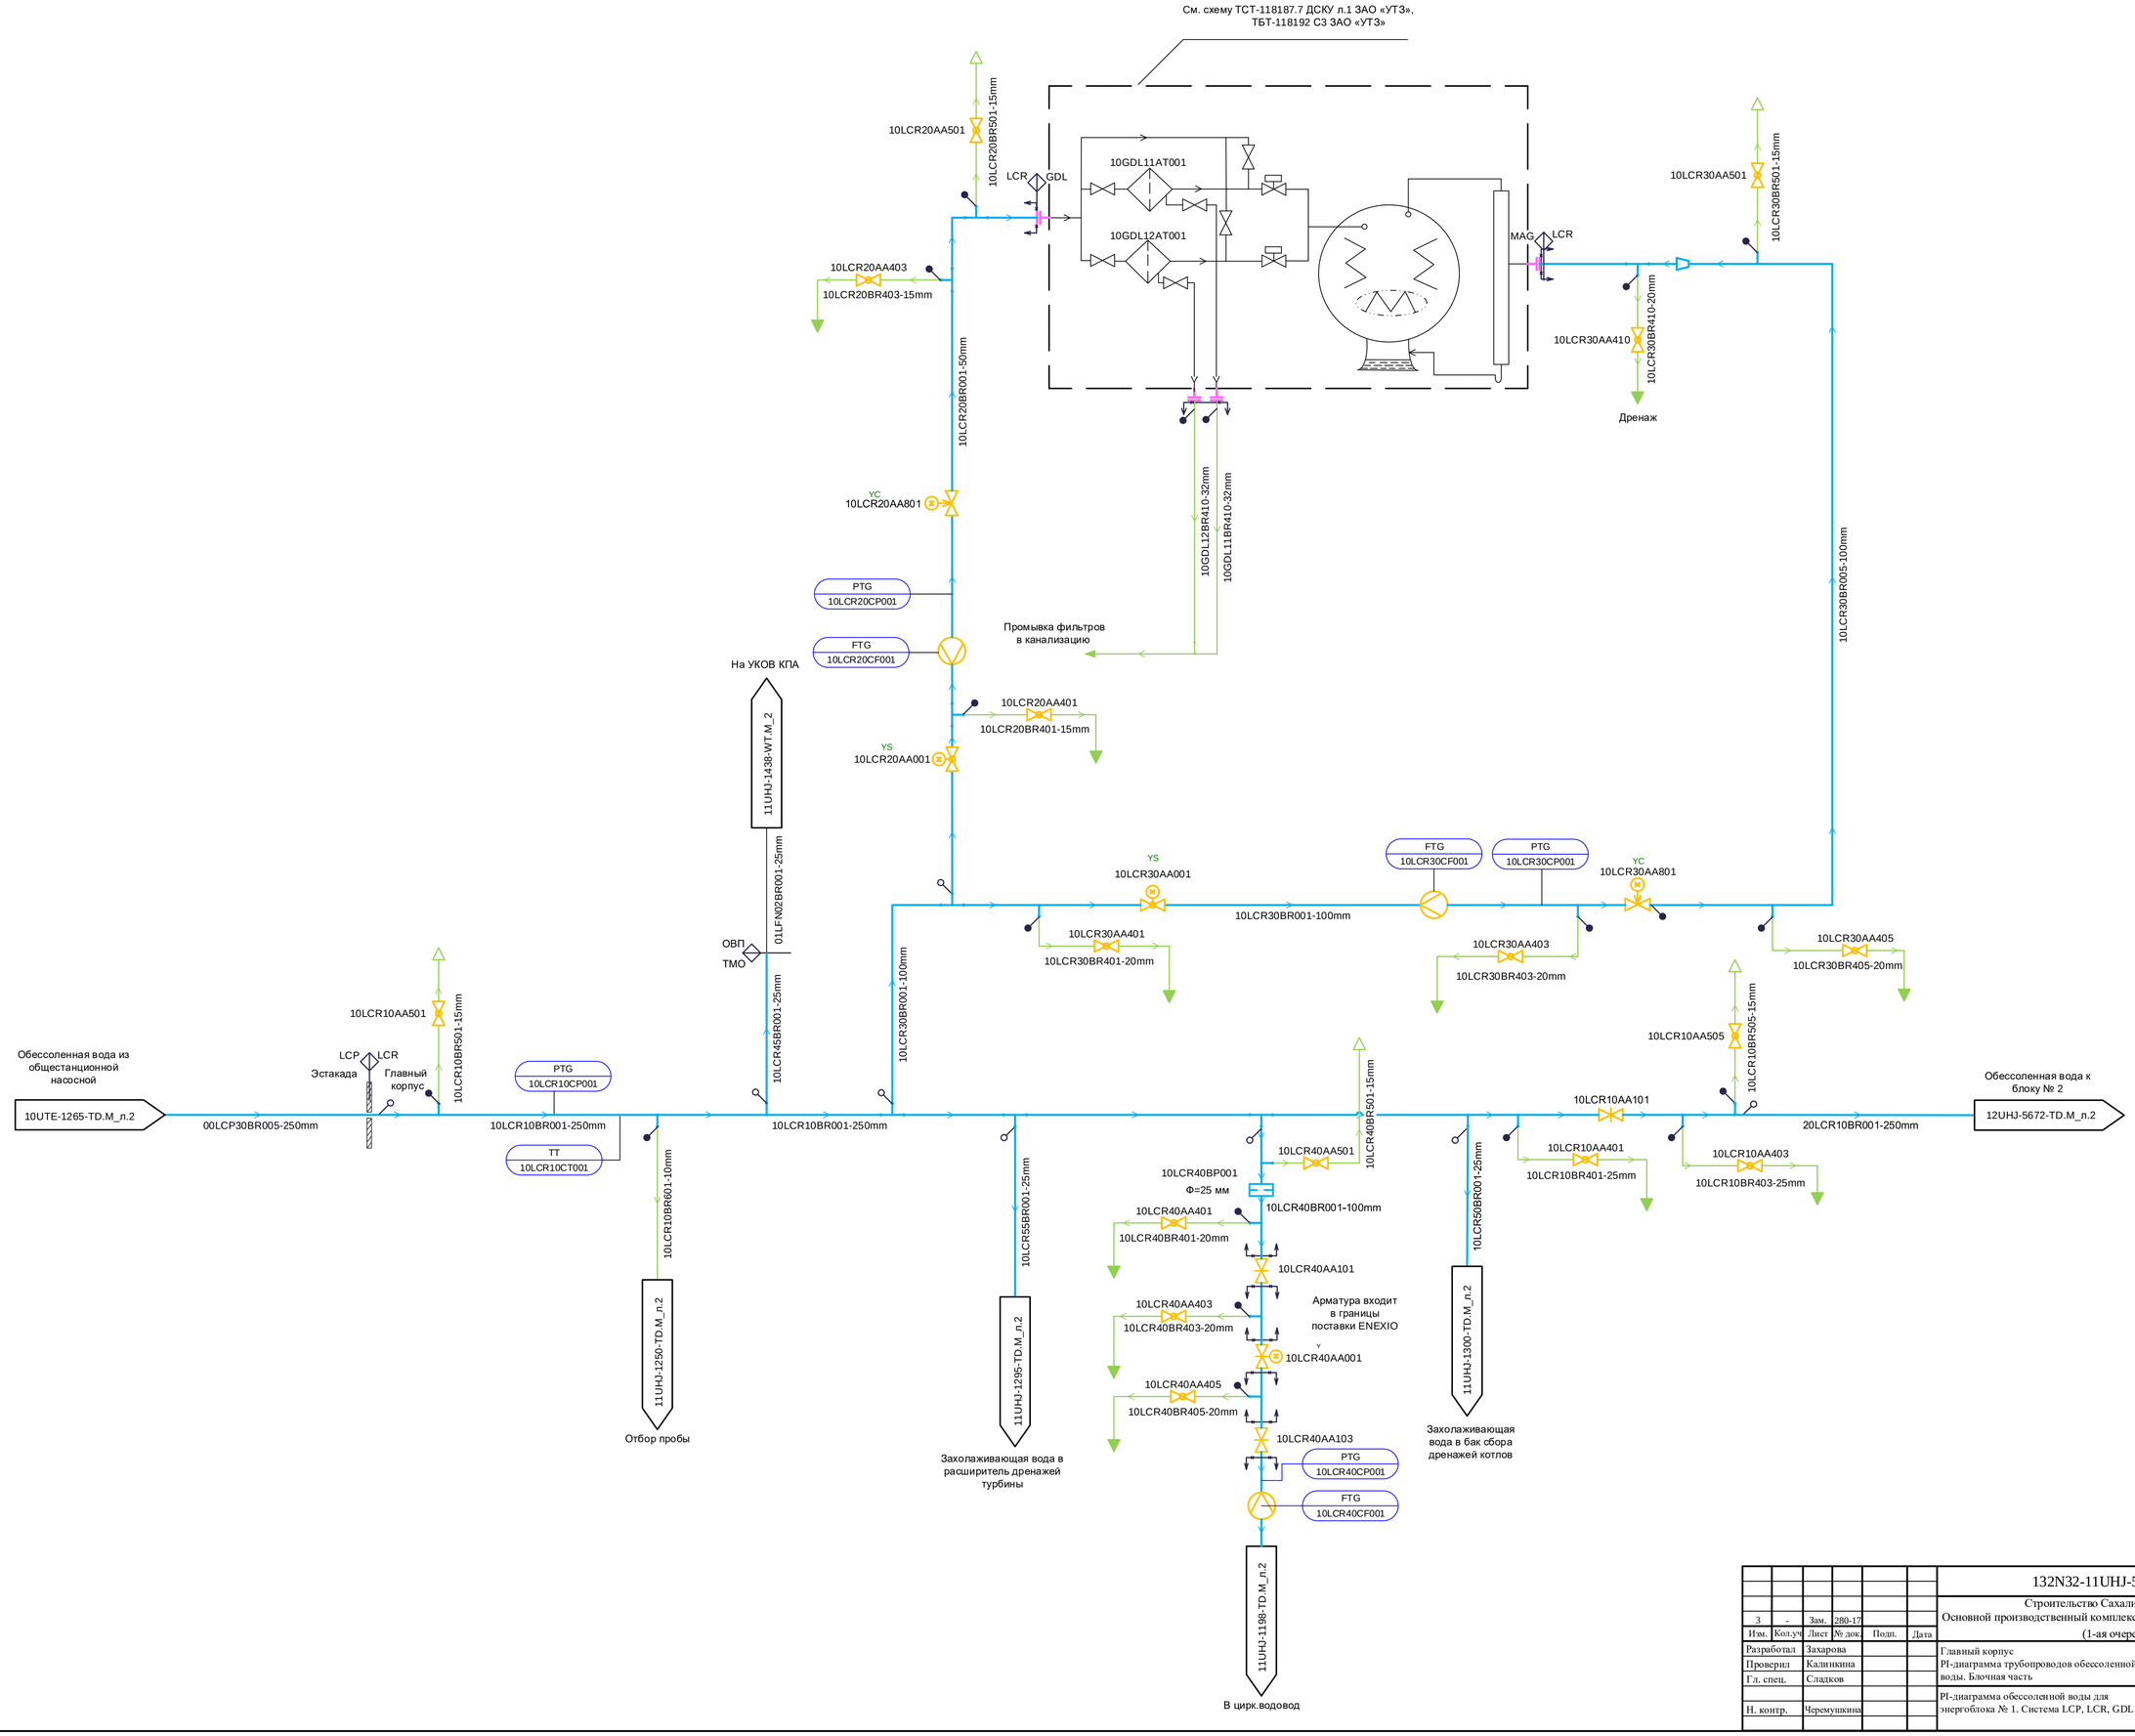

3	-	Зам.	280-17			
Изм.	Кол.уч	Лист	№ док.	Подп.	Дата	
Разработал		Захарова				
Проверил		Калинкина				
Гл. спец.		Сладков				
Н. контр.		Черемушкина				

132N32-11UHJ-5167-TD.M

Строительство Сахалинской ГРЭС-2.
Основной производственный комплекс. Внутриплощадочные объекты
(1-ая очередь)

Главный корпус
PI-диаграмма трубопроводов обессоленной воды. Блочная часть

PI-диаграмма обессоленной воды для энергоблока № 1. Система LCP, LCR, GDL.

Стадия	Лист	Листов
Р	2	

АКЦИОНЕРНОЕ ОБЩЕСТВО «ИНСТИТУТ ТЕПЛОЭЛЕКТРОПРОЕКТ» Г. МОСКВА

Согласовано
ОАСУ
Соболева

Взам. инв. №
Подпись и дата
Инв. № подл.

Формат А1