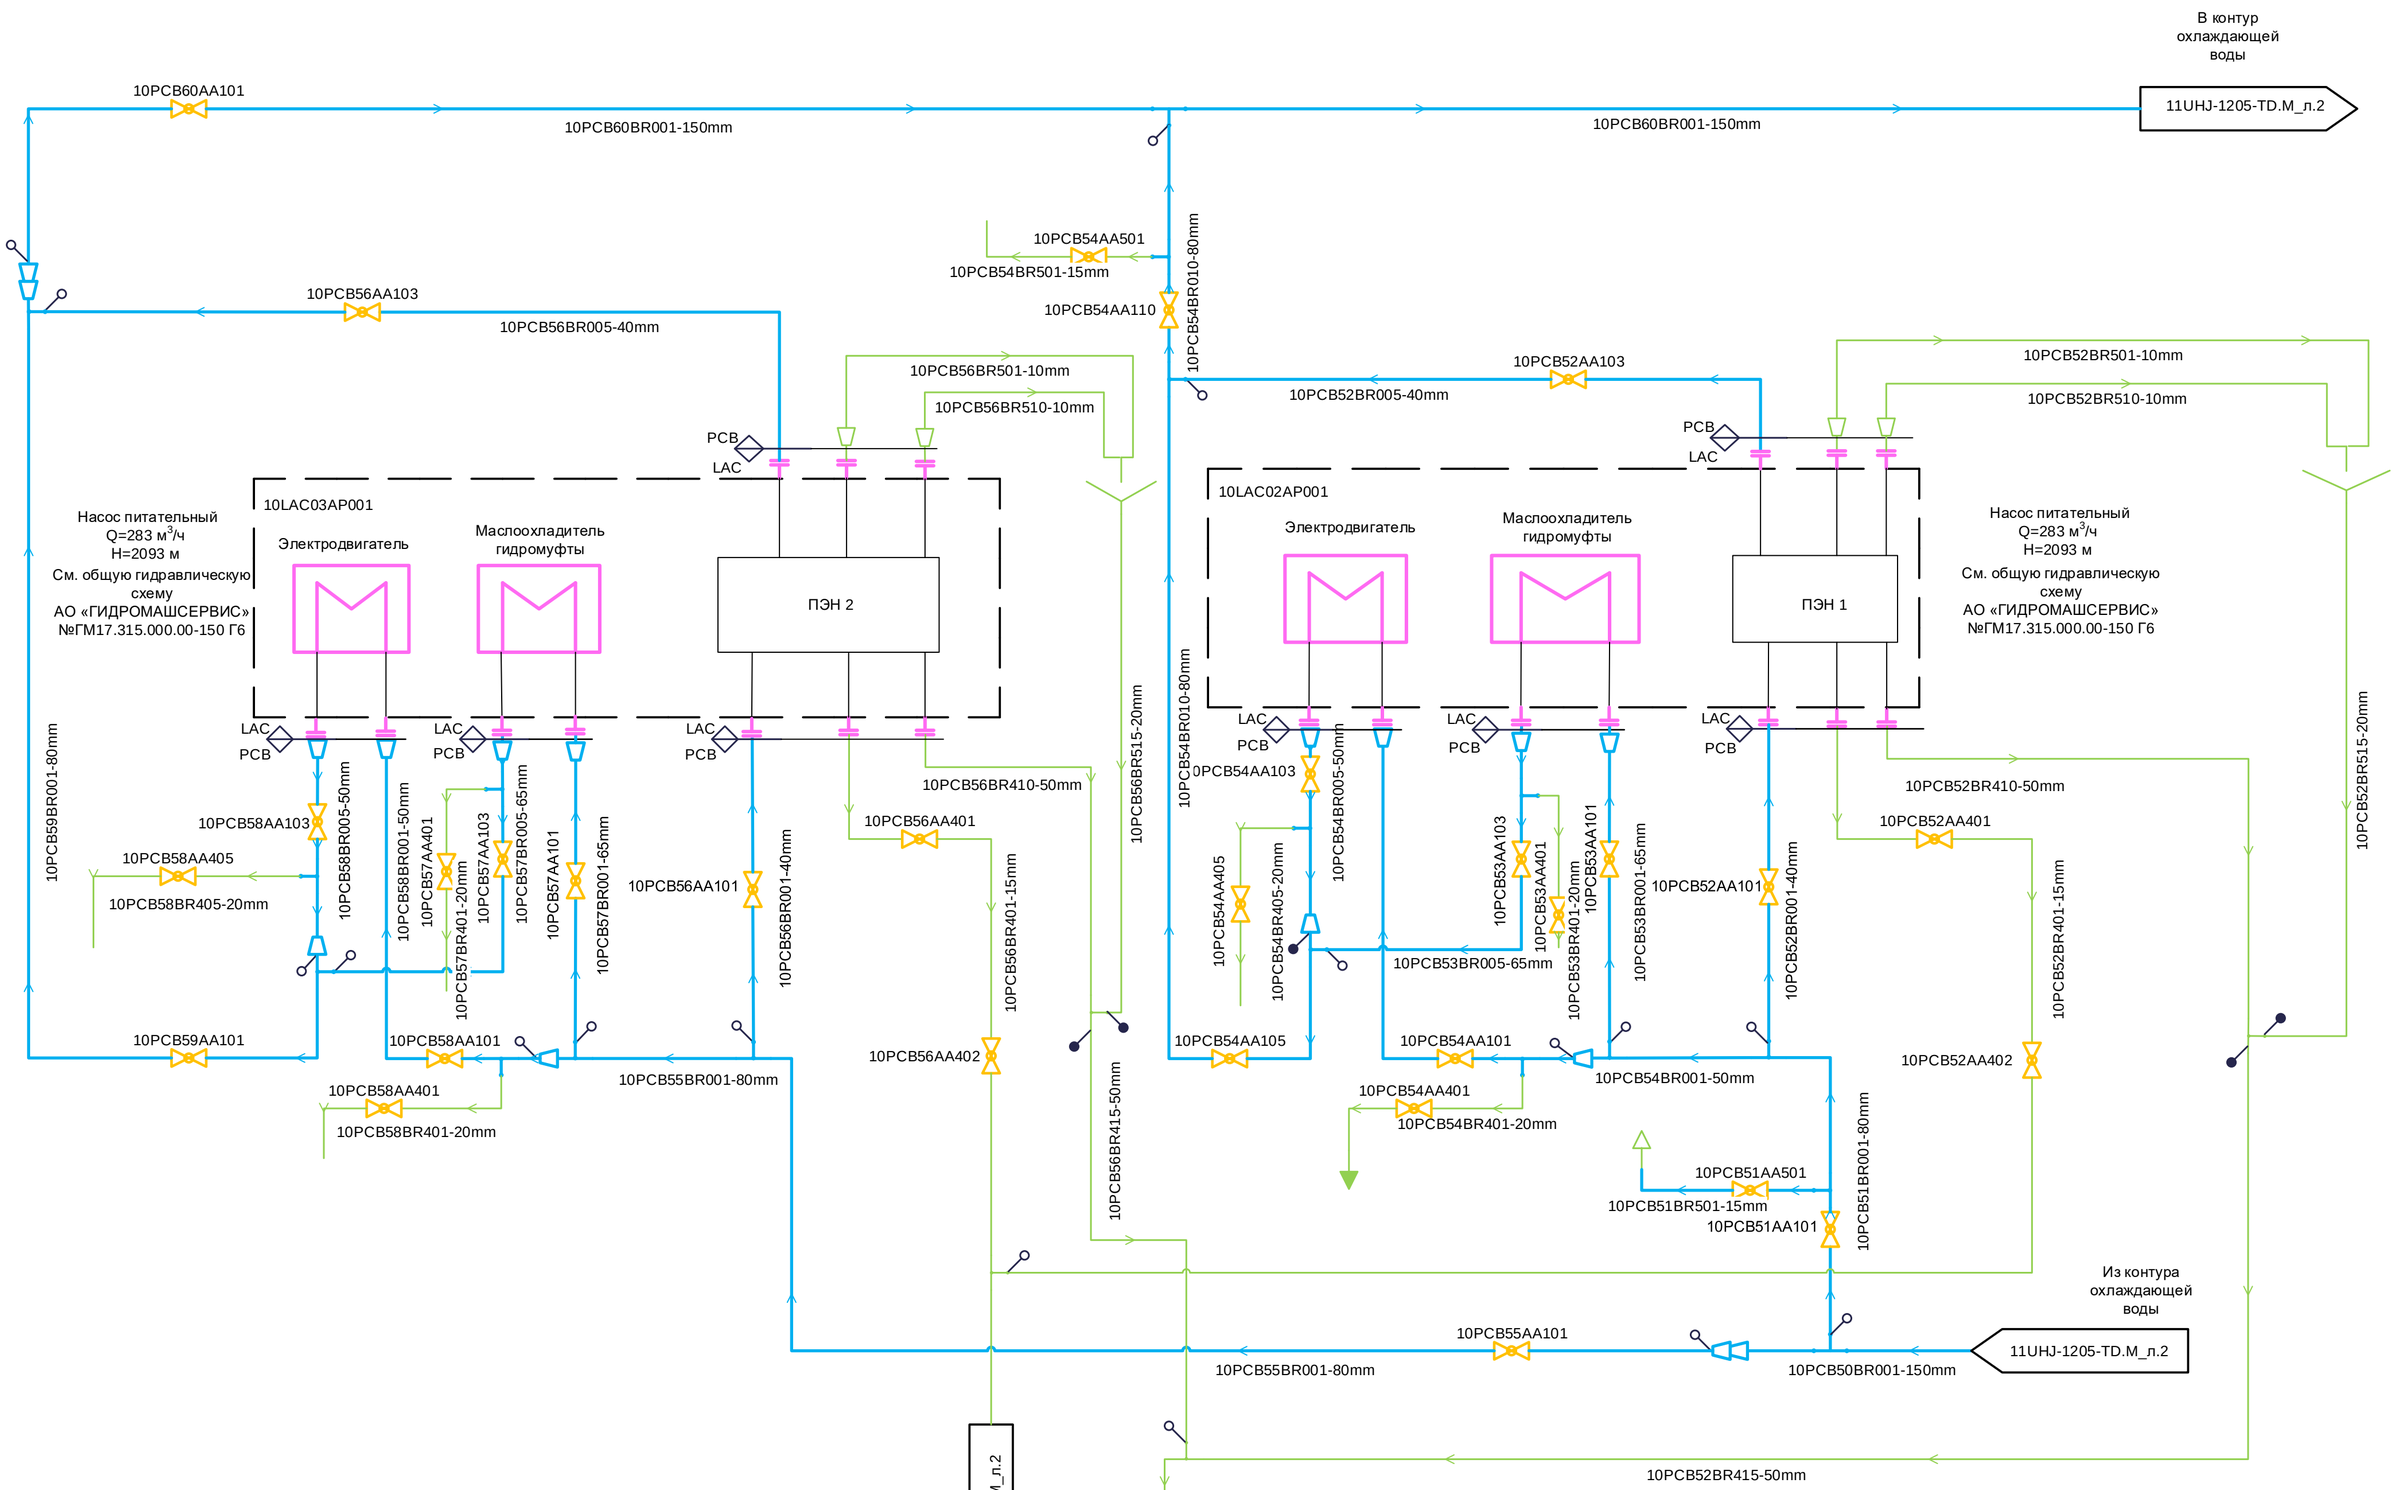

Согласовано

ОАСУ Владиславлев

Взам. инв. №

Подпись и дата

Инв. № подл.

1	-	Зам.	372-16			
Изм.	Кол.уч	Лист	№ док.	Подп.	Дата	
Разработал		Захарова				
Проверил		Калинкина				
Глав. спец.		Бакатин				
Н. контр.		Черемушкина				

132N32-11UHJ-5172-TD.M

Строительство Сахалинской ГРЭС-2.
Основной производственный комплекс. Внутриплощадочные объекты
(1-ая очередь)

Главный корпус.
PI-диаграмма вспомогательных трубопроводов ПЭН

Стадия	Лист	Листов
Р	2	

PI-диаграмма вспомогательных трубопроводов ПЭН. Система PCB.

АКЦИОНЕРНОЕ ОБЩЕСТВО ИНСТИТУТ ТЕПЛОЭЛЕКТРОПРОЕКТ Г. МОСКВА

Формат А2