Примечания:

1. Побудительные сопла под котлом устанавливают на расстоянии 1,0-1,5 м до места сброса шлака в канал

2. Побудительные сопла по длине канала устанавливаются на расстоянии 8-10 м. друг от друга

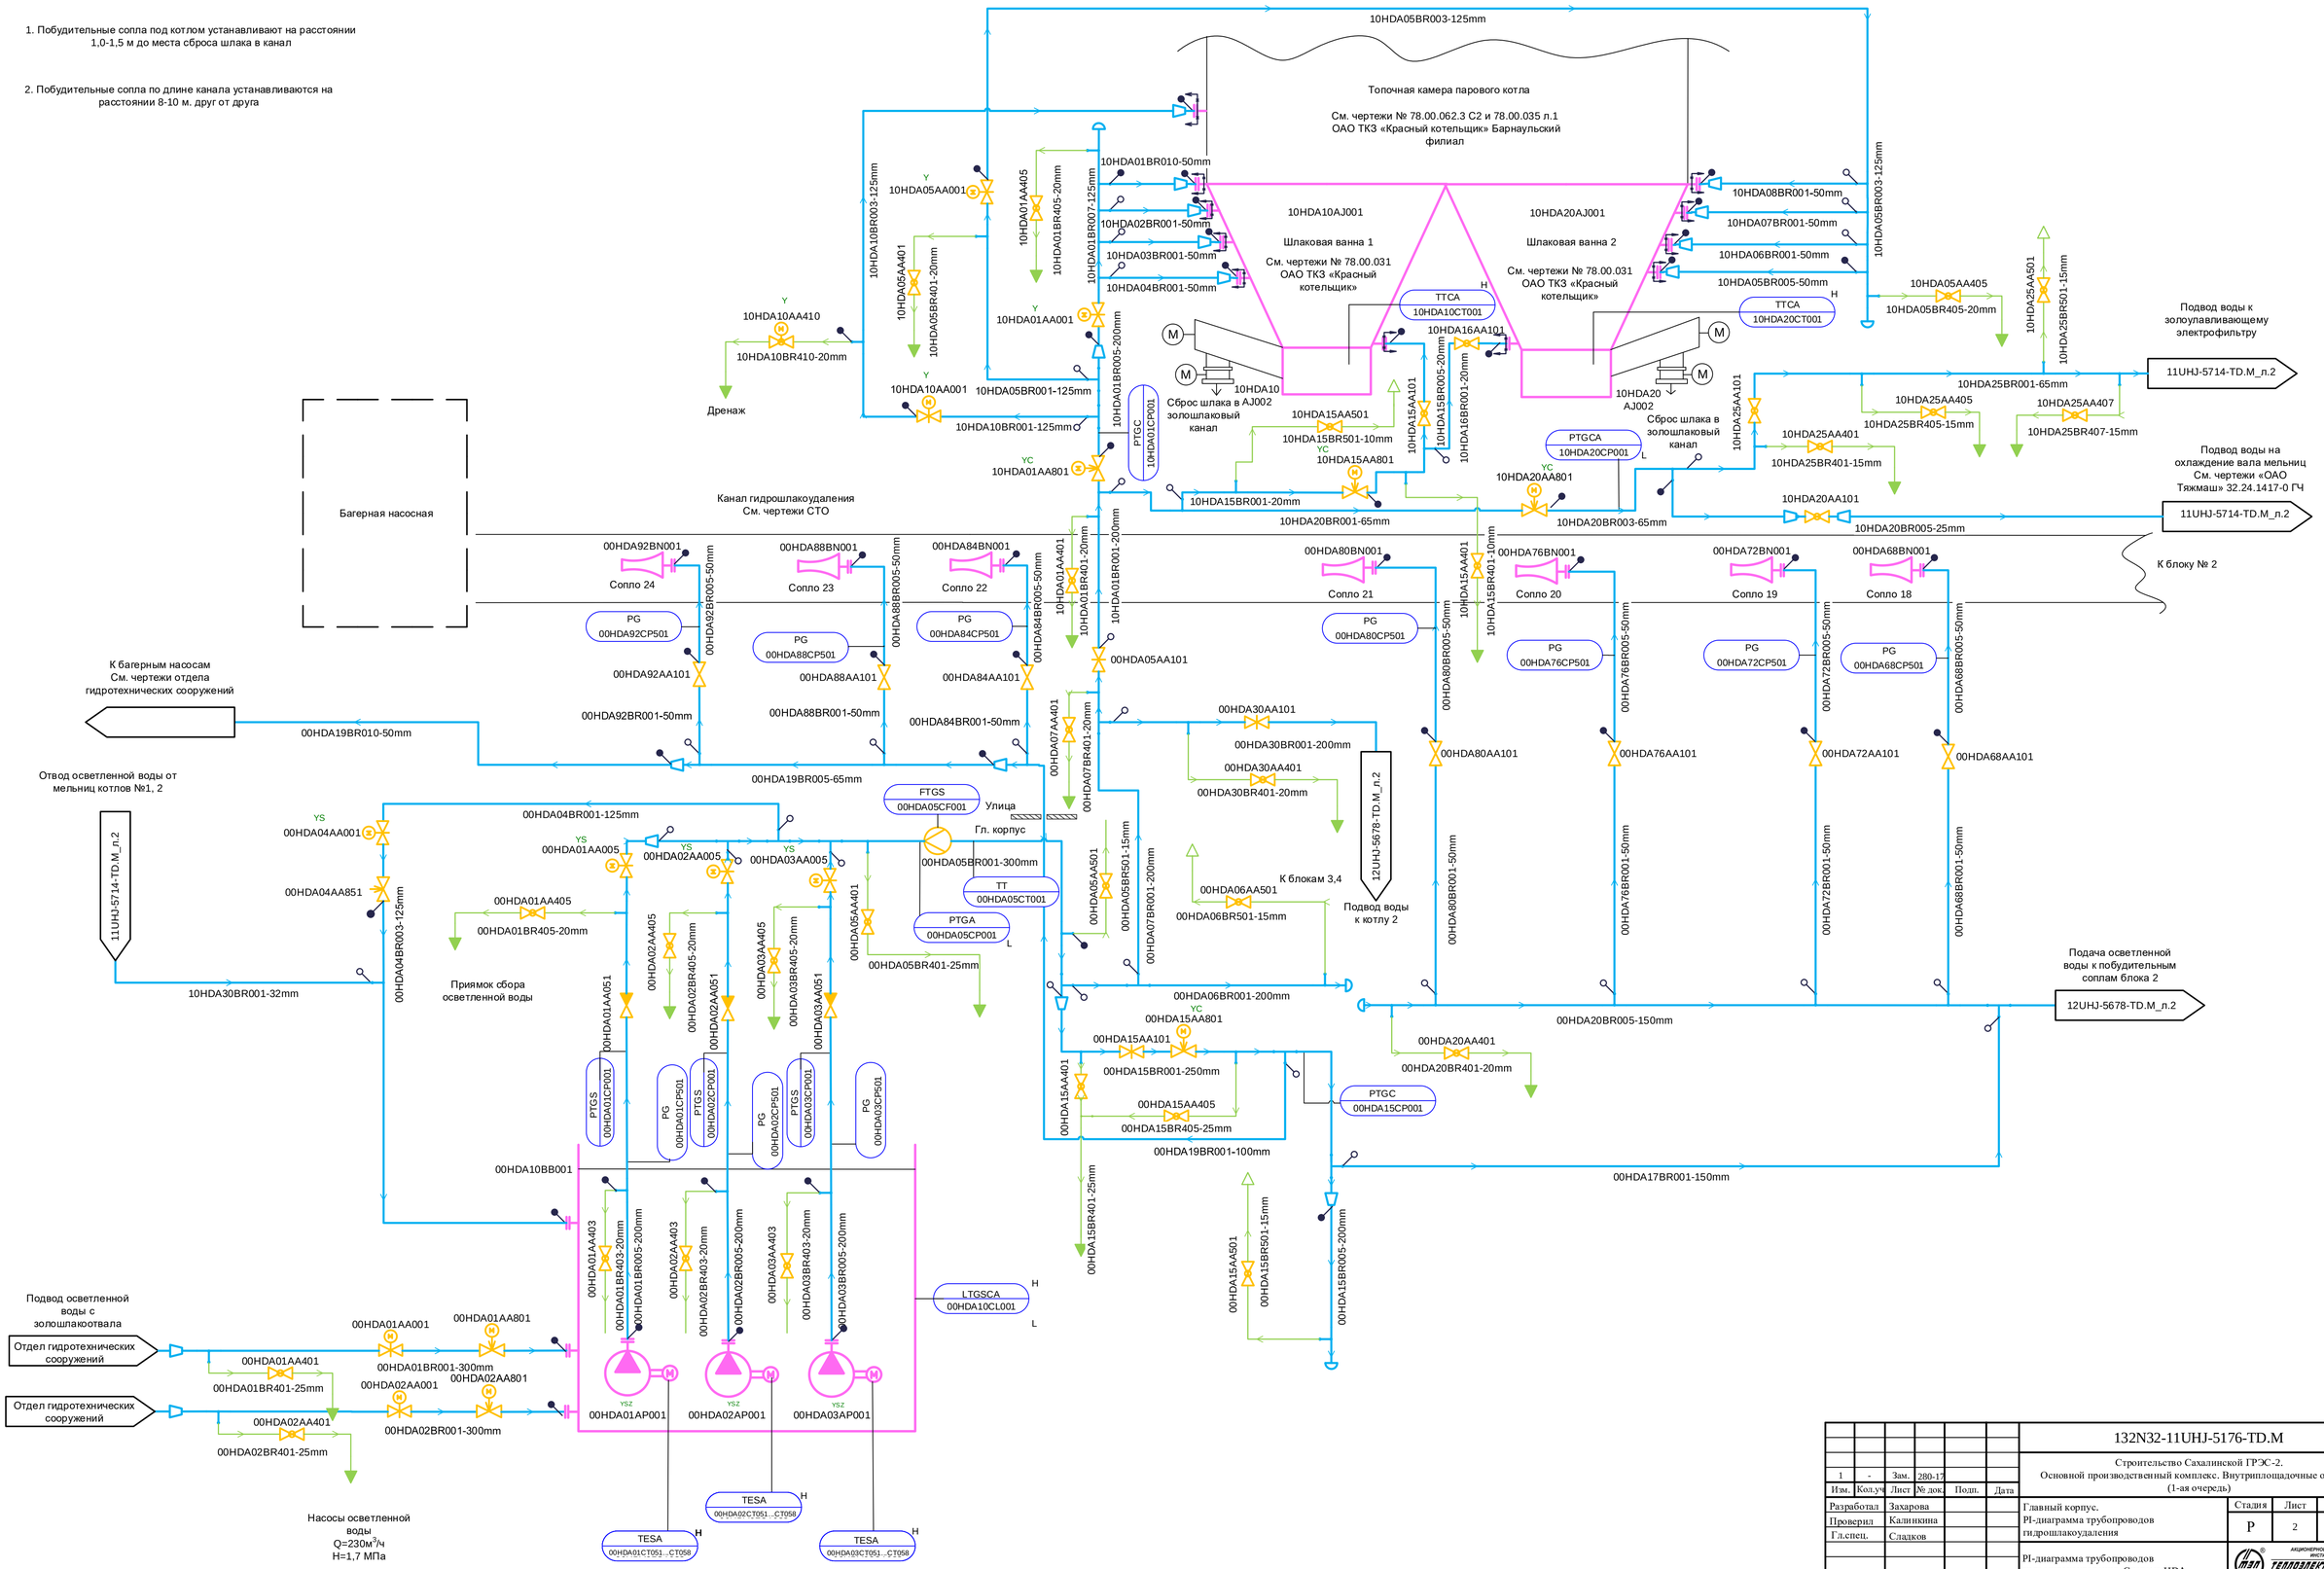

1	-	Зам.	280-17			132N32-11UHJ-5176-TD.M	
Изм.	Кол.уч.	Лист	№ док.	Подп.	Дата	Строительство Сахалинской ГРЭС-2. Основной производственный комплекс. Внутриплощадочные объекты (1-ая очередь)	
Разработал		Захарова				Главный корпус. PI-диаграмма трубопроводов гидрошлакоудаления	Стадия: Р; Лист: 2; Листов:
Проверил		Калинкина					
Гл.спец.		Сладков					
						PI-диаграмма трубопроводов гидрошлакоудаления. Система HDA.	АКЦИОНЕРНОЕ ОБЩЕСТВО ИНСТИТУТ ТЕПЛОЭЛЕКТРОПРОЕКТ г. МОСКВА
Н. контр.		Черемушкина					

Согласовано

ОАСУ

Взам. инв. №

Подпись и дата

Инв. № подл.

Формат А1