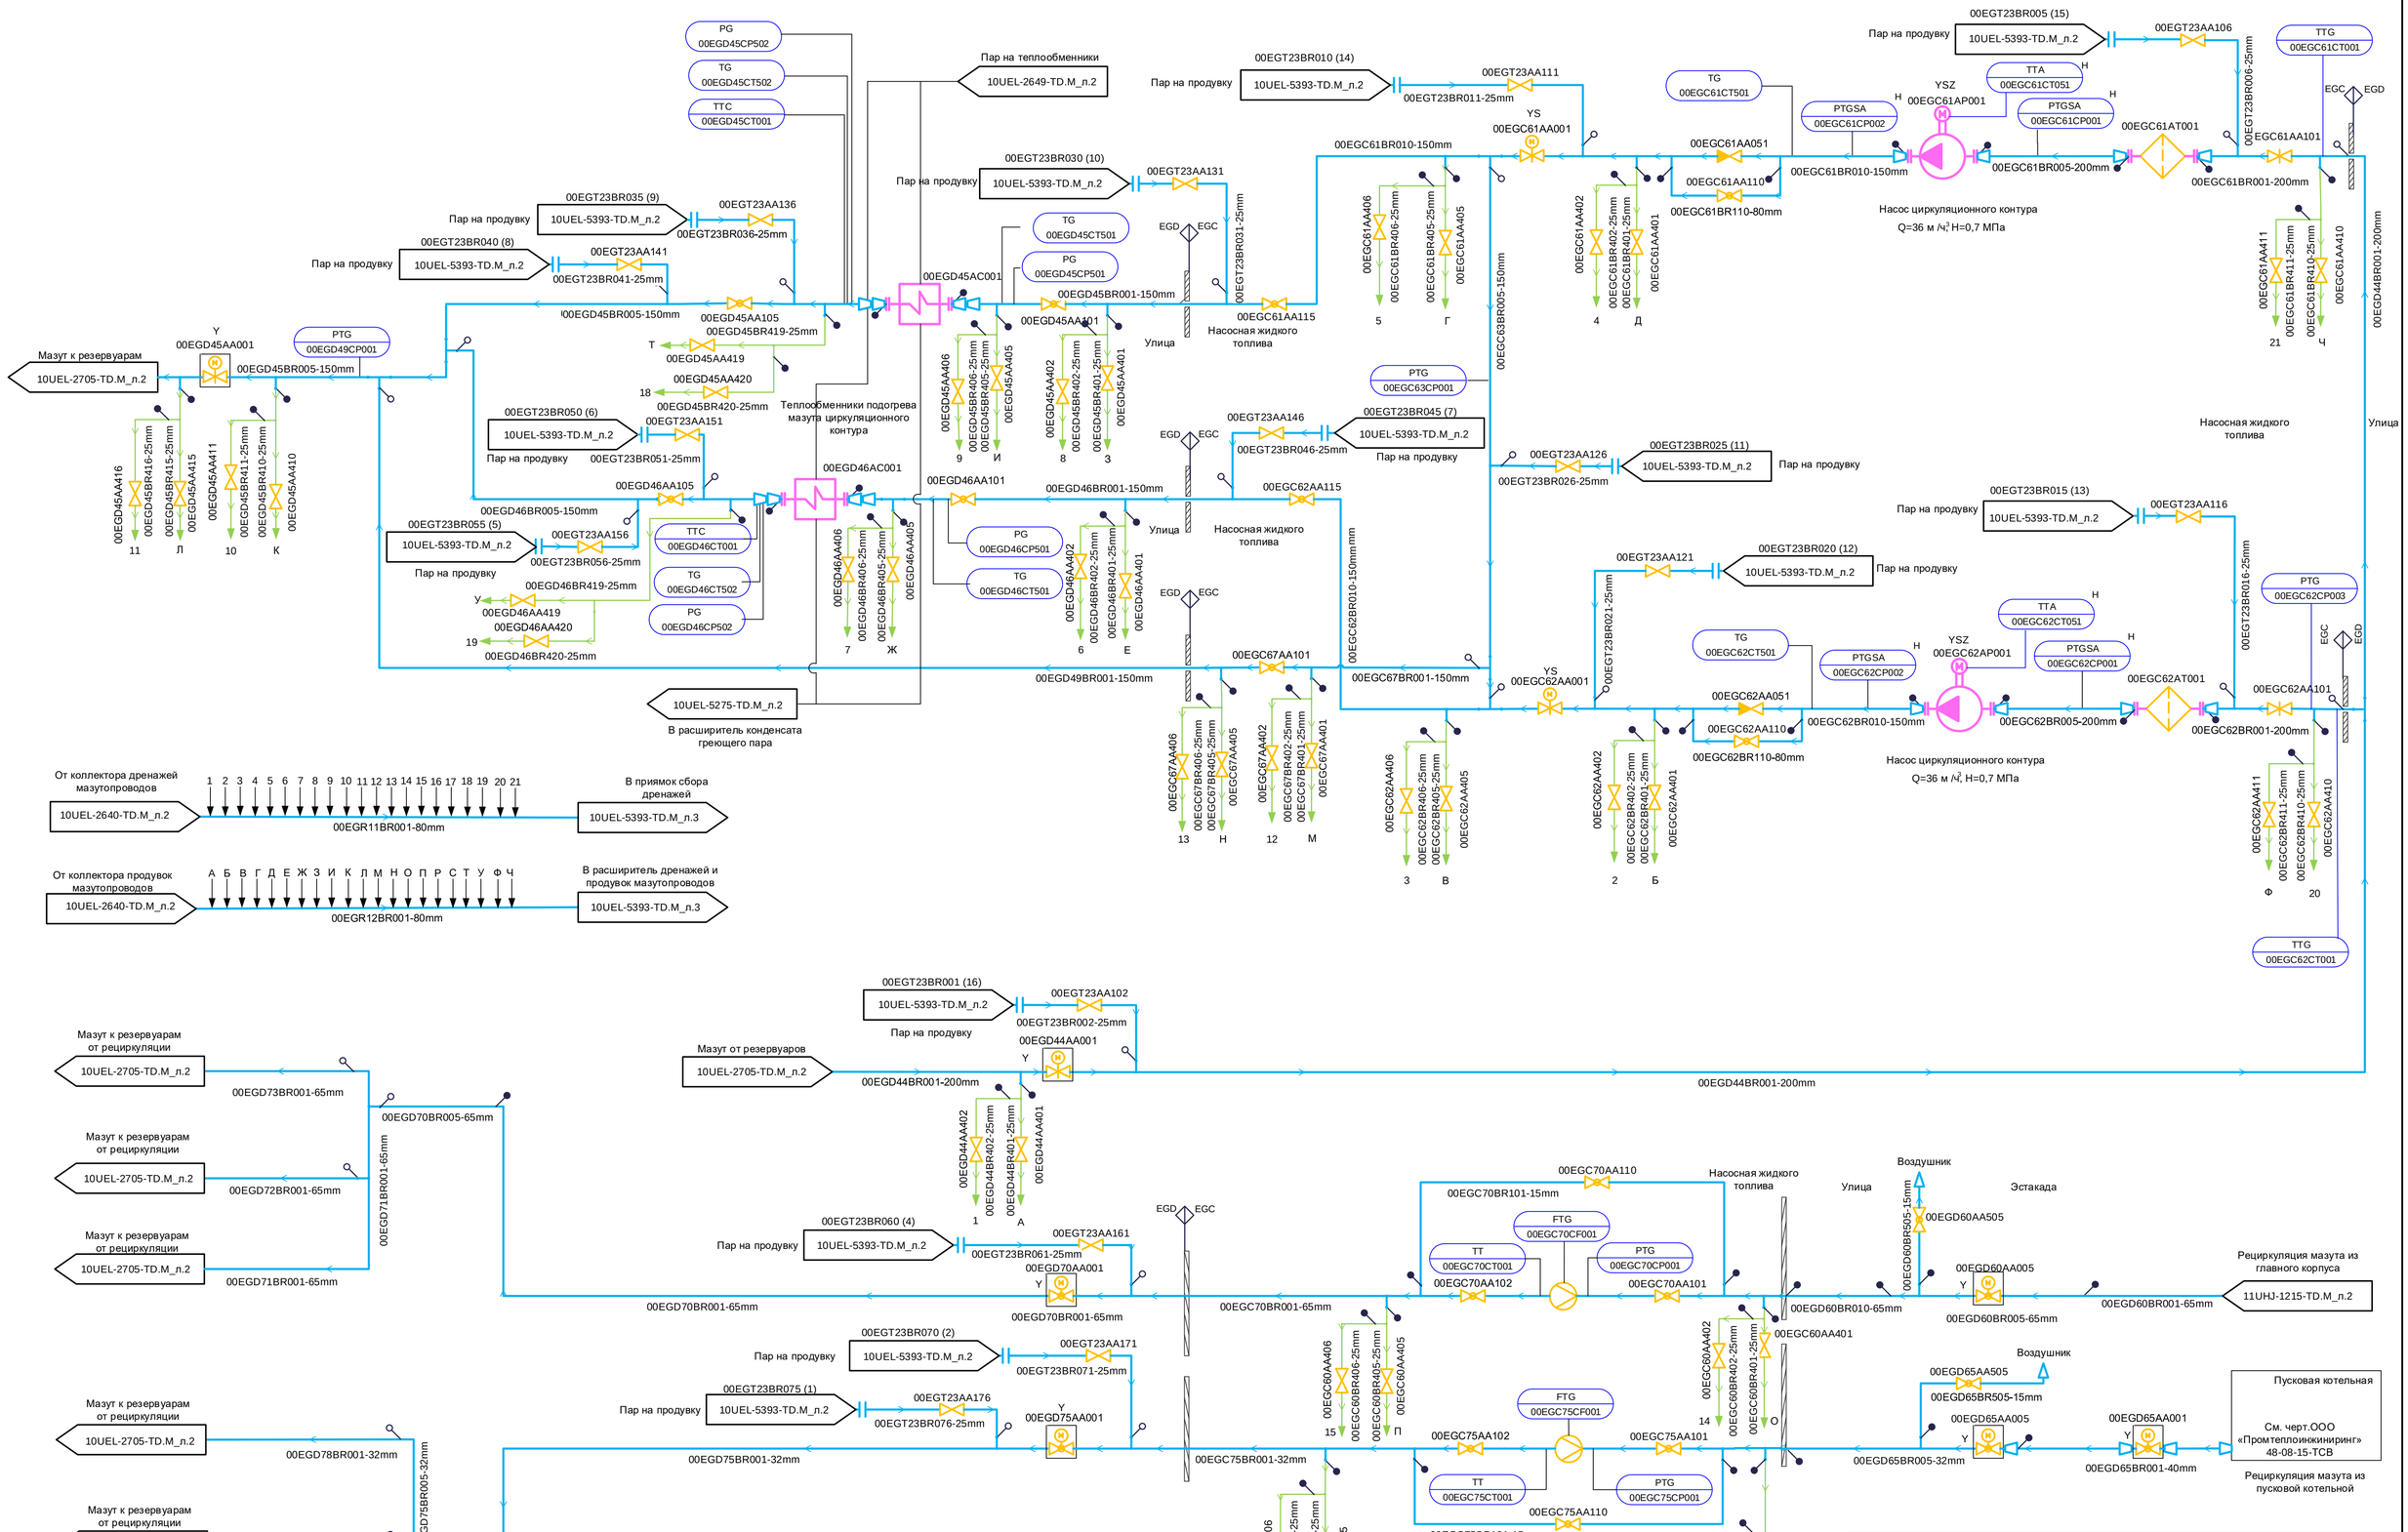

2	-	Зам	918-16			
Изм.	Кол.уч	Лист	№ док.	Подп.	Дата	
Разработал	Полянская					
Проверил	Бобров					
Гл.спец.	Бакатин					
Н. контр.	Гридчина					

132N32-10UEL-5183-TD.M

Строительство Сахалинской ГРЭС-2. Основной производственный комплекс. Внутриплощадочные объекты (1очередь)

Насосная жидкого топлива. PI-диаграмма трубопроводов циркуляционного контура мазута.

Стадия	Лист	Листов
Р	2	

PI-диаграмма трубопроводов циркуляционного контура мазута. Система EGC, EGD

АКЦИОНЕРНОЕ ОБЩЕСТВО ВНИПИЭТ ТЕПЛОЭЛЕКТРОПРОЕКТ г. Москва

Согласовано

ОАСУ

Взам. инв. №

Подпись и дата

Инв. № подл.

Формат А1