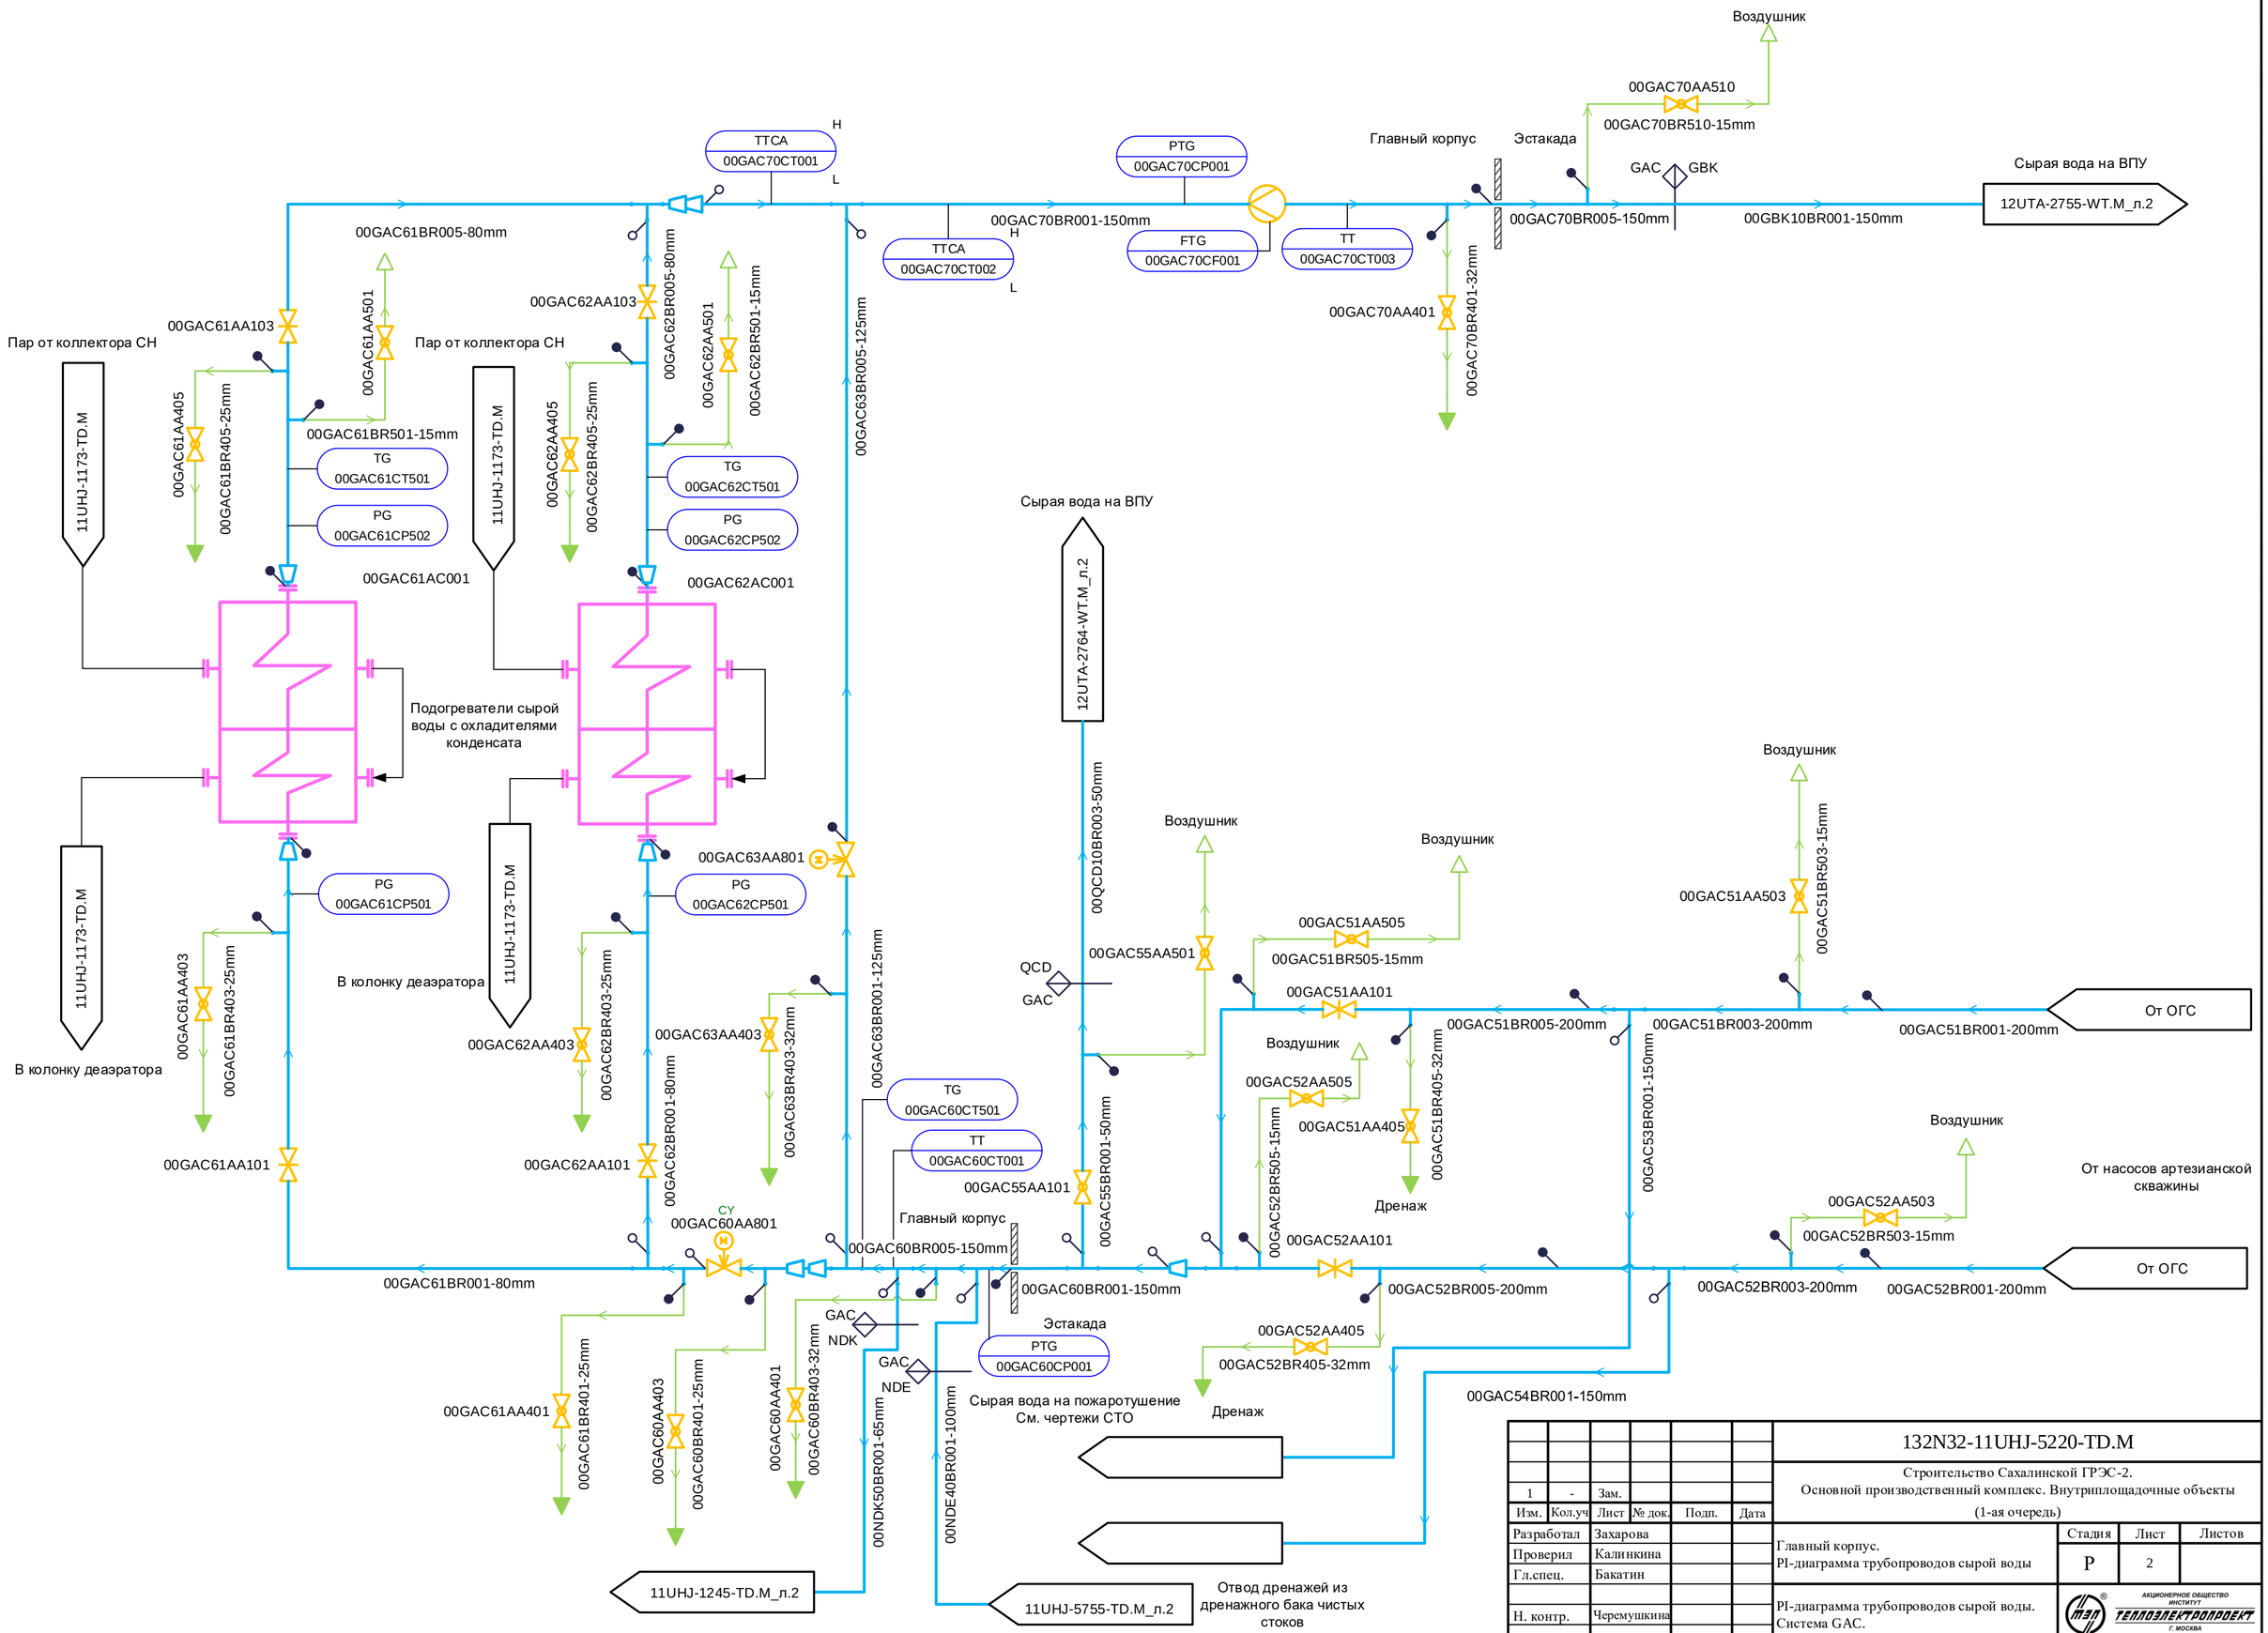

1	-	Зам.				
Изм.	Кол.уч	Лист	№ док.	Подп.	Дата	

132N32-11UHJ-5220-TD.M

Строительство Сахалинской ГРЭС-2.
Основной производственный комплекс. Внутриплощадочные объекты
(1-ая очередь)

Разработал	Захарова	
Проверил	Калинкина	
Гл.спец.	Бакатин	
Н. контр.	Черемушкина	

Главный корпус.
PI-диаграмма трубопроводов сырой воды

Стадия	Лист	Листов
Р	2	

PI-диаграмма трубопроводов сырой воды.
Система GAC.

АКЦИОНЕРНОЕ ОБЩЕСТВО ИНСТИТУТ ТЕПЛОЭЛЕКТРОПРОЕКТ Г. МОСКВА

Согласовано
ОАСУ Владиславлев
Взам. инв. №
Подпись и дата
Инв. № подл.

Формат А2