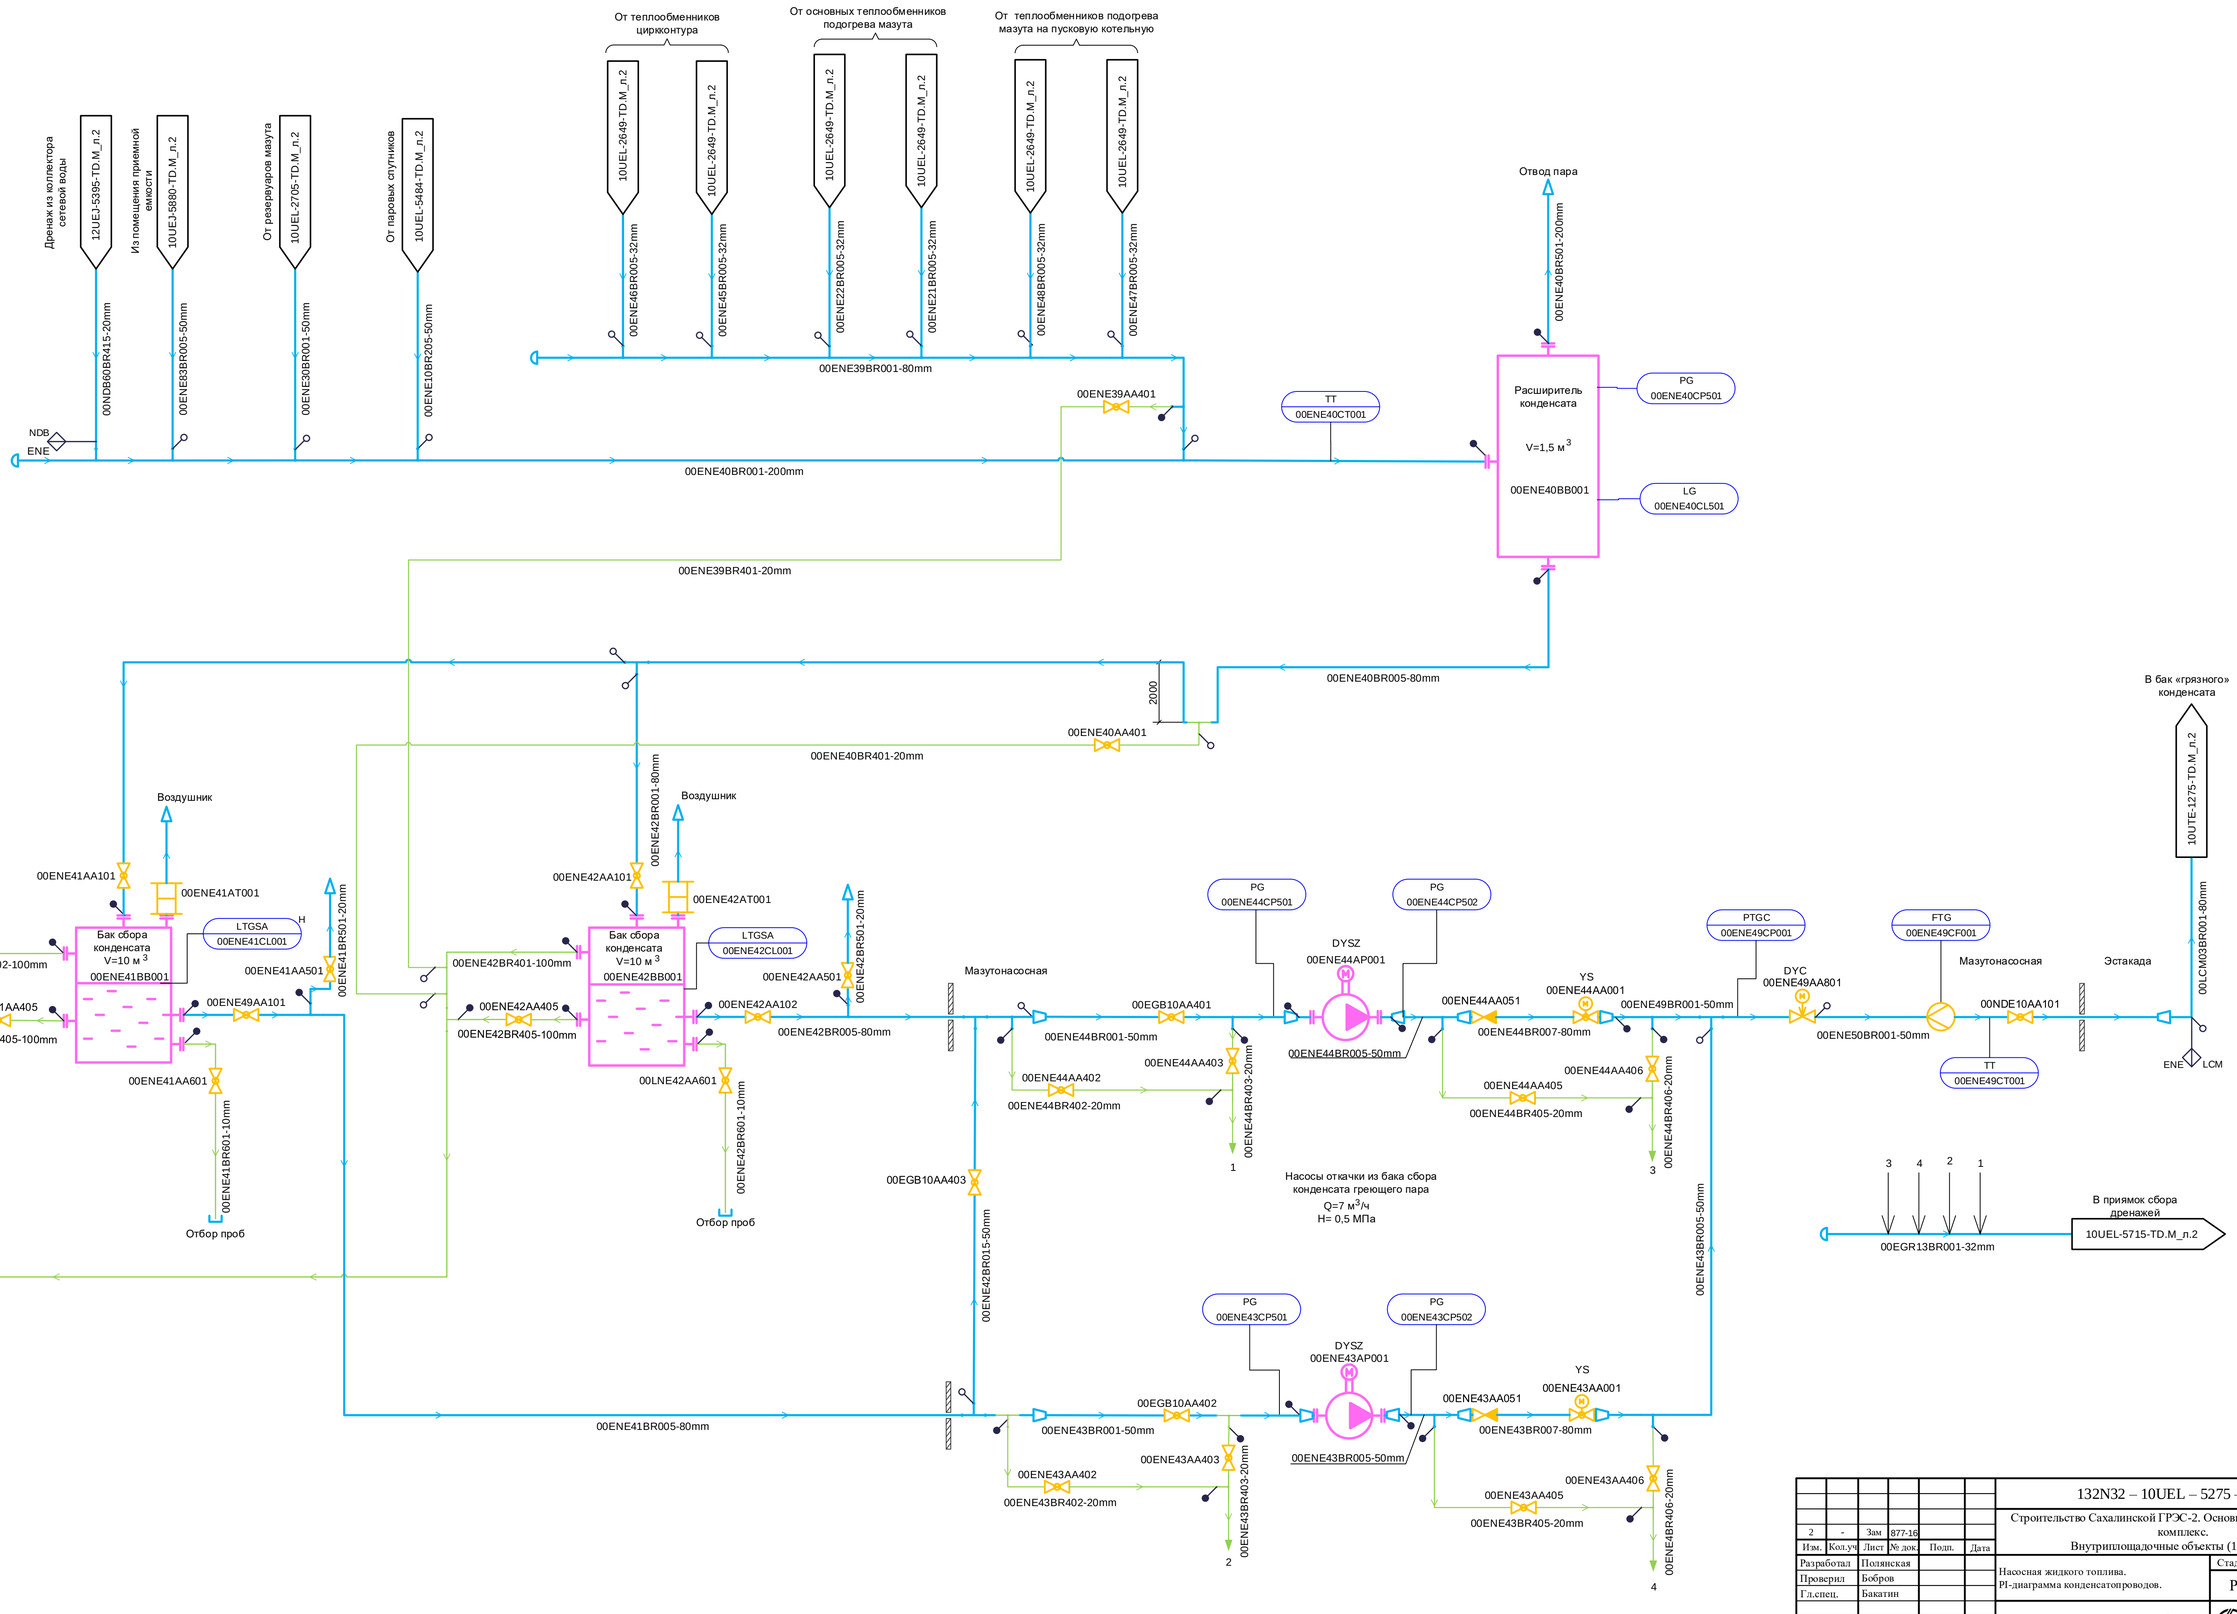

2	-	Зам	877-16			
Изм.	Кол.уч	Лист	№ док.	Подп.	Дата	

132N32 – 10UEL – 5275 – TD.M

Строительство Сахалинской ГРЭС-2. Основной производственный комплекс.
Внуприплощадочные объекты (1-ая очередь)

Разработал	Полянская	
Проверил	Бобров	
Гл.спец.	Бакатин	
Н. контр.	Грядчина	

Насосная жидкого топлива.
PI-диаграмма конденсатопроводов.

Стадия	Лист	Листов
Р	2	

PI-диаграмма конденсатопроводов. Система ENE.

АКЦИОНЕРНОЕ ОБЩЕСТВО ИНСТИТУТ ТЕПЛОЭЛЕКТРОПРОЕКТ г. МОСКВА

Согласовано

ОАСУ

Взам. инв. №

Подпись и дата

Инв. № подл.

Формат А1