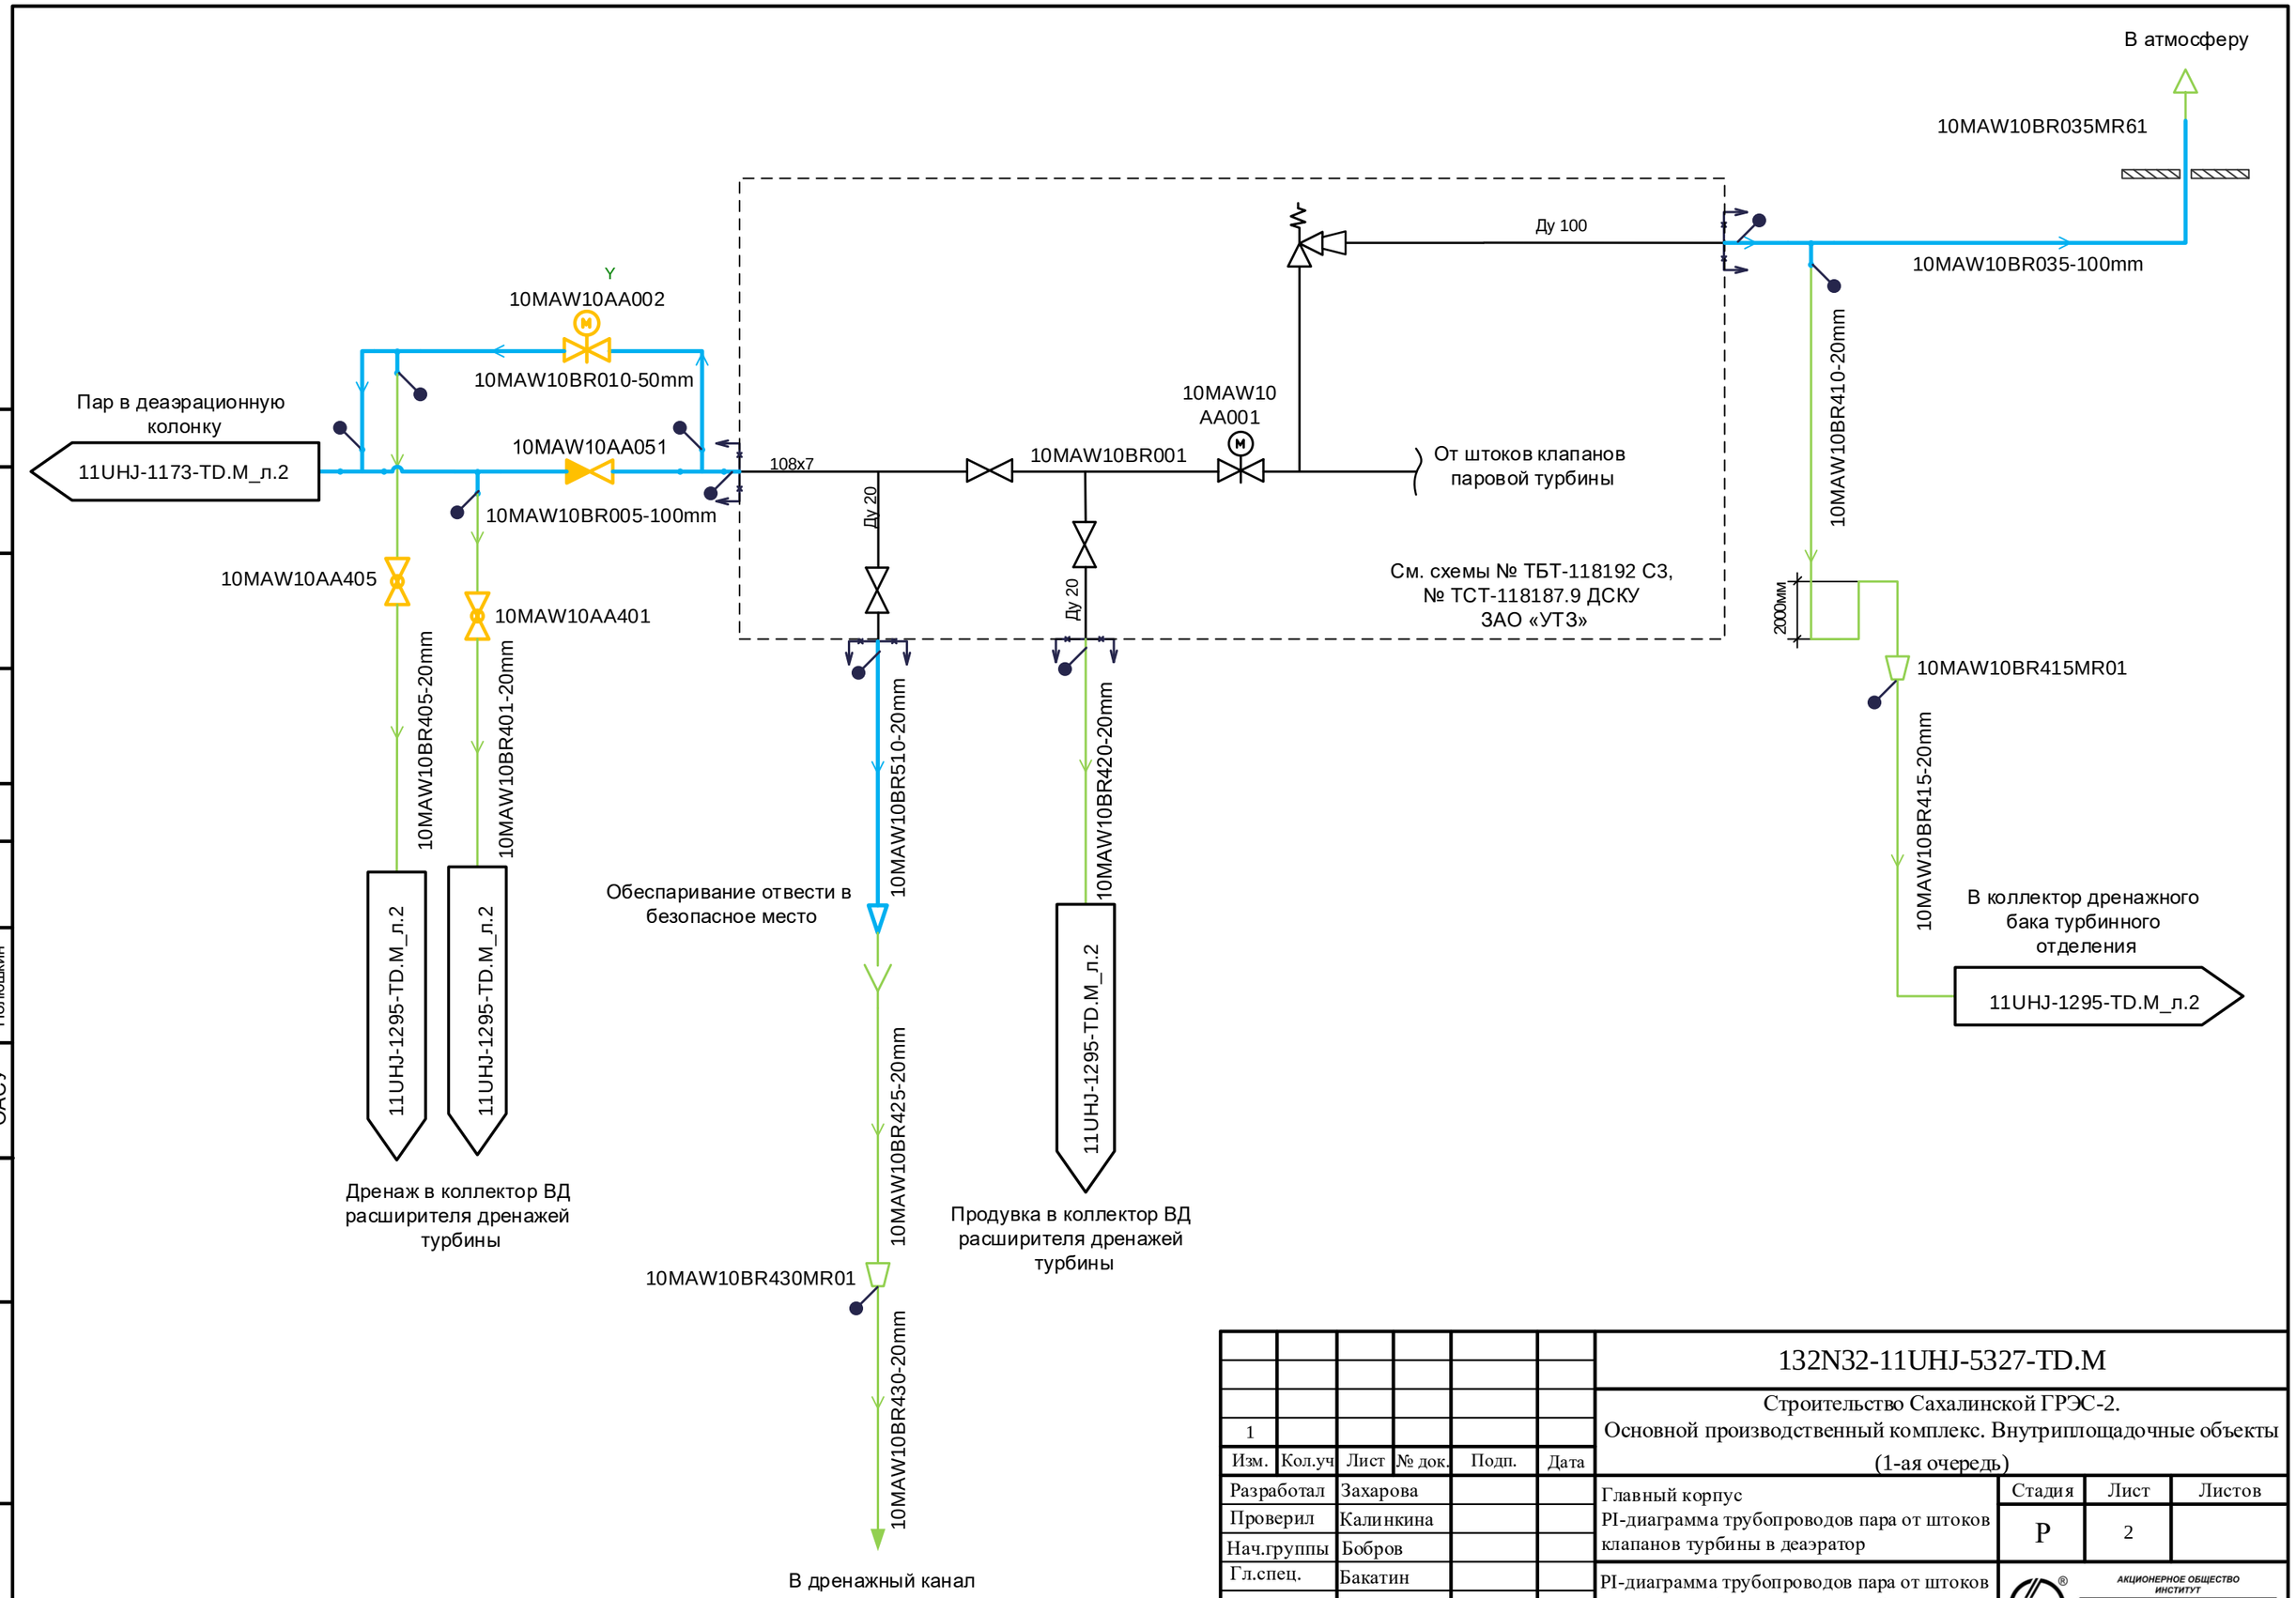

Согласовано

ОАСУ Полюшкин

Взам. инв. №

Подпись и дата

Инв. № подл.

Изм.	Кол.уч	Лист	№ док.	Подп.	Дата
1					
Разработал		Захарова			
Проверил		Калинкина			
Нач.группы		Бобров			
Гл.спец.		Бакатин			
Н. контр.		Черемушкина			

132N32-11UHJ-5327-TD.M

Строительство Сахалинской ГРЭС-2.
Основной производственный комплекс. Внутриплощадочные объекты
(1-ая очередь)

Главный корпус
PI-диаграмма трубопроводов пара от штоков клапанов турбины в деаэратор

Стадия	Лист	Листов
Р	2	

PI-диаграмма трубопроводов пара от штоков клапанов турбины в деаэратор. Система MAW

АКЦИОНЕРНОЕ ОБЩЕСТВО ИНСТИТУТ ТЕПЛОЭЛЕКТРОПРОЕКТ Г. МОСКВА

Формат А3