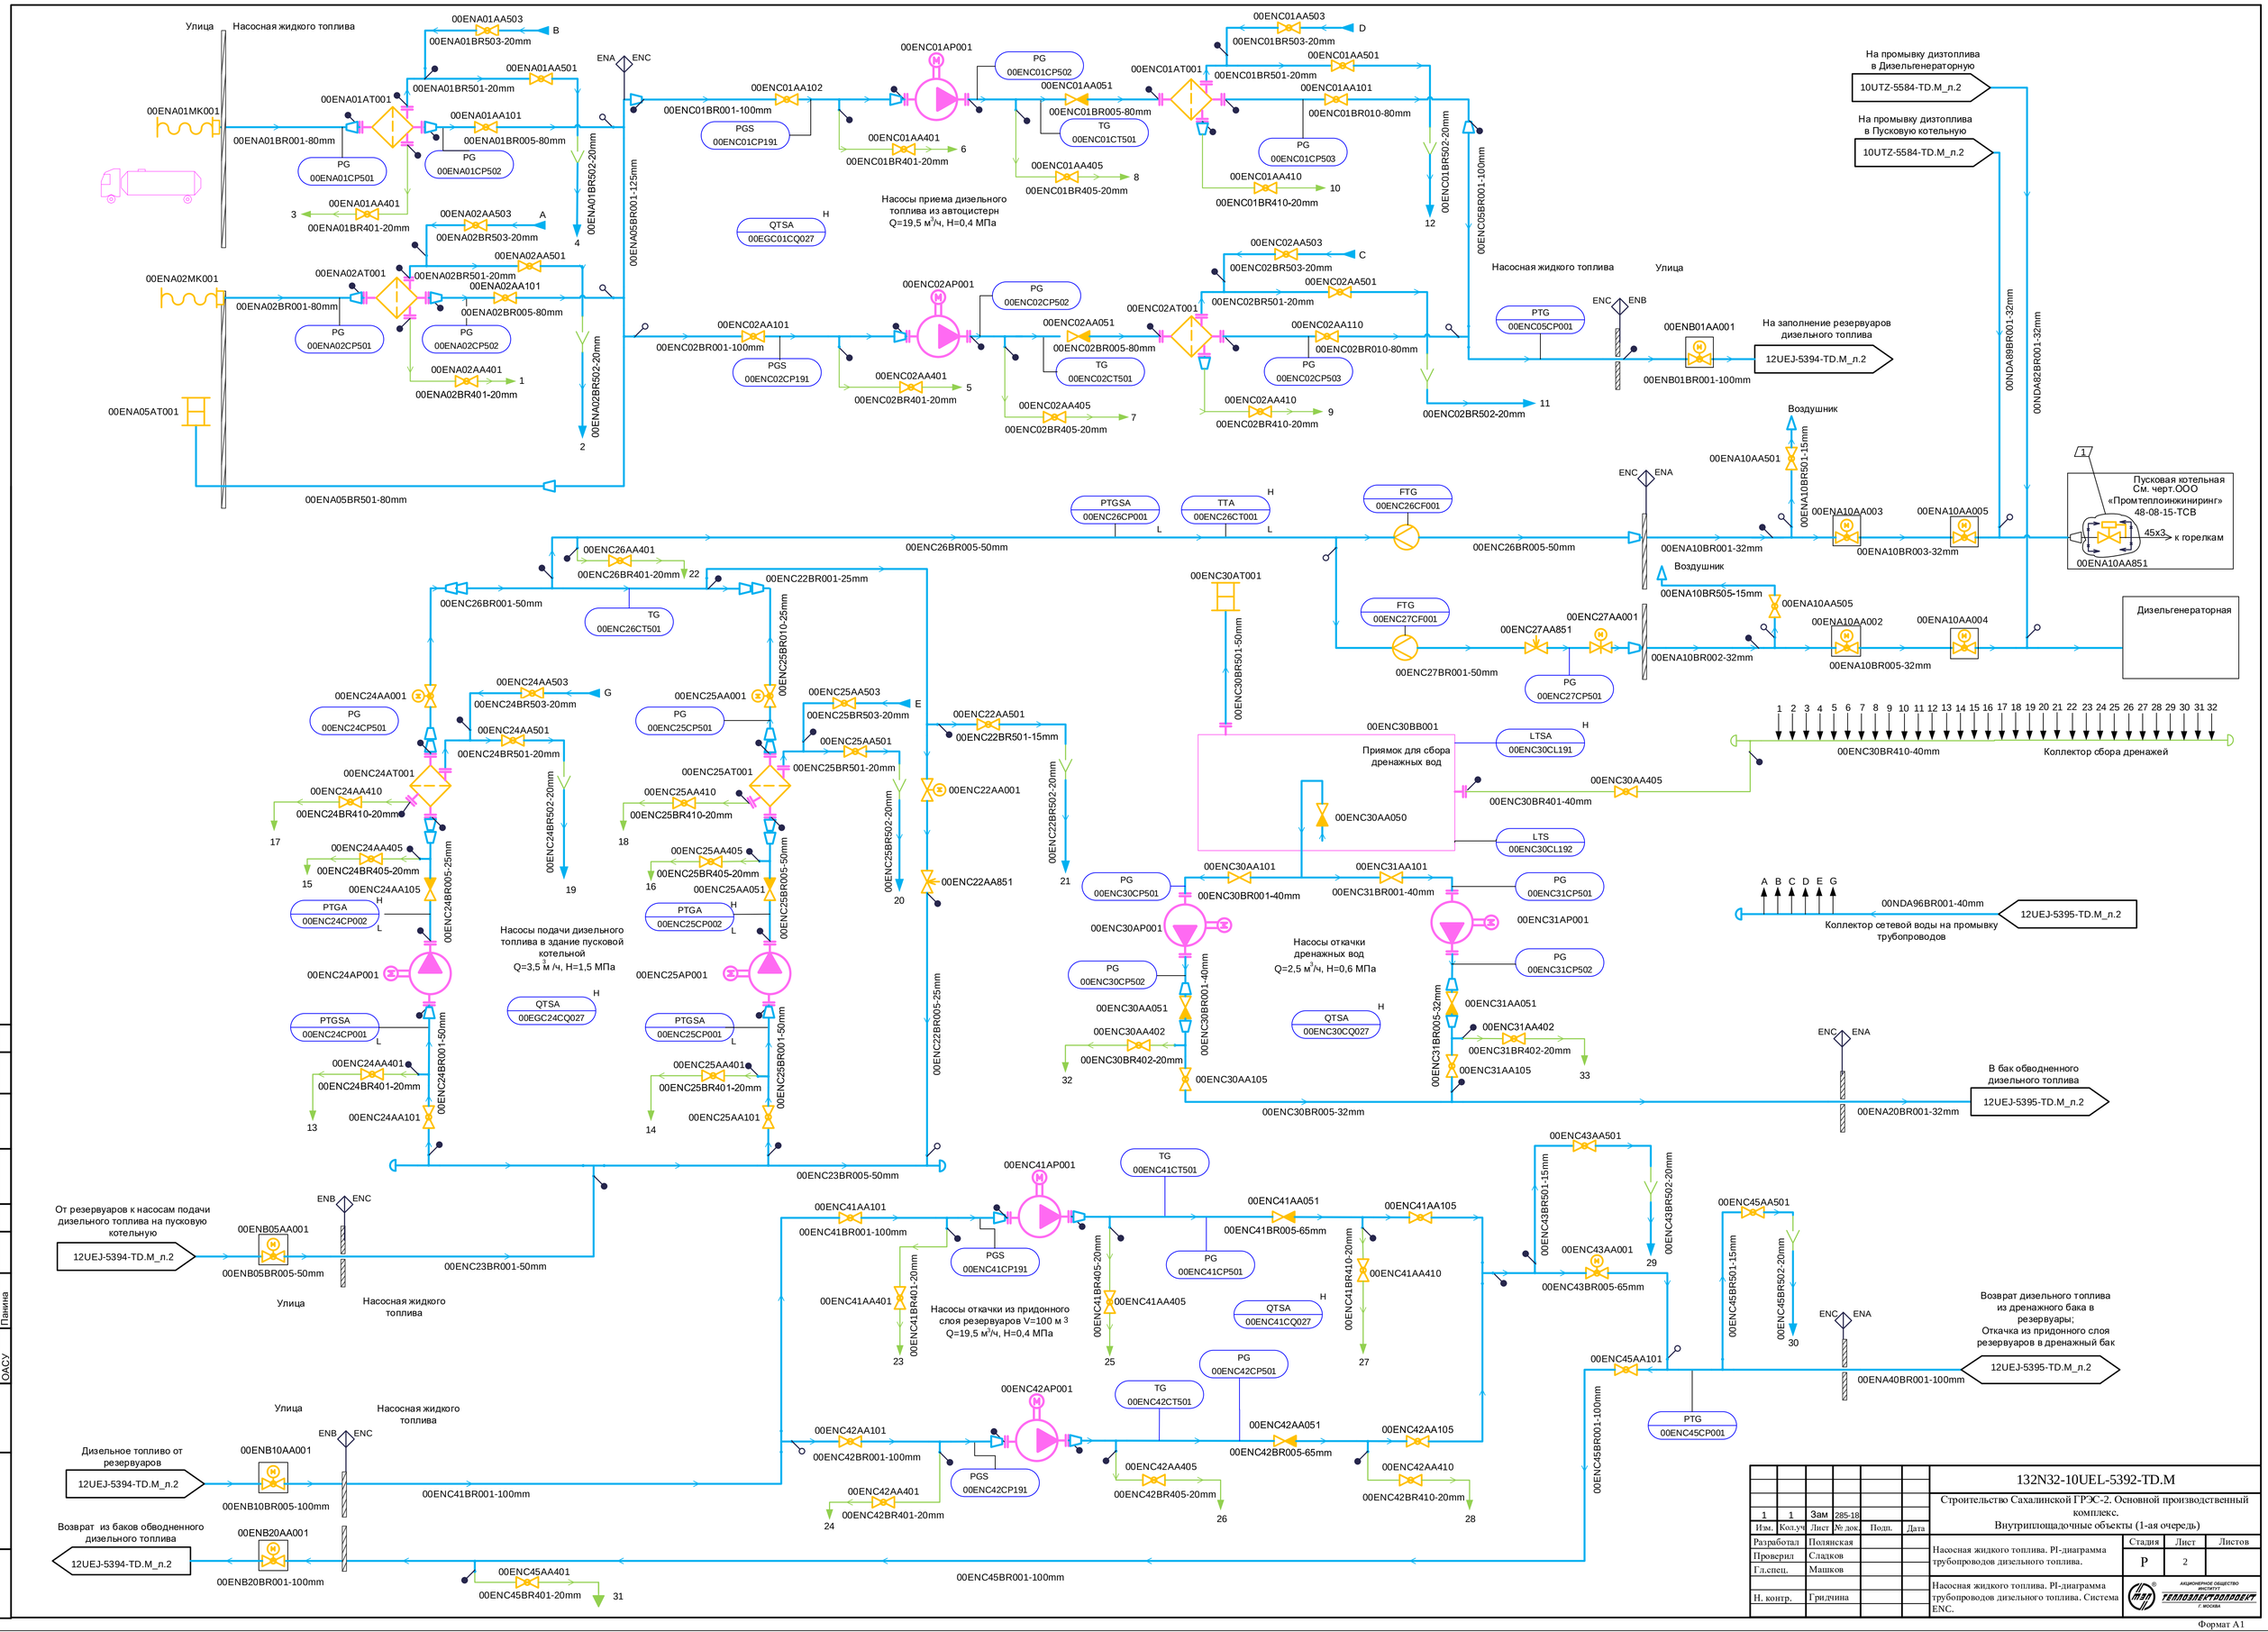
Насосная жидкого топлива
Насосы приема дизельного топлива из автоцистерн Q=19,5 м³/ч, H=0,4 МПа
Насосы подачи дизельного топлива в здание пусковой котельной Q=3,5 м³/ч, H=1,5 МПа
Насосы откачки дренажных вод Q=2,5 м³/ч, H=0,6 МПа
Насосы откачки из придонного слоя резервуаров V=100 м³ Q=19,5 м³/ч, H=0,4 МПа
Приямок для сбора дренажных вод
На промывку дизтоплива в Дизельгенераторную
На промывку дизтоплива в Пусковую котельную
На заполнение резервуаров дизельного топлива
Пусковая котельная См. черт.ООО «Промтеплоинжиниринг» 48-08-15-ТСВ
Дизельгенераторная
Коллектор сбора дренажей
Коллектор сетевой воды на промывку трубопроводов
В бак обводненного дизельного топлива
Возврат дизельного топлива из дренажного бака в резервуары; Откачка из придонного слоя резервуаров в дренажный бак
От резервуаров к насосам подачи дизельного топлива на пусковую котельную
Дизельное топливо от резервуаров
Возврат из баков обводненного дизельного топлива
Улица
Воздушник
132N32-10UEL-5392-TD.M
Строительство Сахалинской ГРЭС-2. Основной производственный комплекс. Внутриплощадочные объекты (1-ая очередь)
Насосная жидкого топлива. PI-диаграмма трубопроводов дизельного топлива.
Насосная жидкого топлива. PI-диаграмма трубопроводов дизельного топлива. Система ENC.
Разработал Полянская
Проверил Сладков
Гл.спец. Машков
Н. контр. Грядчина
Стадия P
Лист 2
Листов
АКЦИОНЕРНОЕ ОБЩЕСТВО ВНИИПИ ТЕПЛОЭЛЕКТРОПРОЕКТ г. МОСКВА
Формат А1