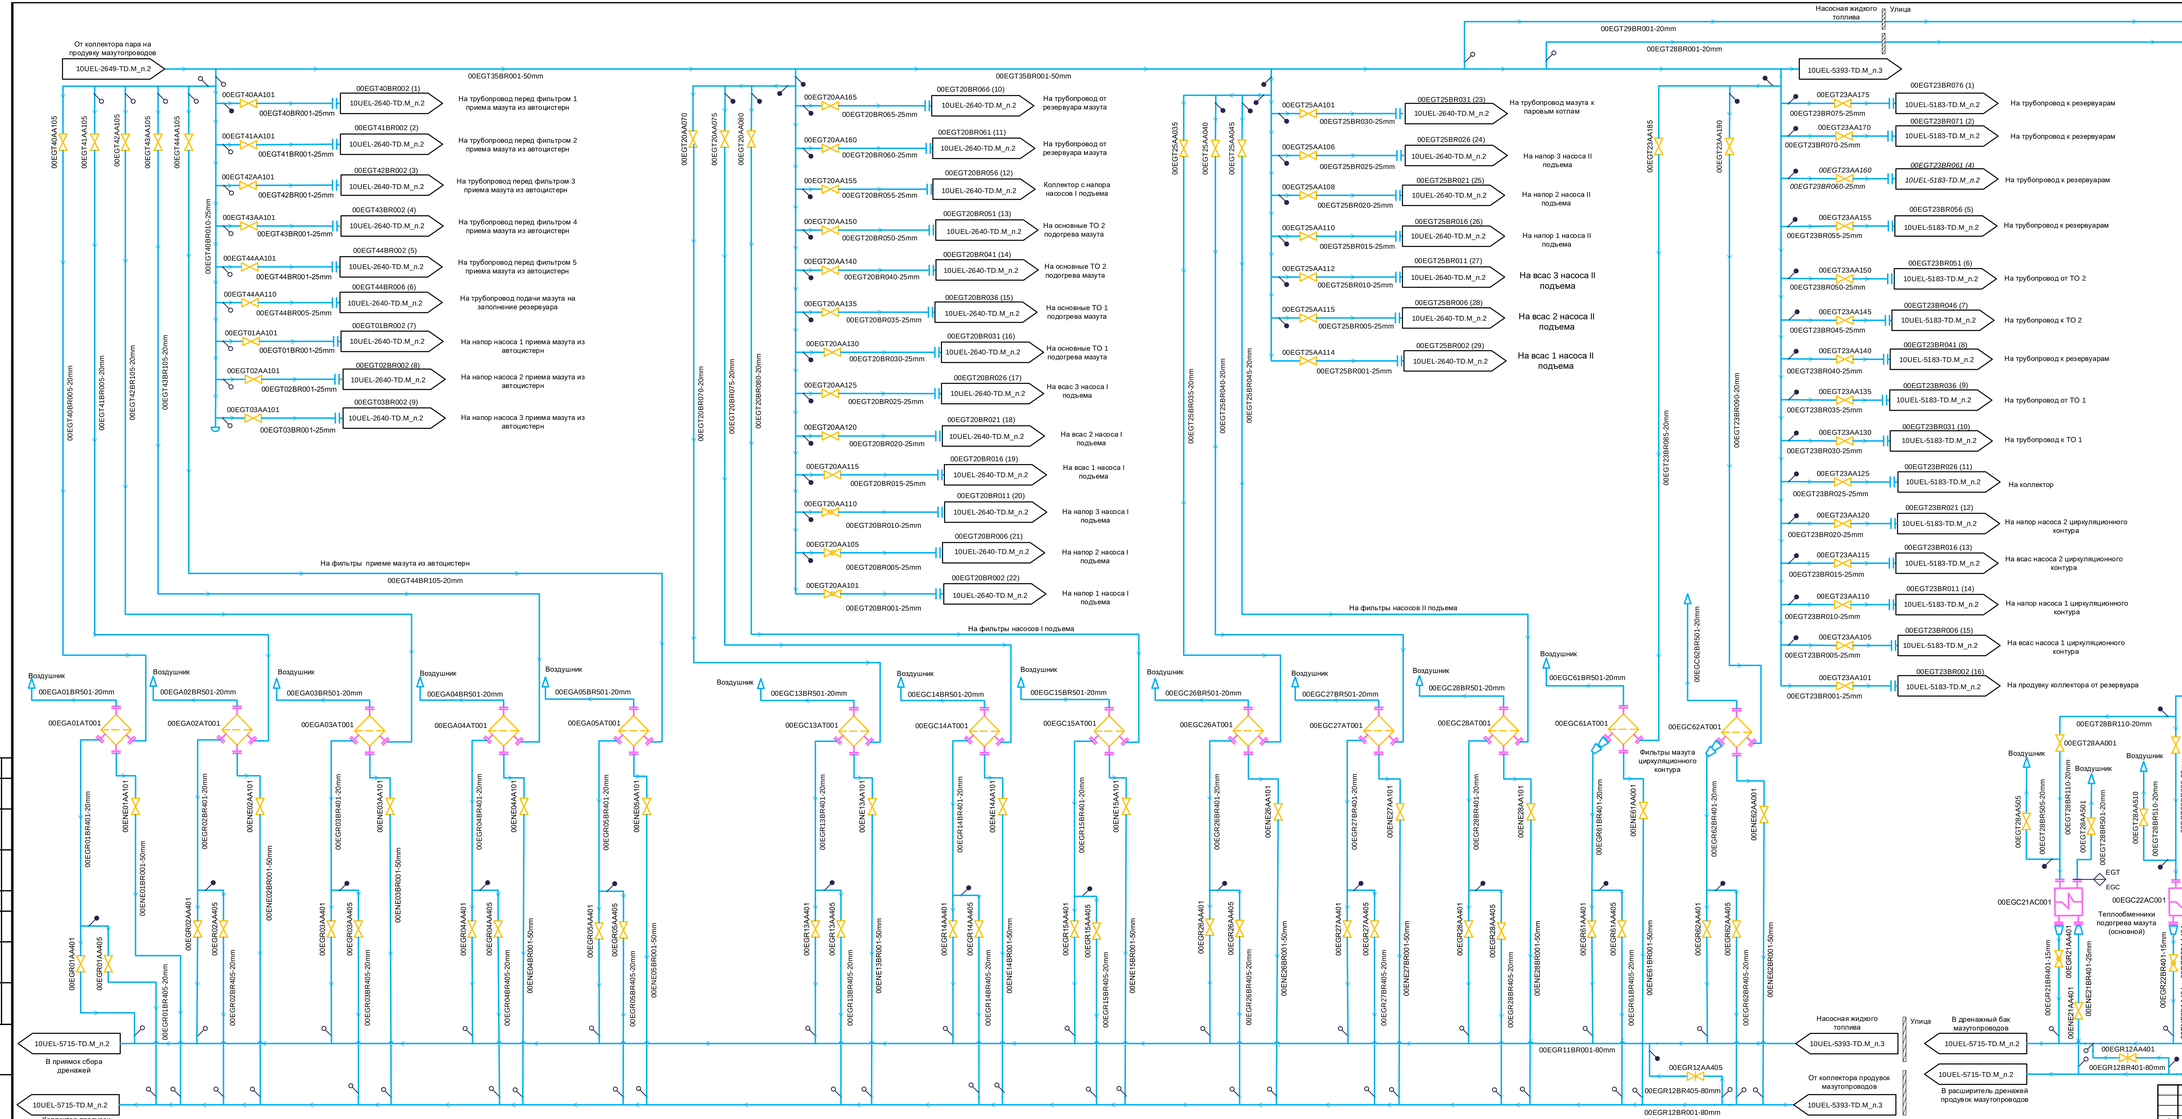

2	-	Зам	74-17				
Изм.	Кол.уч.	Лист	№ док.	Подп.	Дата		
Разработал	Полянская						
Проверил	Бобров						
Гл.спец.	Егоров						
Н. контр.	Грицечка						

Строительство Сахалинской ГРЭС-2. Основной производственный комплекс.
Внутрипродуктовые объекты (1-ая очередь)

132N32 – 10UEL – 5393 – TD.M

Насосная жидкого топлива.
PI-диаграмма опорожнения и продувок оборудования

PI-диаграмма опорожнения и продувок оборудования. Системы EGT, EGR.

Стадия	Лист	Листов
Р	2	

ОБЪЕДИНЕНИЕ ЮЖНОЕ ТЕПЛОЭНЕРГОМОНТАЖ

Согласовано

Взам. инв. №

Подпись и дата

Инв. № подл.

Формат А2х3