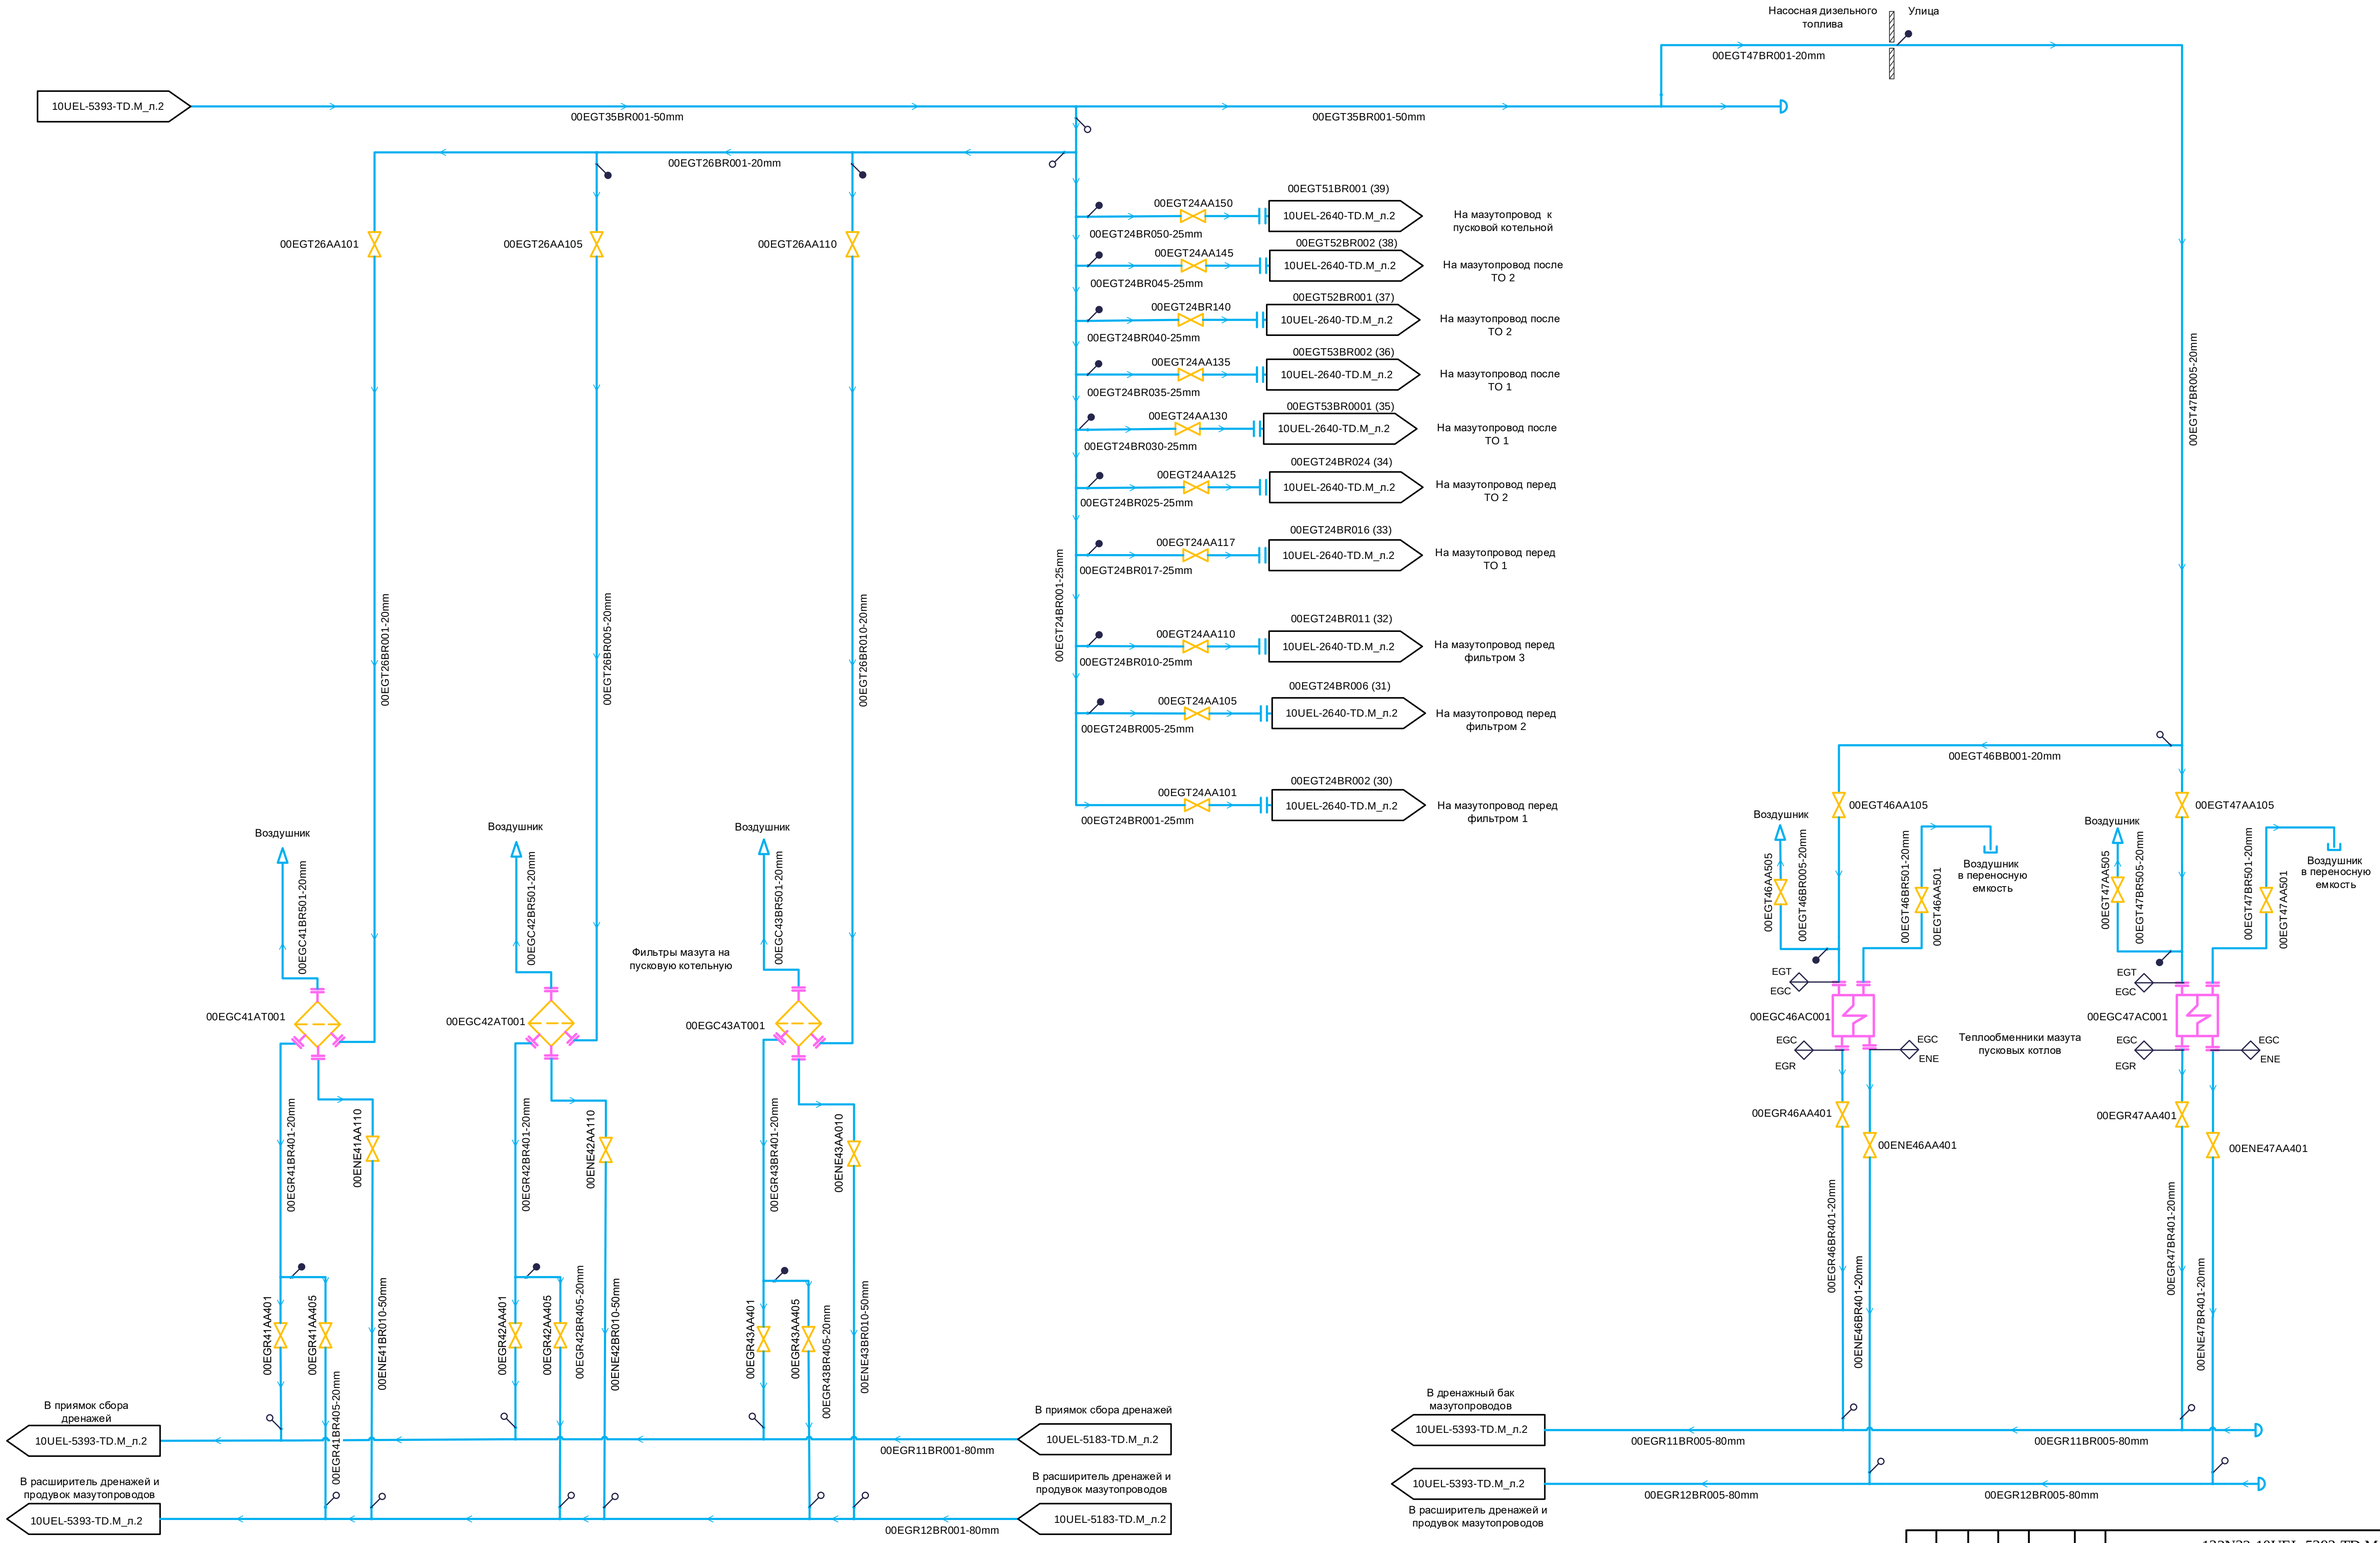

2	-	Зам	74-17			
Изм.	Кол.уч	Лист	№ док.	Подп.	Дата	

132N32-10UEL-5393-TD.M

Строительство Сахалинской ГРЭС-2. Основной производственный комплекс.
Внутриплощадочные объекты (1-ая очередь)

Разработал	Полянская	
Проверил	Бобров	
Гл.спец.	Егоров	
Н. контр.	Грядчина	

Насосная жидкого топлива.
PI-диаграмма опорожнения и продувок оборудования

Стадия	Лист	Листов
Р	3	

PI-диаграмма опорожнения и продувок оборудования. Системы EGT, EGR.

АКЦИОНЕРНОЕ ОБЩЕСТВО ВНИПИЭТ ТЕПЛОЭЛЕКТРОПРОЕКТ г. МОСКВА

Согласовано

ОАСУ

Взам. инв. №

Подпись и дата

Инв. № подл.

Формат А1