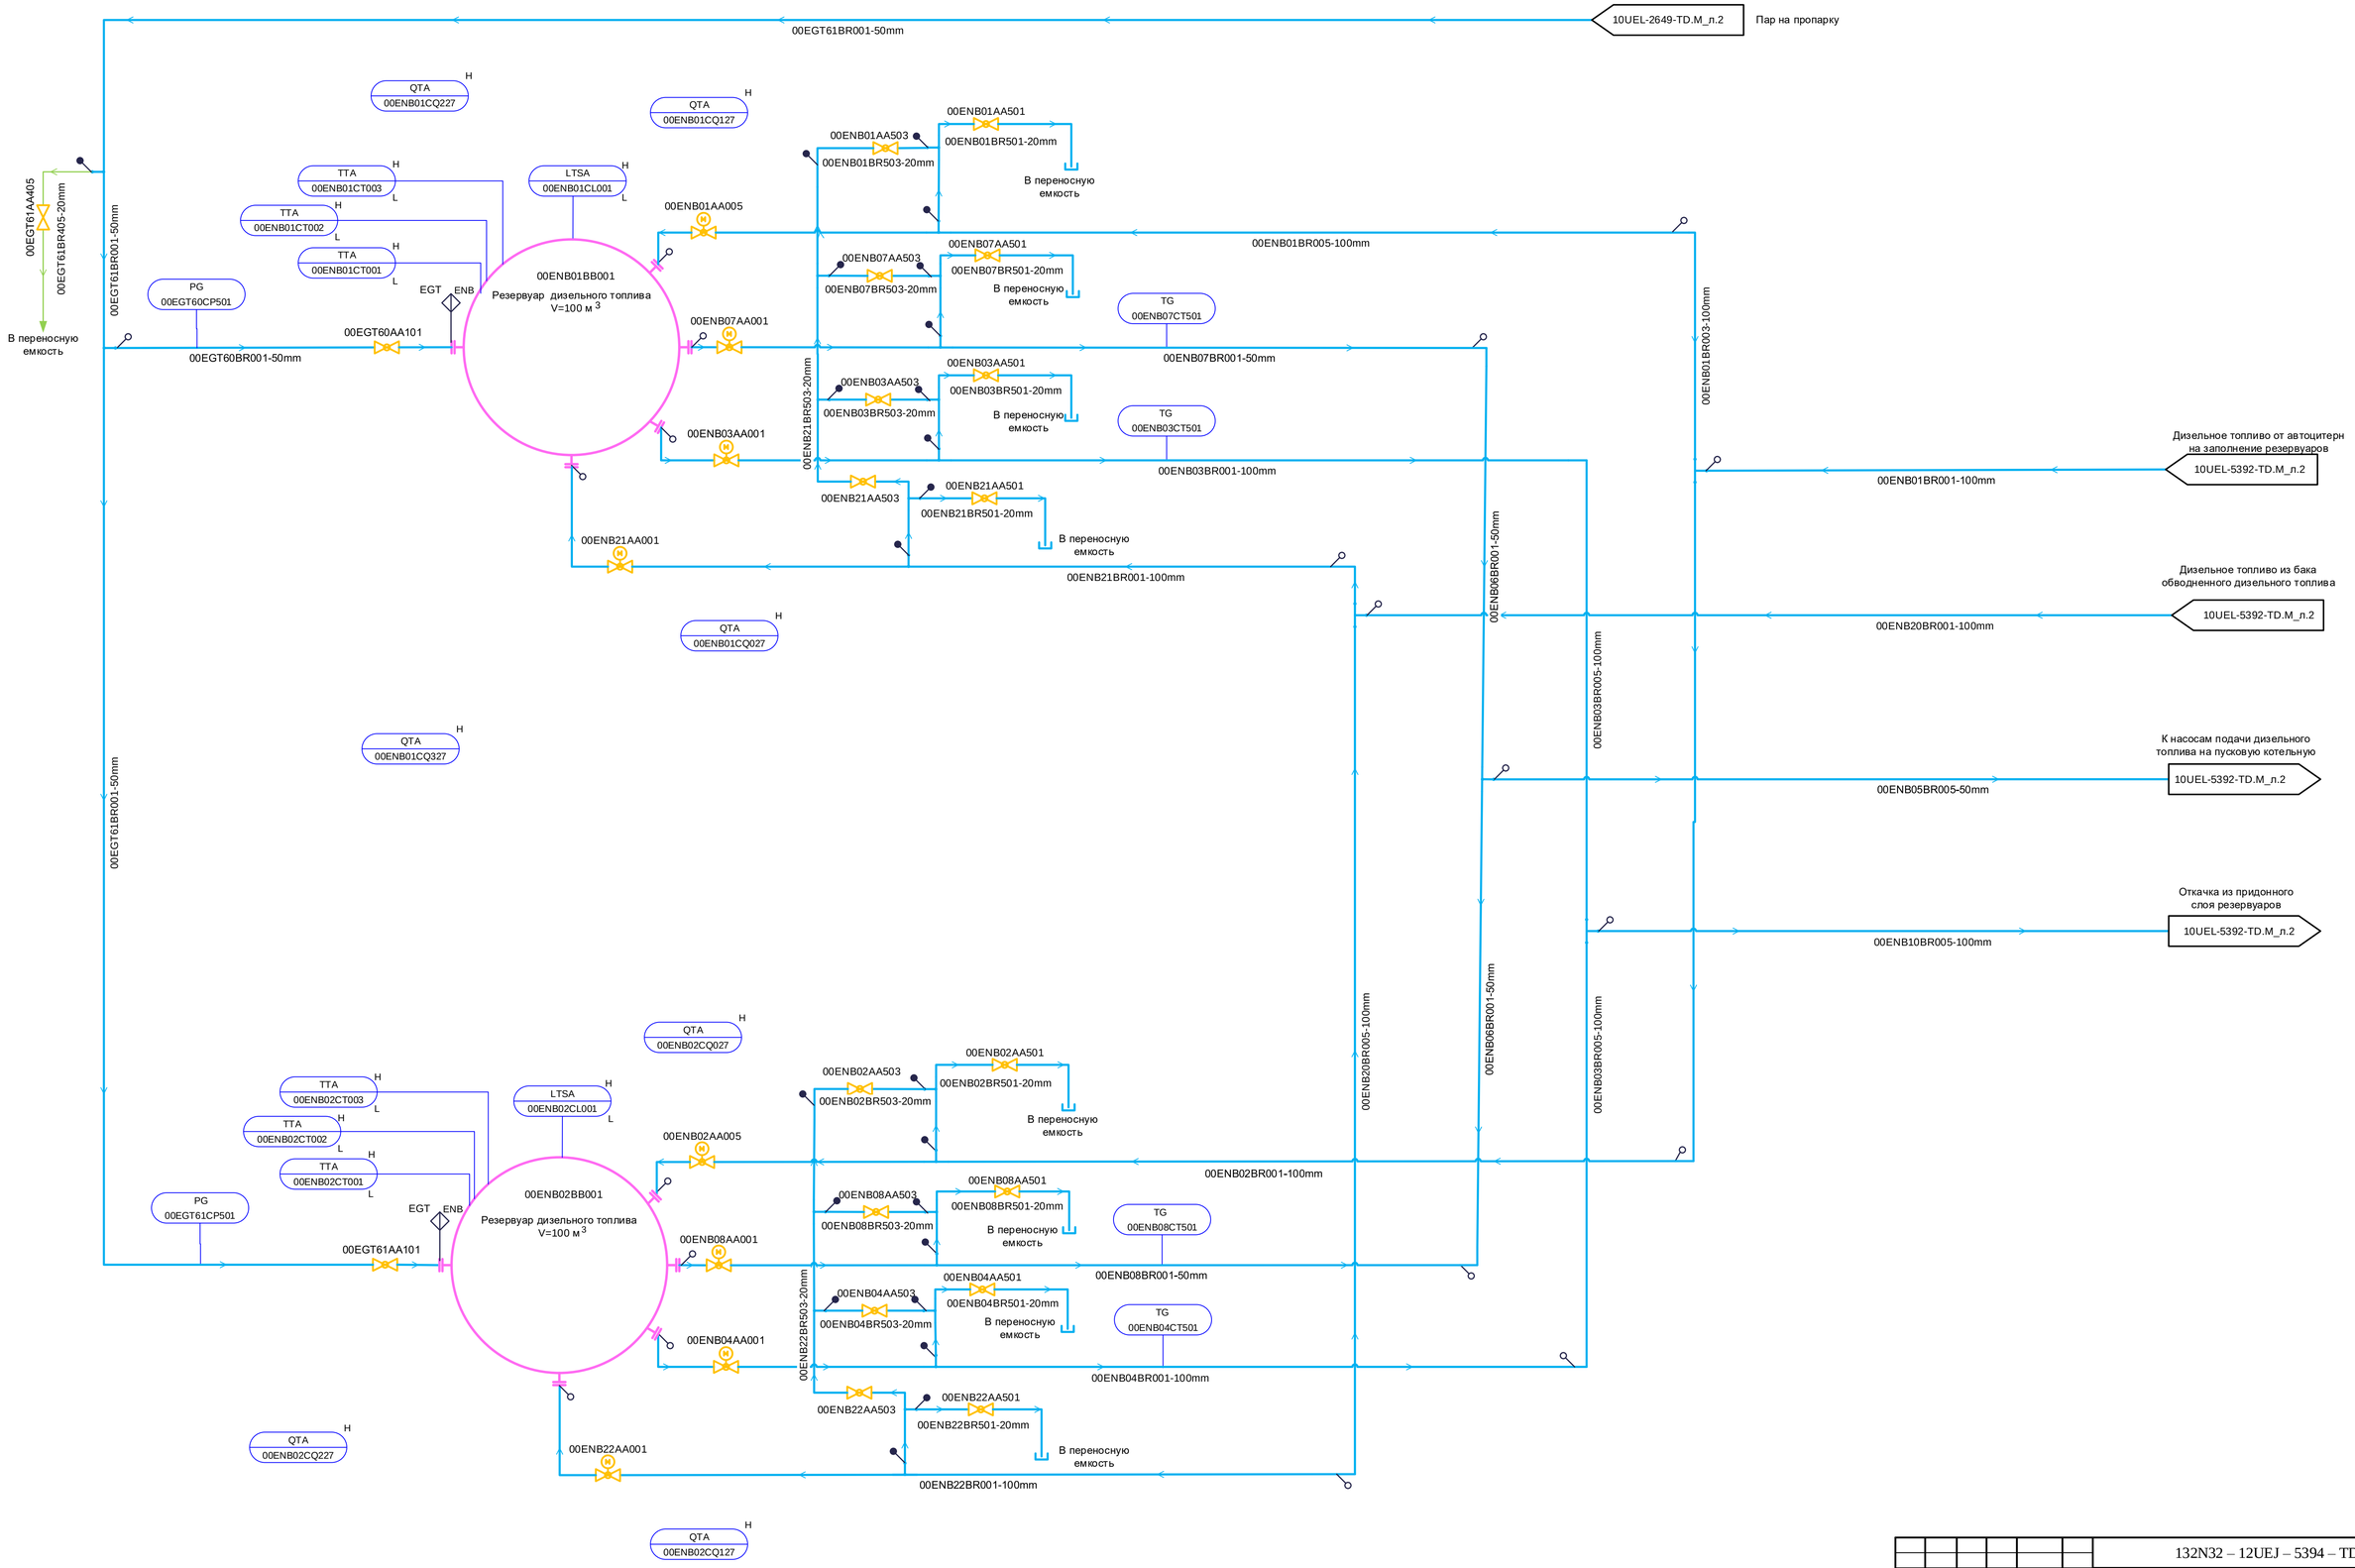

Согласовано

ОАСУ

Взам. инв. №

Подпись и дата

Инв. № подл.

1	-	Зам	98-17			
Изм.	Кол.уч	Лист	№ док.	Подп.	Дата	

132N32 – 12UEJ – 5394 – TD.M

Строительство Сахалинской ГРЭС-2. Основной производственный комплекс.
Внутриплощадочные объекты (1-ая очередь)

Разработал	Полянская	
Проверил	Бобров	
Гл.спец.	Егоров	
Н. контр.	Гридчина	

Склад дизельного топлива.
PI-диаграмма обвязки резервуаров дизельного топлива.

PI-диаграмма обвязки резервуаров дизельного топлива. Система ENB.

Стадия	Лист	Листов
Р	2	

АКЦИОНЕРНОЕ ОБЩЕСТВО ВНИИПИ ТЕПЛОЭЛЕКТРОПРОЕКТ г. Москва

Формат А1