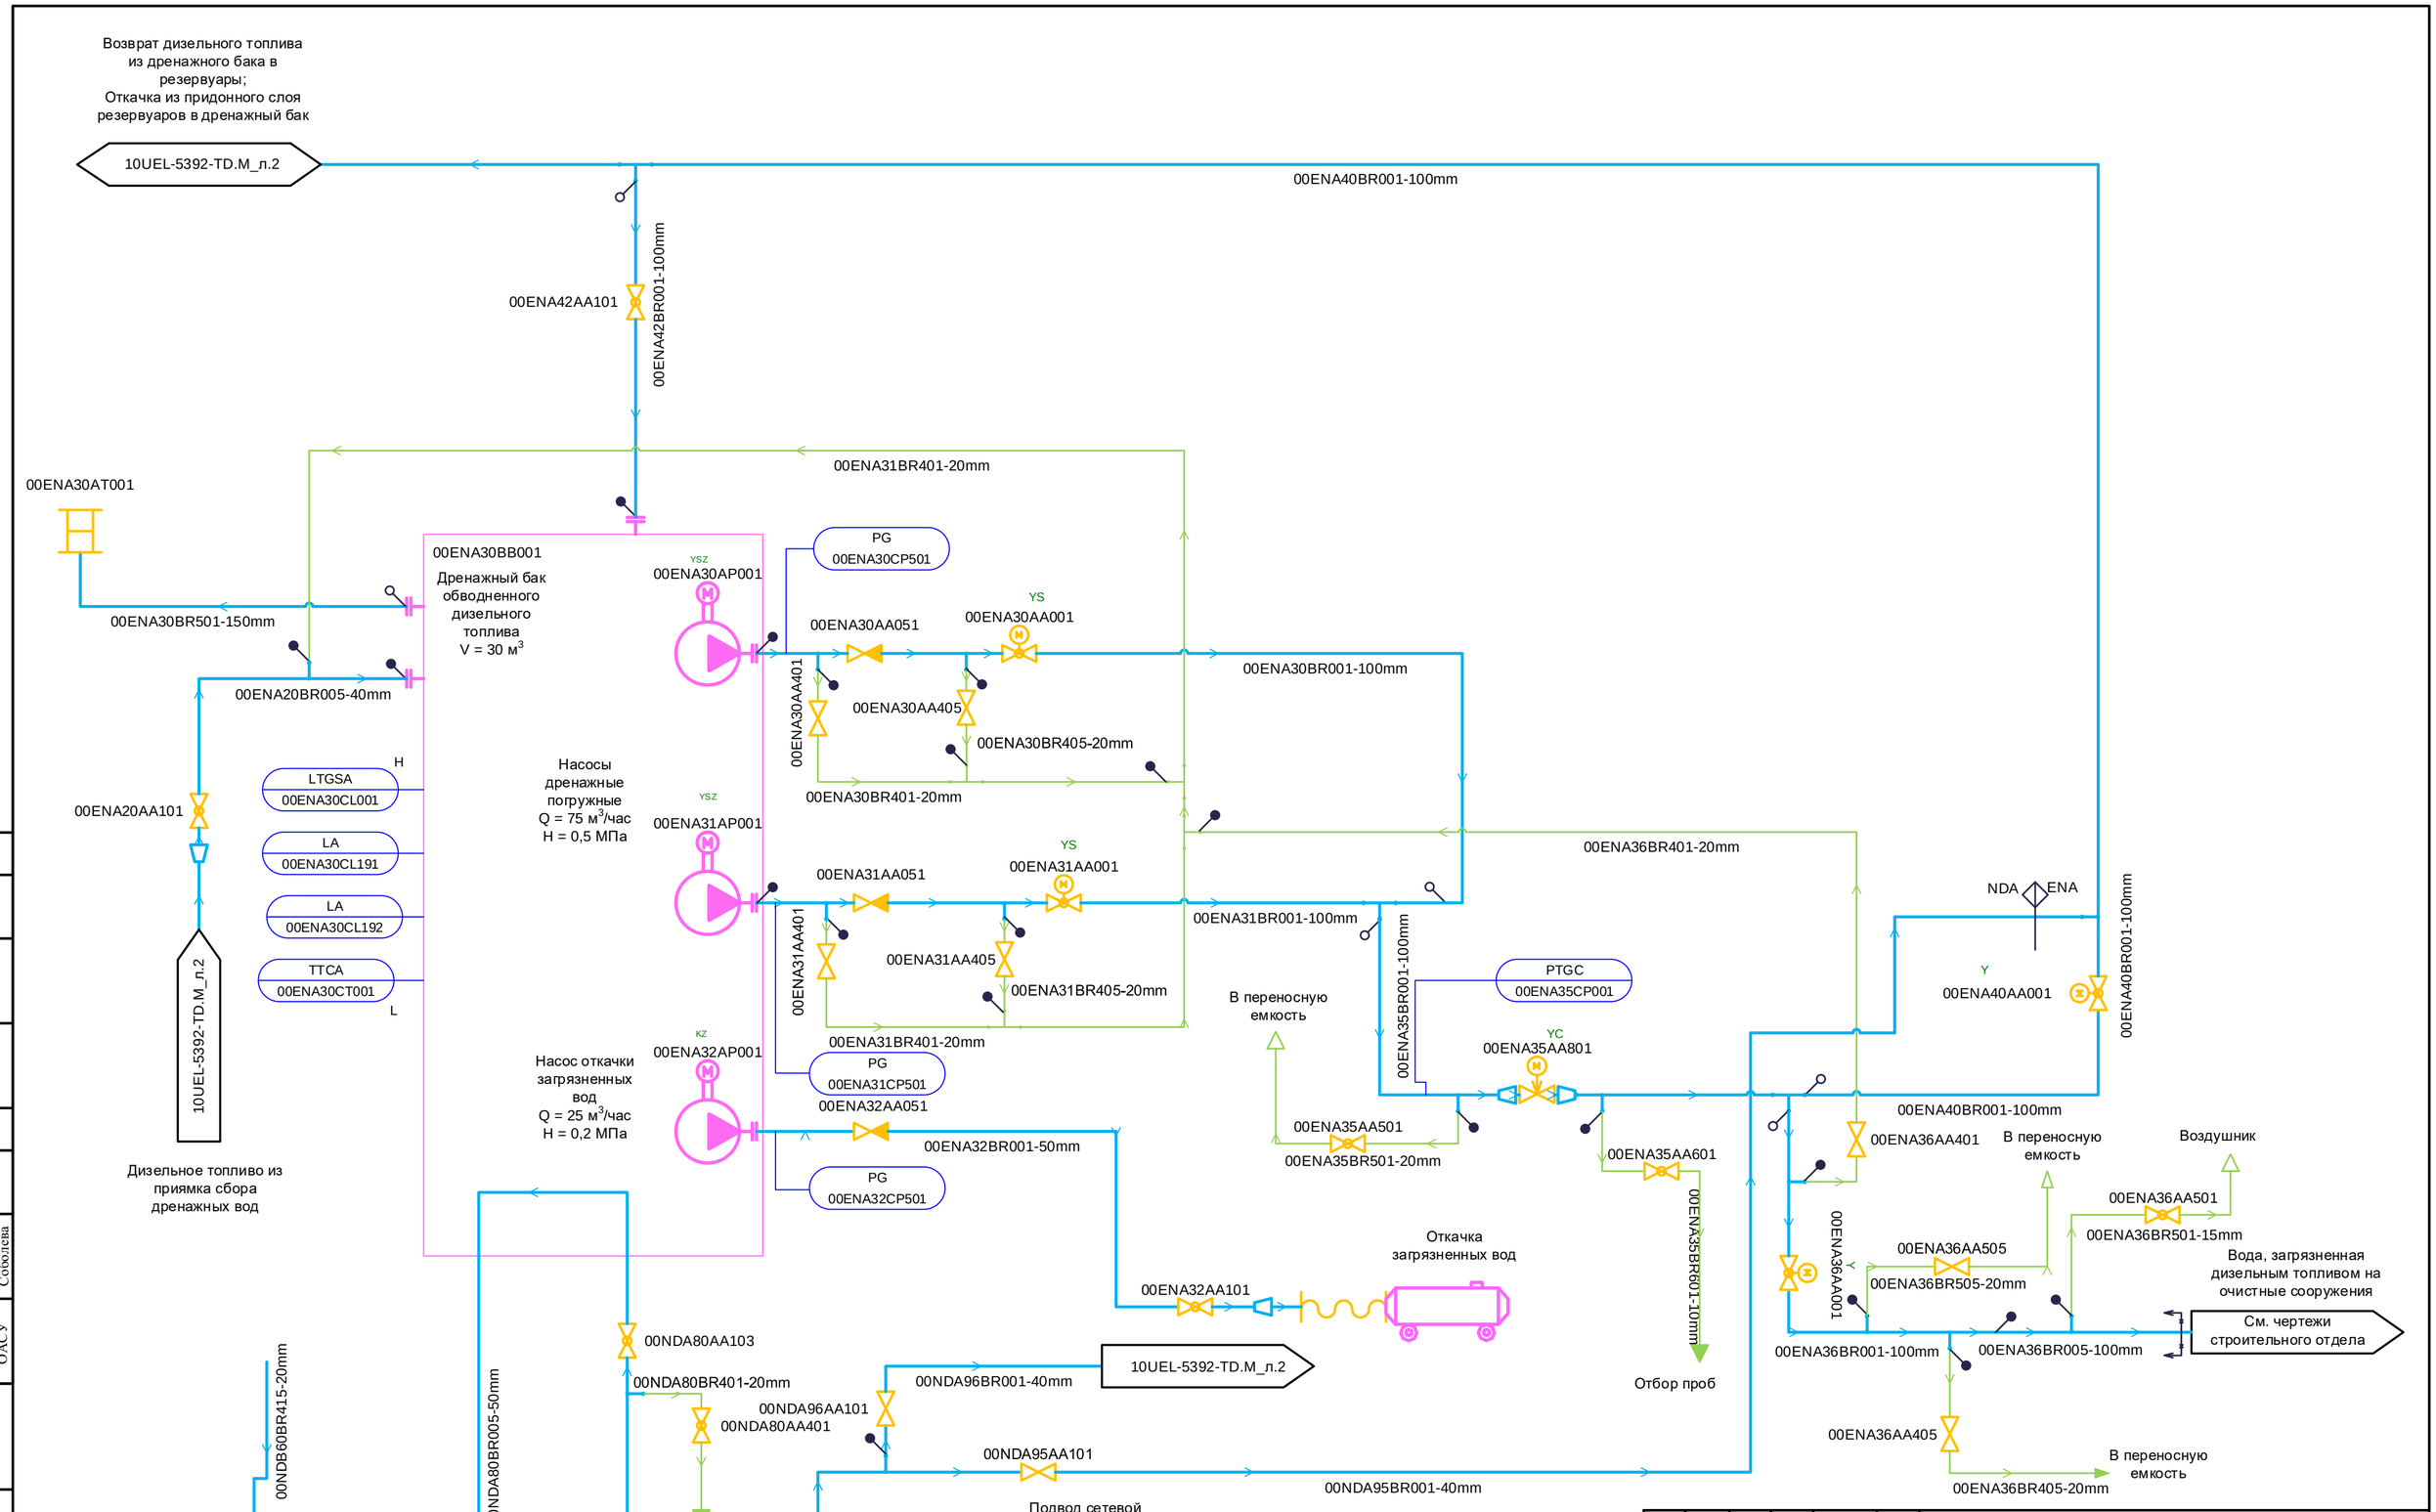

2	-	Зам.	681-16			
Изм.	Кол.уч	Лист	№ док.	Подп.	Дата	
Разработал		Захарова				
Проверил		Попова				
Гл.спец.		Бакатин				
Н. контр.		Черемушкина				

132N32-12UEJ-5395-TD.M

Строительство Сахалинской ГРЭС-2.
Основной производственный комплекс. Внутриплощадочные объекты
(1-ая очередь)

Склад дизтоплива
PI-диаграмма трубопроводов обвязки бака обводненного дизтоплива

Стадия	Лист	Листов
Р	2	

PI-диаграмма трубопроводов обвязки бака обводненного дизтоплива. Система ENA,NDA.

АКЦИОНЕРНОЕ ОБЩЕСТВО ИНСТИТУТ ТЕПЛОЭЛЕКТРОПРОЕКТ Г. МОСКВА

Согласовано
Соболева
ОАСУ
Взам. инв. №
Подпись и дата
Инв. № подл.

Формат А2