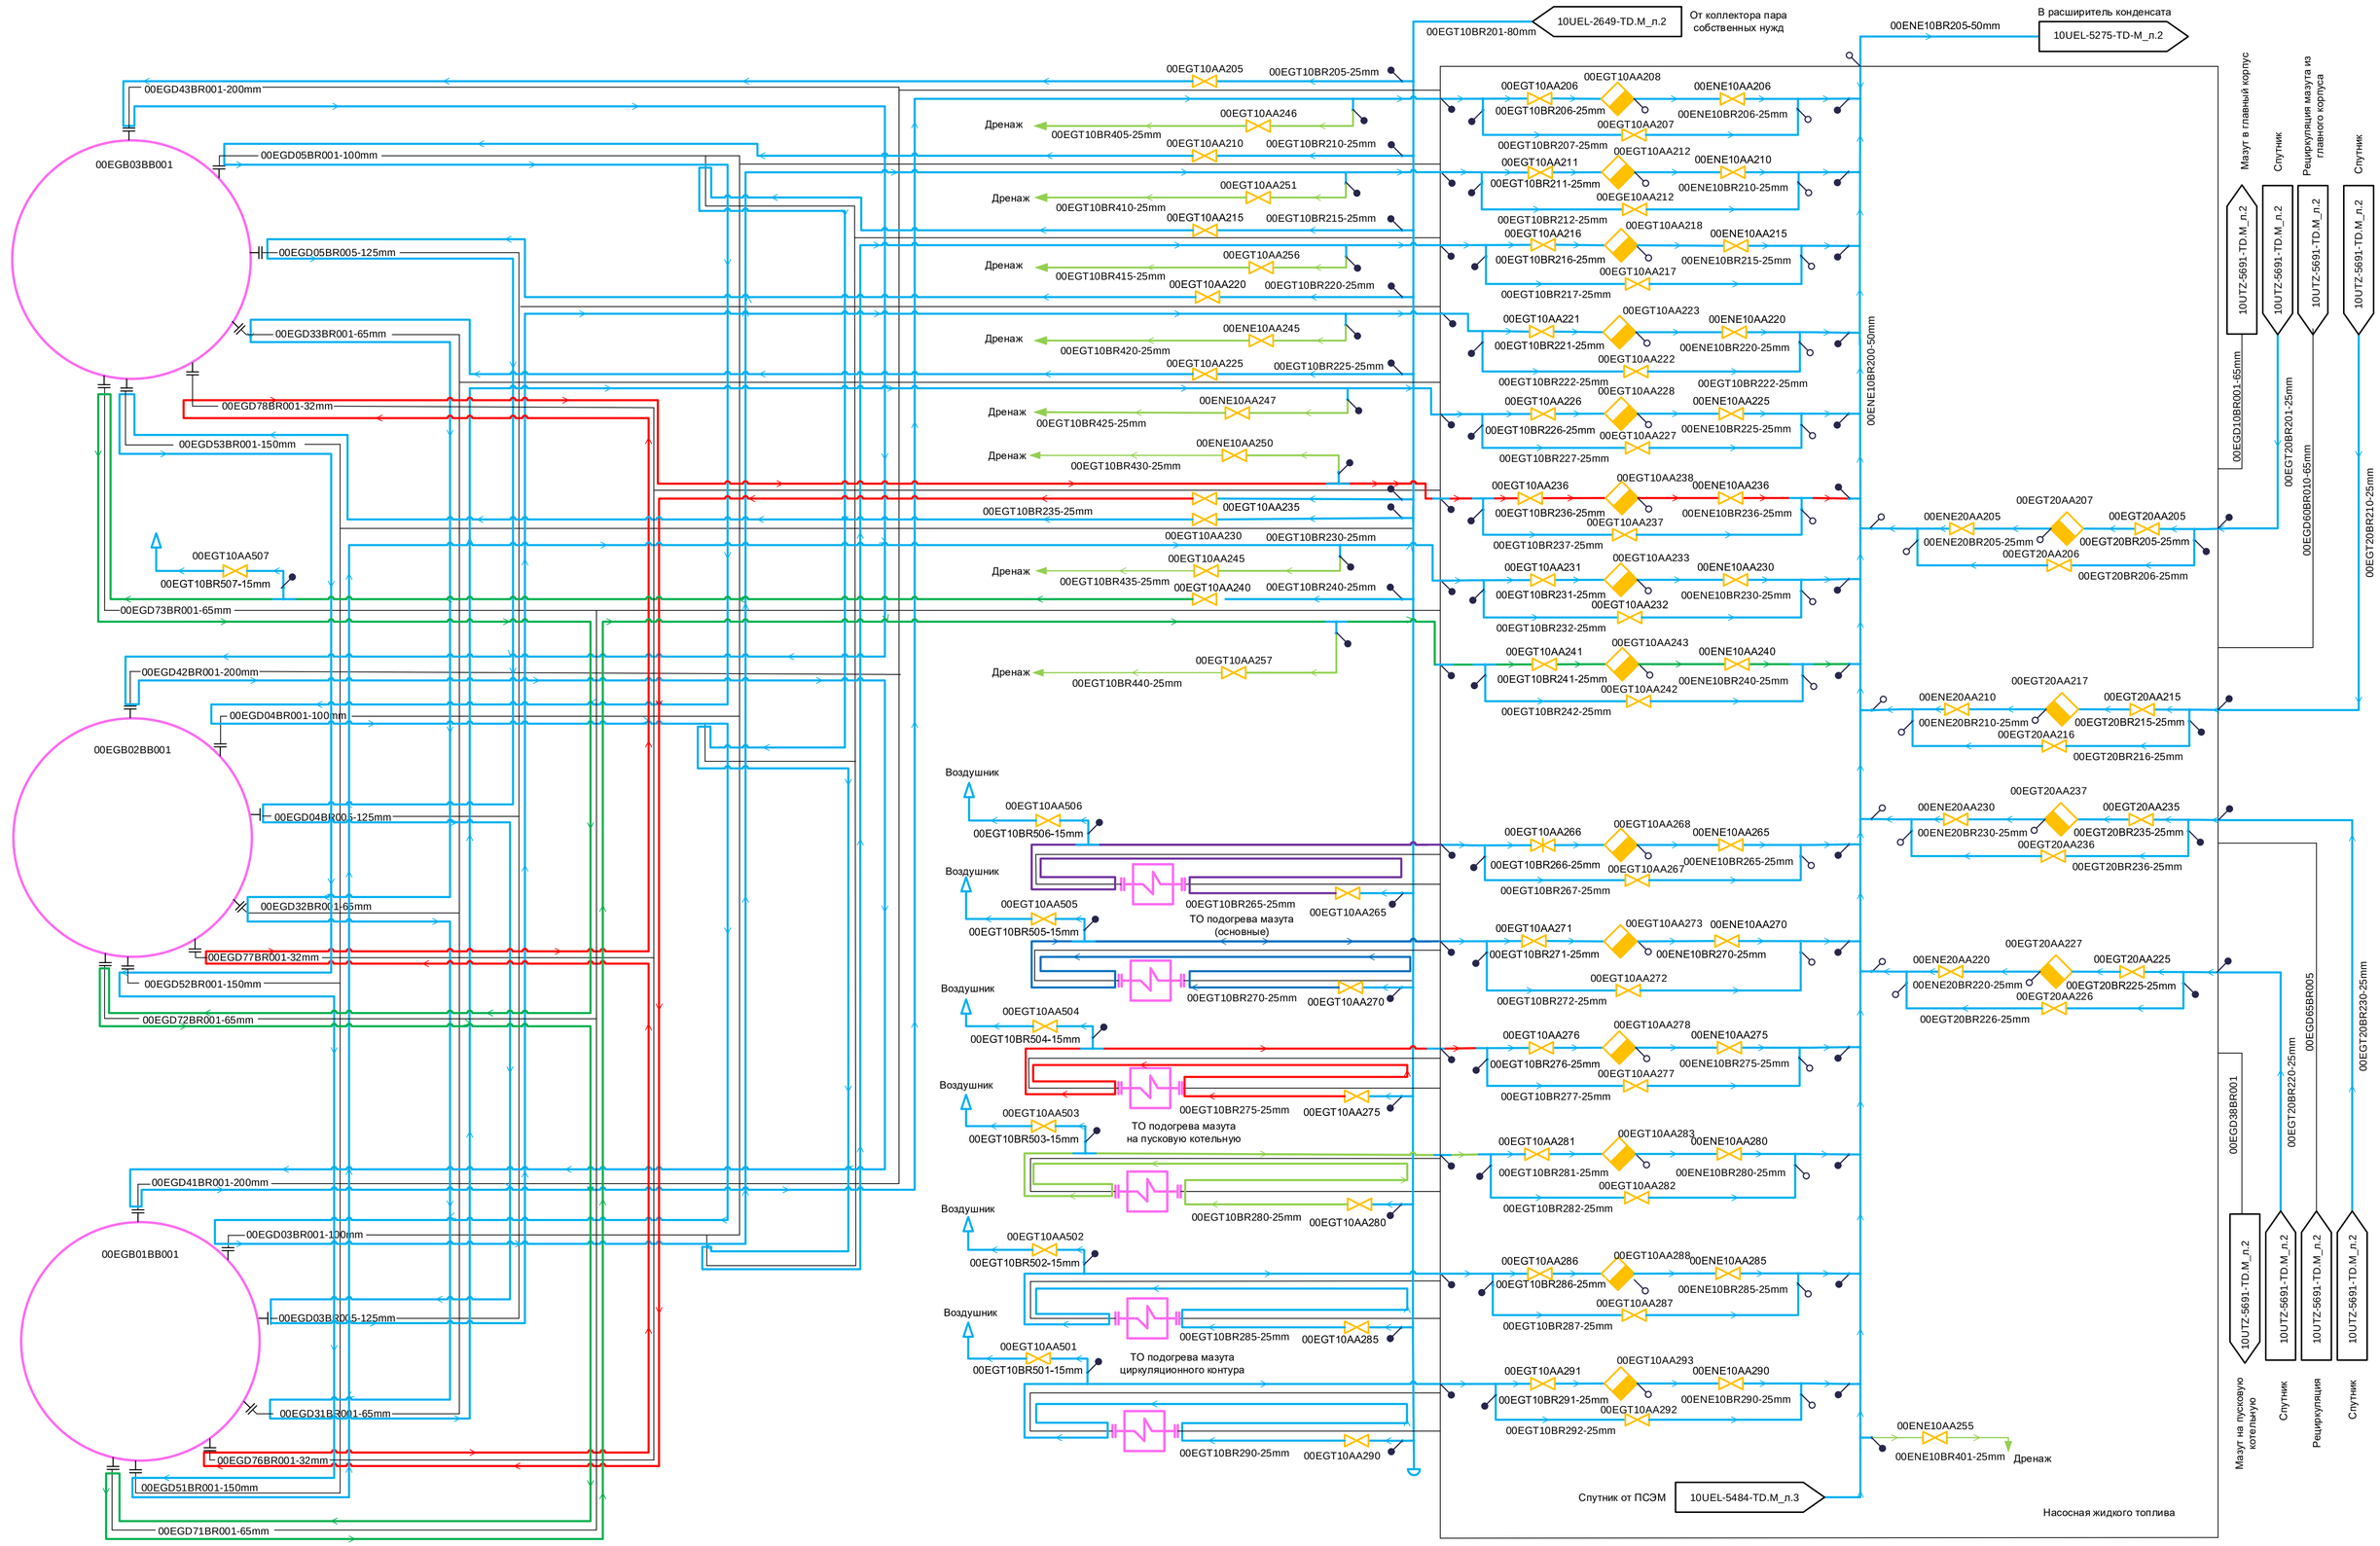

1	-	Зам	261-17			
Изм.	Кол.уч	Лист	№ док.	Подп.	Дата	

132N32 – 10UEL – 5484 – TD.M

Строительство Сахалинской ГРЭС-2. Основной производственный комплекс. Внутриплощадочные объекты (1-ая очередь)

Разработал	Полянская	
Гл.спец.	Сладков	
Н. контр.	Гридчина	

Насосная жидкого топлива. PI-диаграмма паровых спутников мазутопроводов.

PI-диаграмма паровых спутников мазутопроводов. Система EGT

Стадия	Лист	Листов
Р	2	

АКЦИОНЕРНОЕ ОБЩЕСТВО ИНСТИТУТ ТЕПЛОЭЛЕКТРОПРОЕКТ г. МОСКВА

Согласовано

Взам. инв. №

Подпись и дата

Инв. № подл.

Формат А1