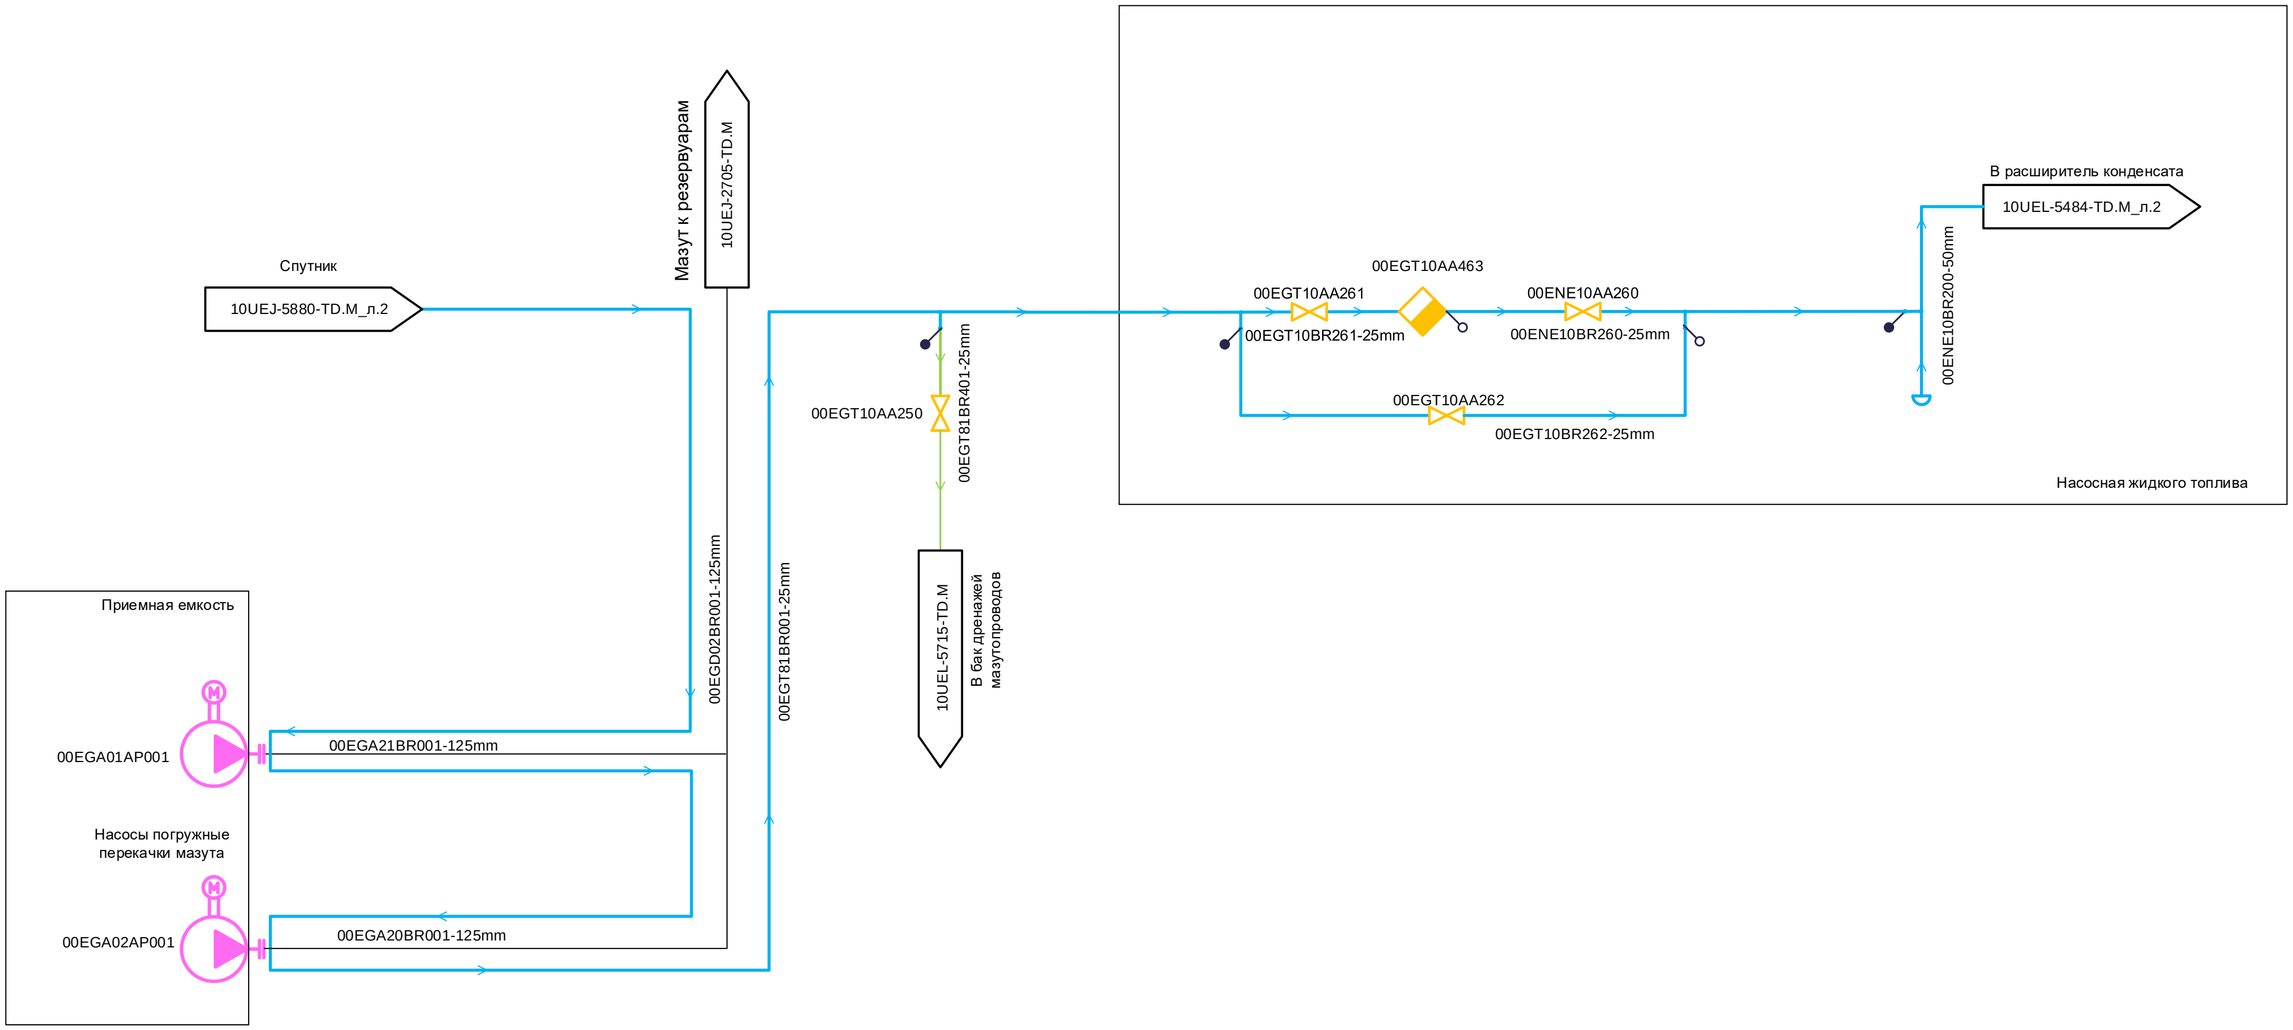

Согласовано

Взам. инв. №

Подпись и дата

Инв. № подл.

1	-	Нов	261-17			
Изм.	Кол.уч	Лист	№ док.	Подп.	Дата	
Разработал		Полянская				
Гл.спец.		Сладков				
Н. контр.		Гридчина				

132N32 – 10UEL – 5484 – TD.M

Строительство Сахалинской ГРЭС-2. Основной производственный комплекс.

Внутриплощадочные объекты (1-ая очередь)

Насосная жидкого топлива.
PI-диаграмма паровых спутников мазутопроводов.

Стадия	Лист	Листов
Р	4	

PI-диаграмма паровых спутников мазутопроводов ПСЭМ. Система EGT

АКЦИОНЕРНОЕ ОБЩЕСТВО ИНСТИТУТ ТЕПЛОЭЛЕКТРОПРОЕКТ Г. МОСКВА

Формат А2