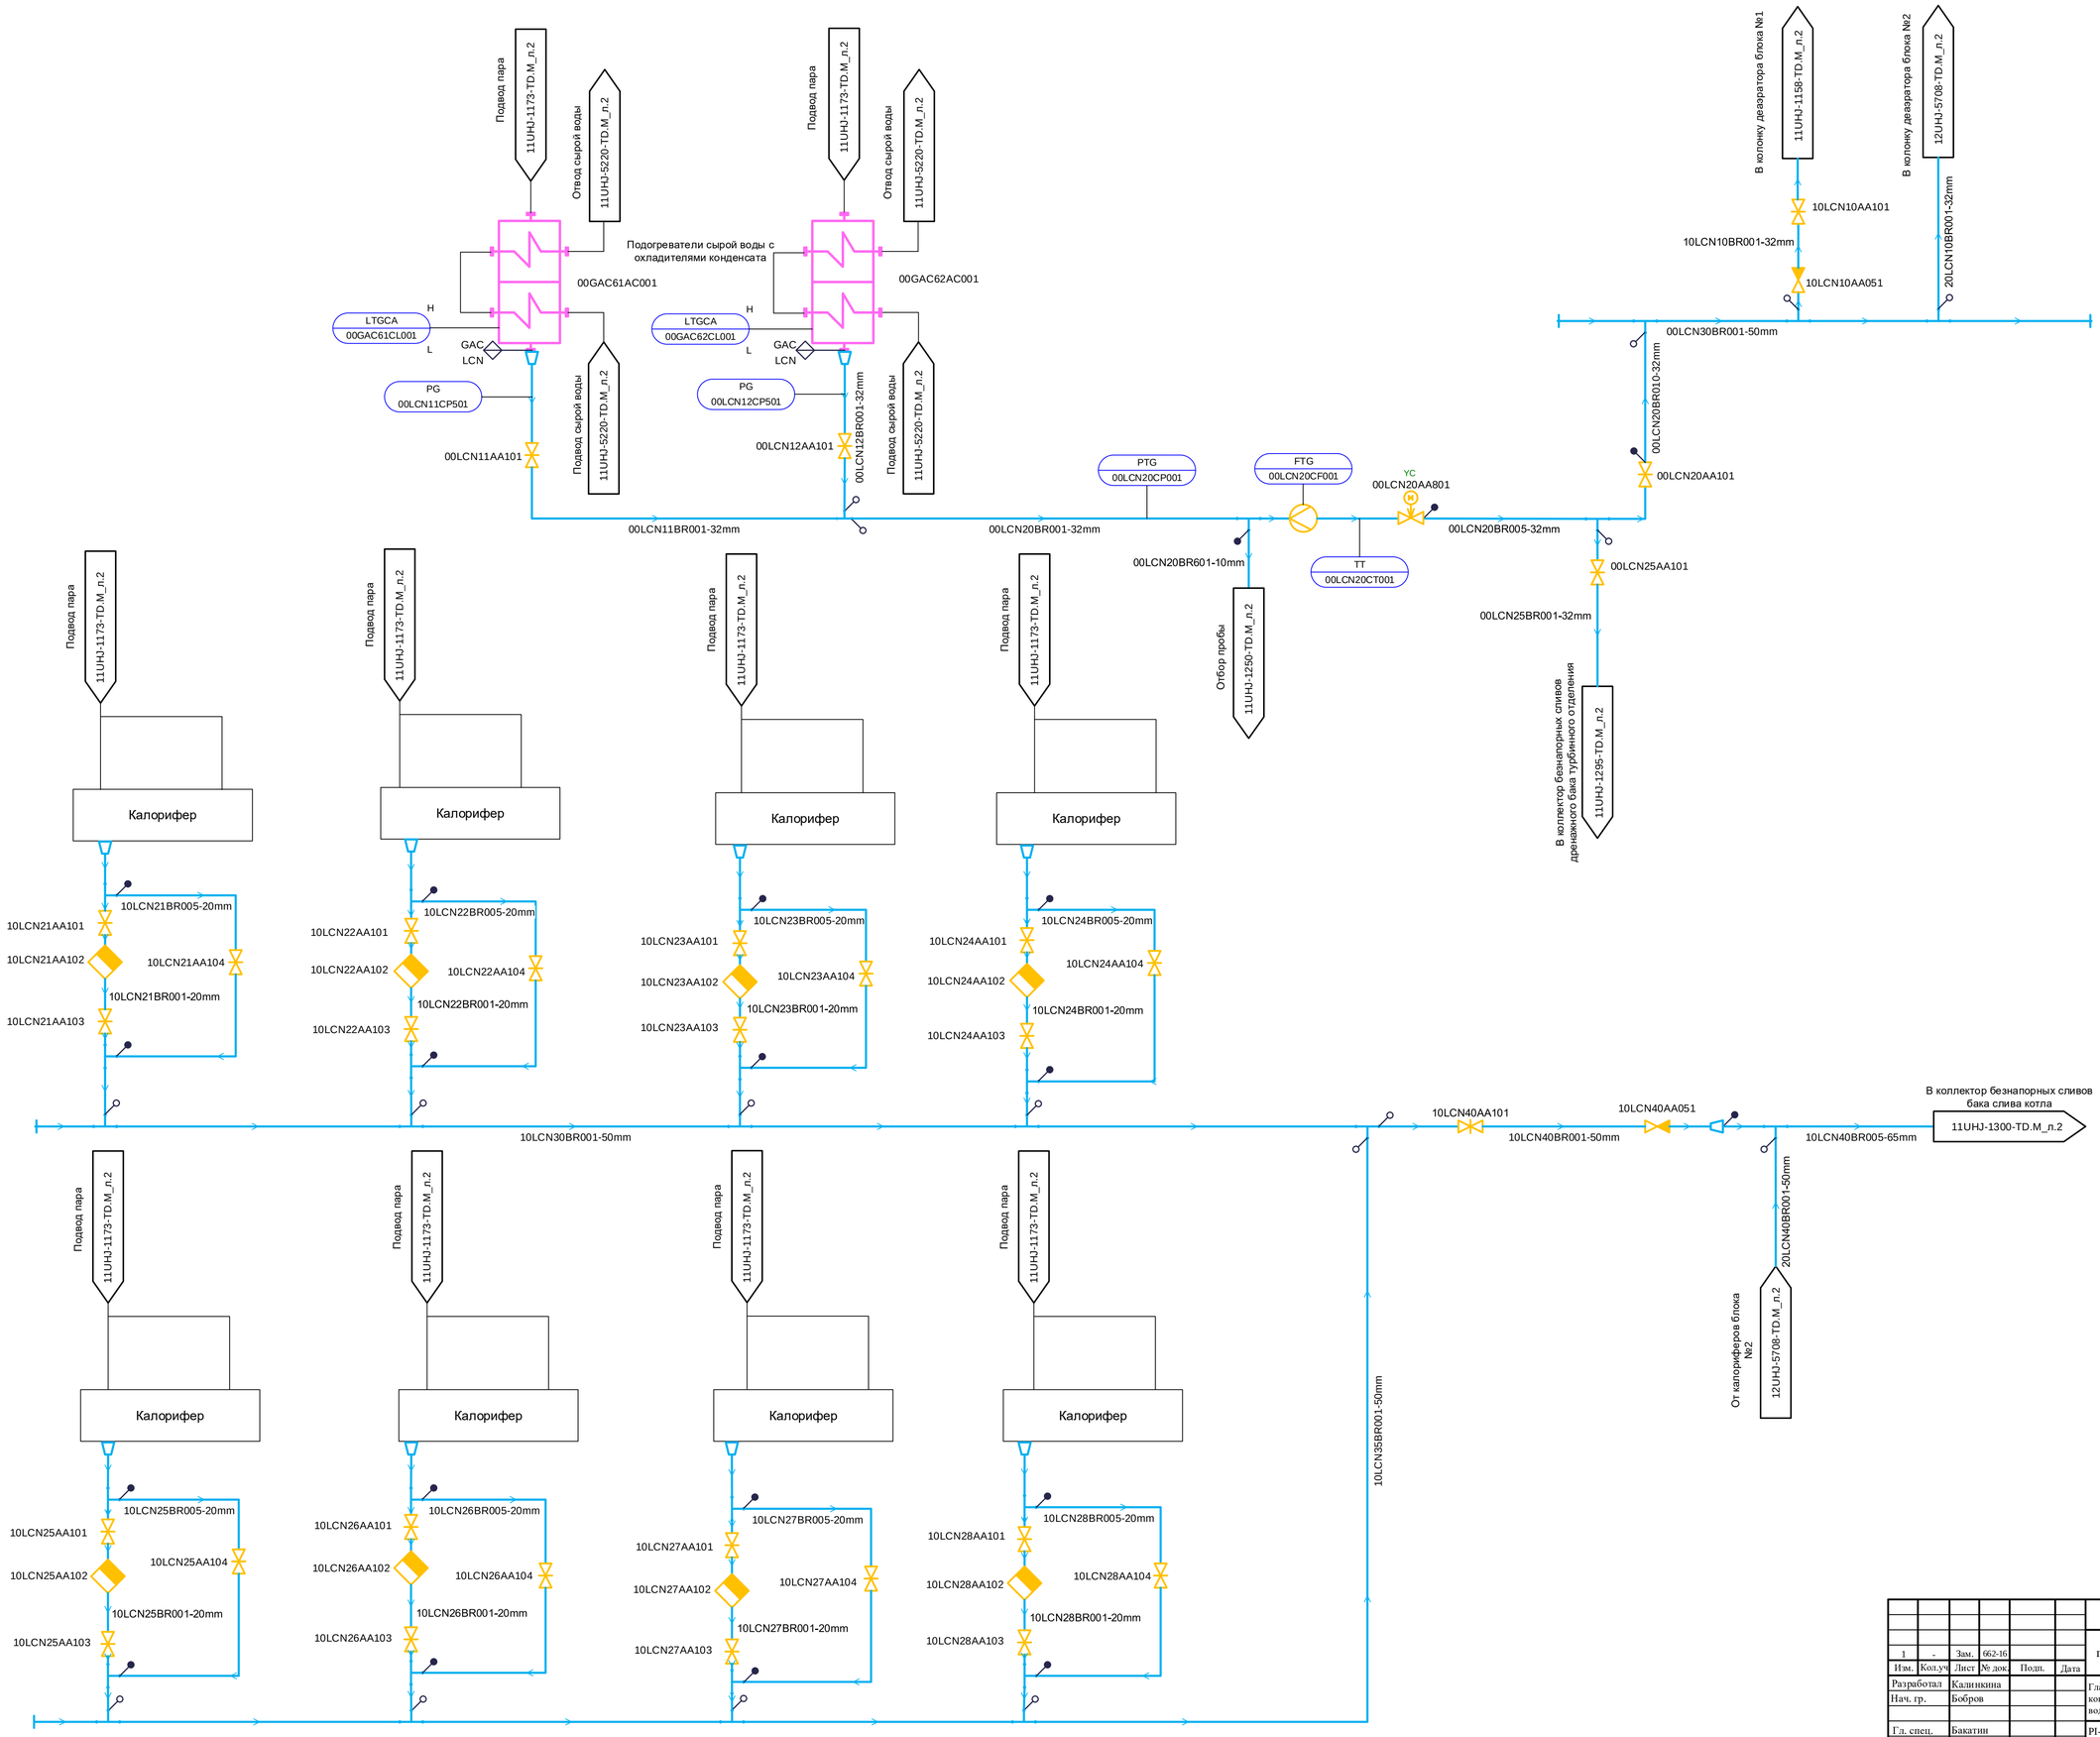

Согласовано

ОАСУ	Соболева

Взам. инв. №

Подпись и дата

Инв. № подл.

1	-	Зам.	662-16			
Изм.	Кол.уч	Лист	№ док.	Подп.	Дата	

132N32 – 11UHJ – 5558 – TD.M

Строительство сахалинской ГРЭС-2. Основной производственный комплекс. Внутриплощадочные объекты (1 очередь)

Разработал	Калинкина	
Нач. гр.	Бобров	
Гл. спец.	Бакатин	
Н. контр.	Гридчина	

Главный корпус. PI-диаграмма трубопроводов конденсата греющего пара подогревателей сырой воды и калориферов котла

PI-диаграмма трубопроводов конденсата греющего пара подогревателей сырой воды и калориферов котла. Система LCN

Стадия	Лист	Листов
Р	2	

АКЦИОНЕРНОЕ ОБЩЕСТВО ИНСТИТУТ ТЕПЛОЭЛЕКТРОПРОЕКТ г. МОСКВА

Формат А1