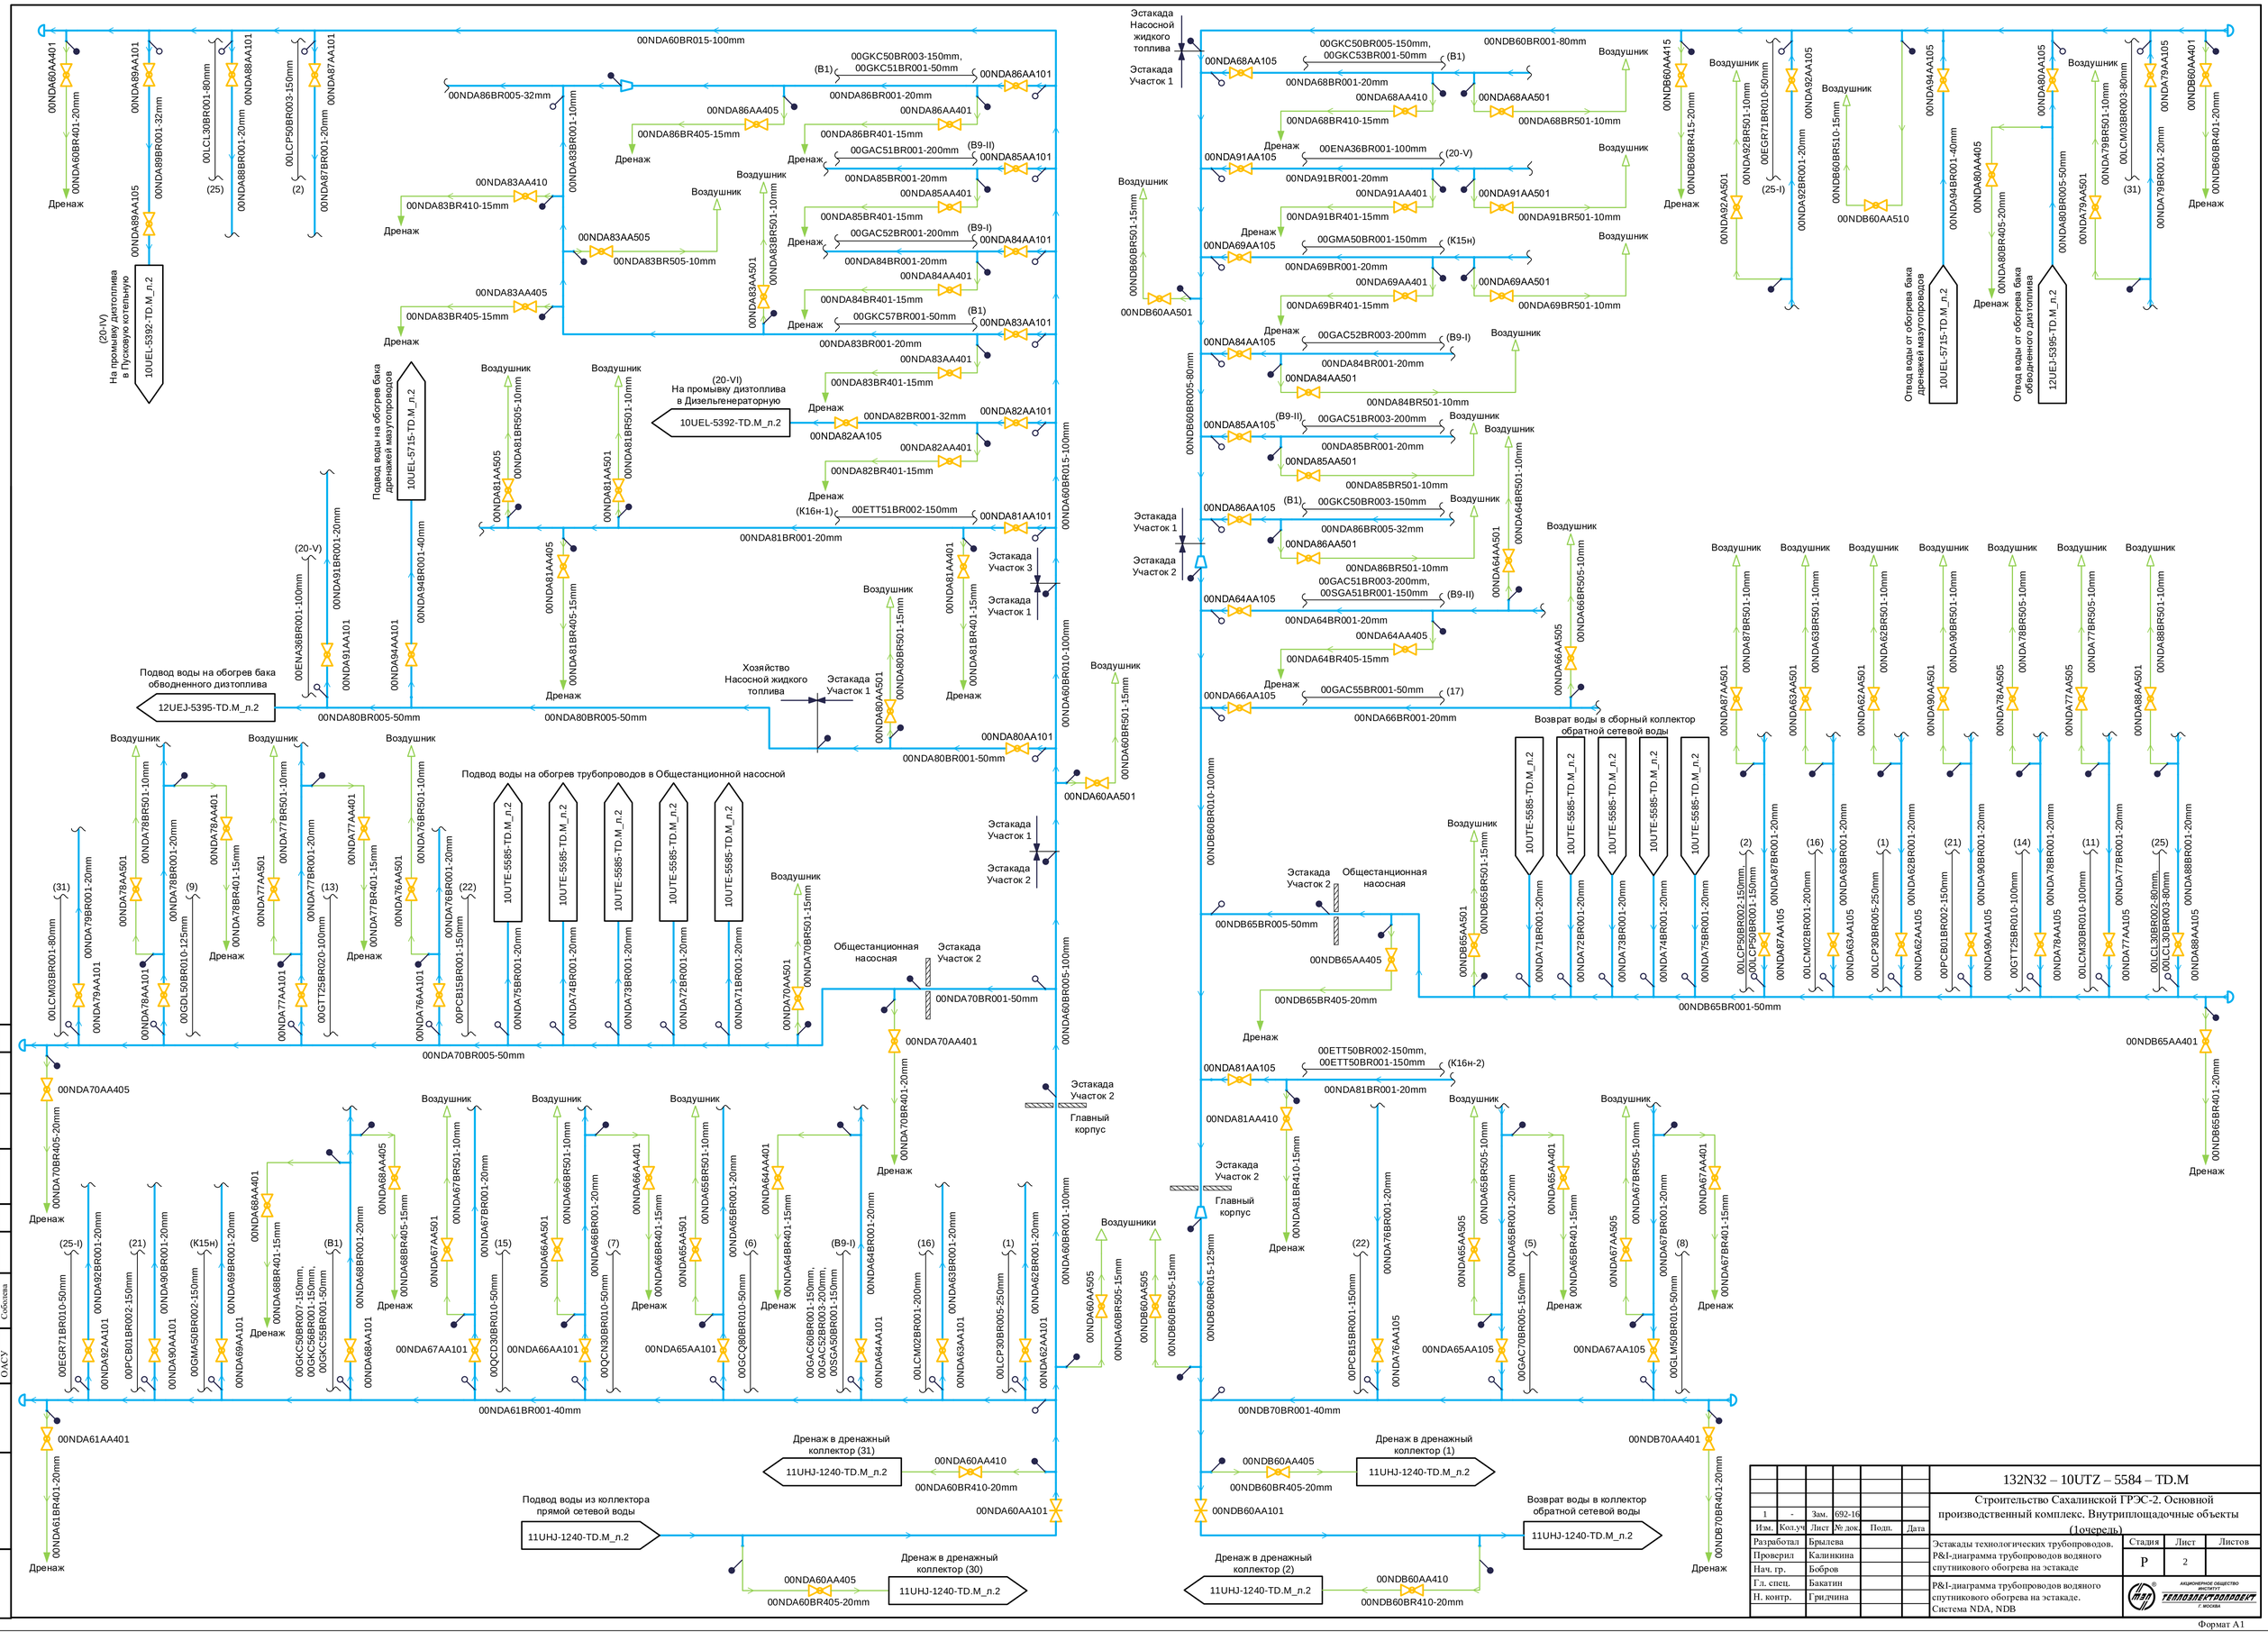

1	-	Зам.	692-16			
Изм.	Кол.уч	Лист	№ док.	Подп.	Дата	
Разработал		Брылева				
Проверил		Калинкина				
Нач. гр.		Бобров				
Гл. спец.		Бакатин				
Н. контр.		Гридчина				

132N32 – 10UTZ – 5584 – TD.M

Строительство Сахалинской ГРЭС-2. Основной производственный комплекс. Внутриплощадочные объекты (1очередь)

Эстакады технологических трубопроводов. P&I-диаграмма трубопроводов водяного спутникового обогрева на эстакаде

P&I-диаграмма трубопроводов водяного спутникового обогрева на эстакаде. Система NDA, NDB

Стадия	Лист	Листов
Р	2	

АКЦИОНЕРНОЕ ОБЩЕСТВО ИНСТИТУТ ТЕПЛОЭЛЕКТРОПРОЕКТ г. МОСКВА

Согласовано

ОАСУ Соболева

Взам. инв. №

Подпись и дата

Инв. № подл.

Формат А1