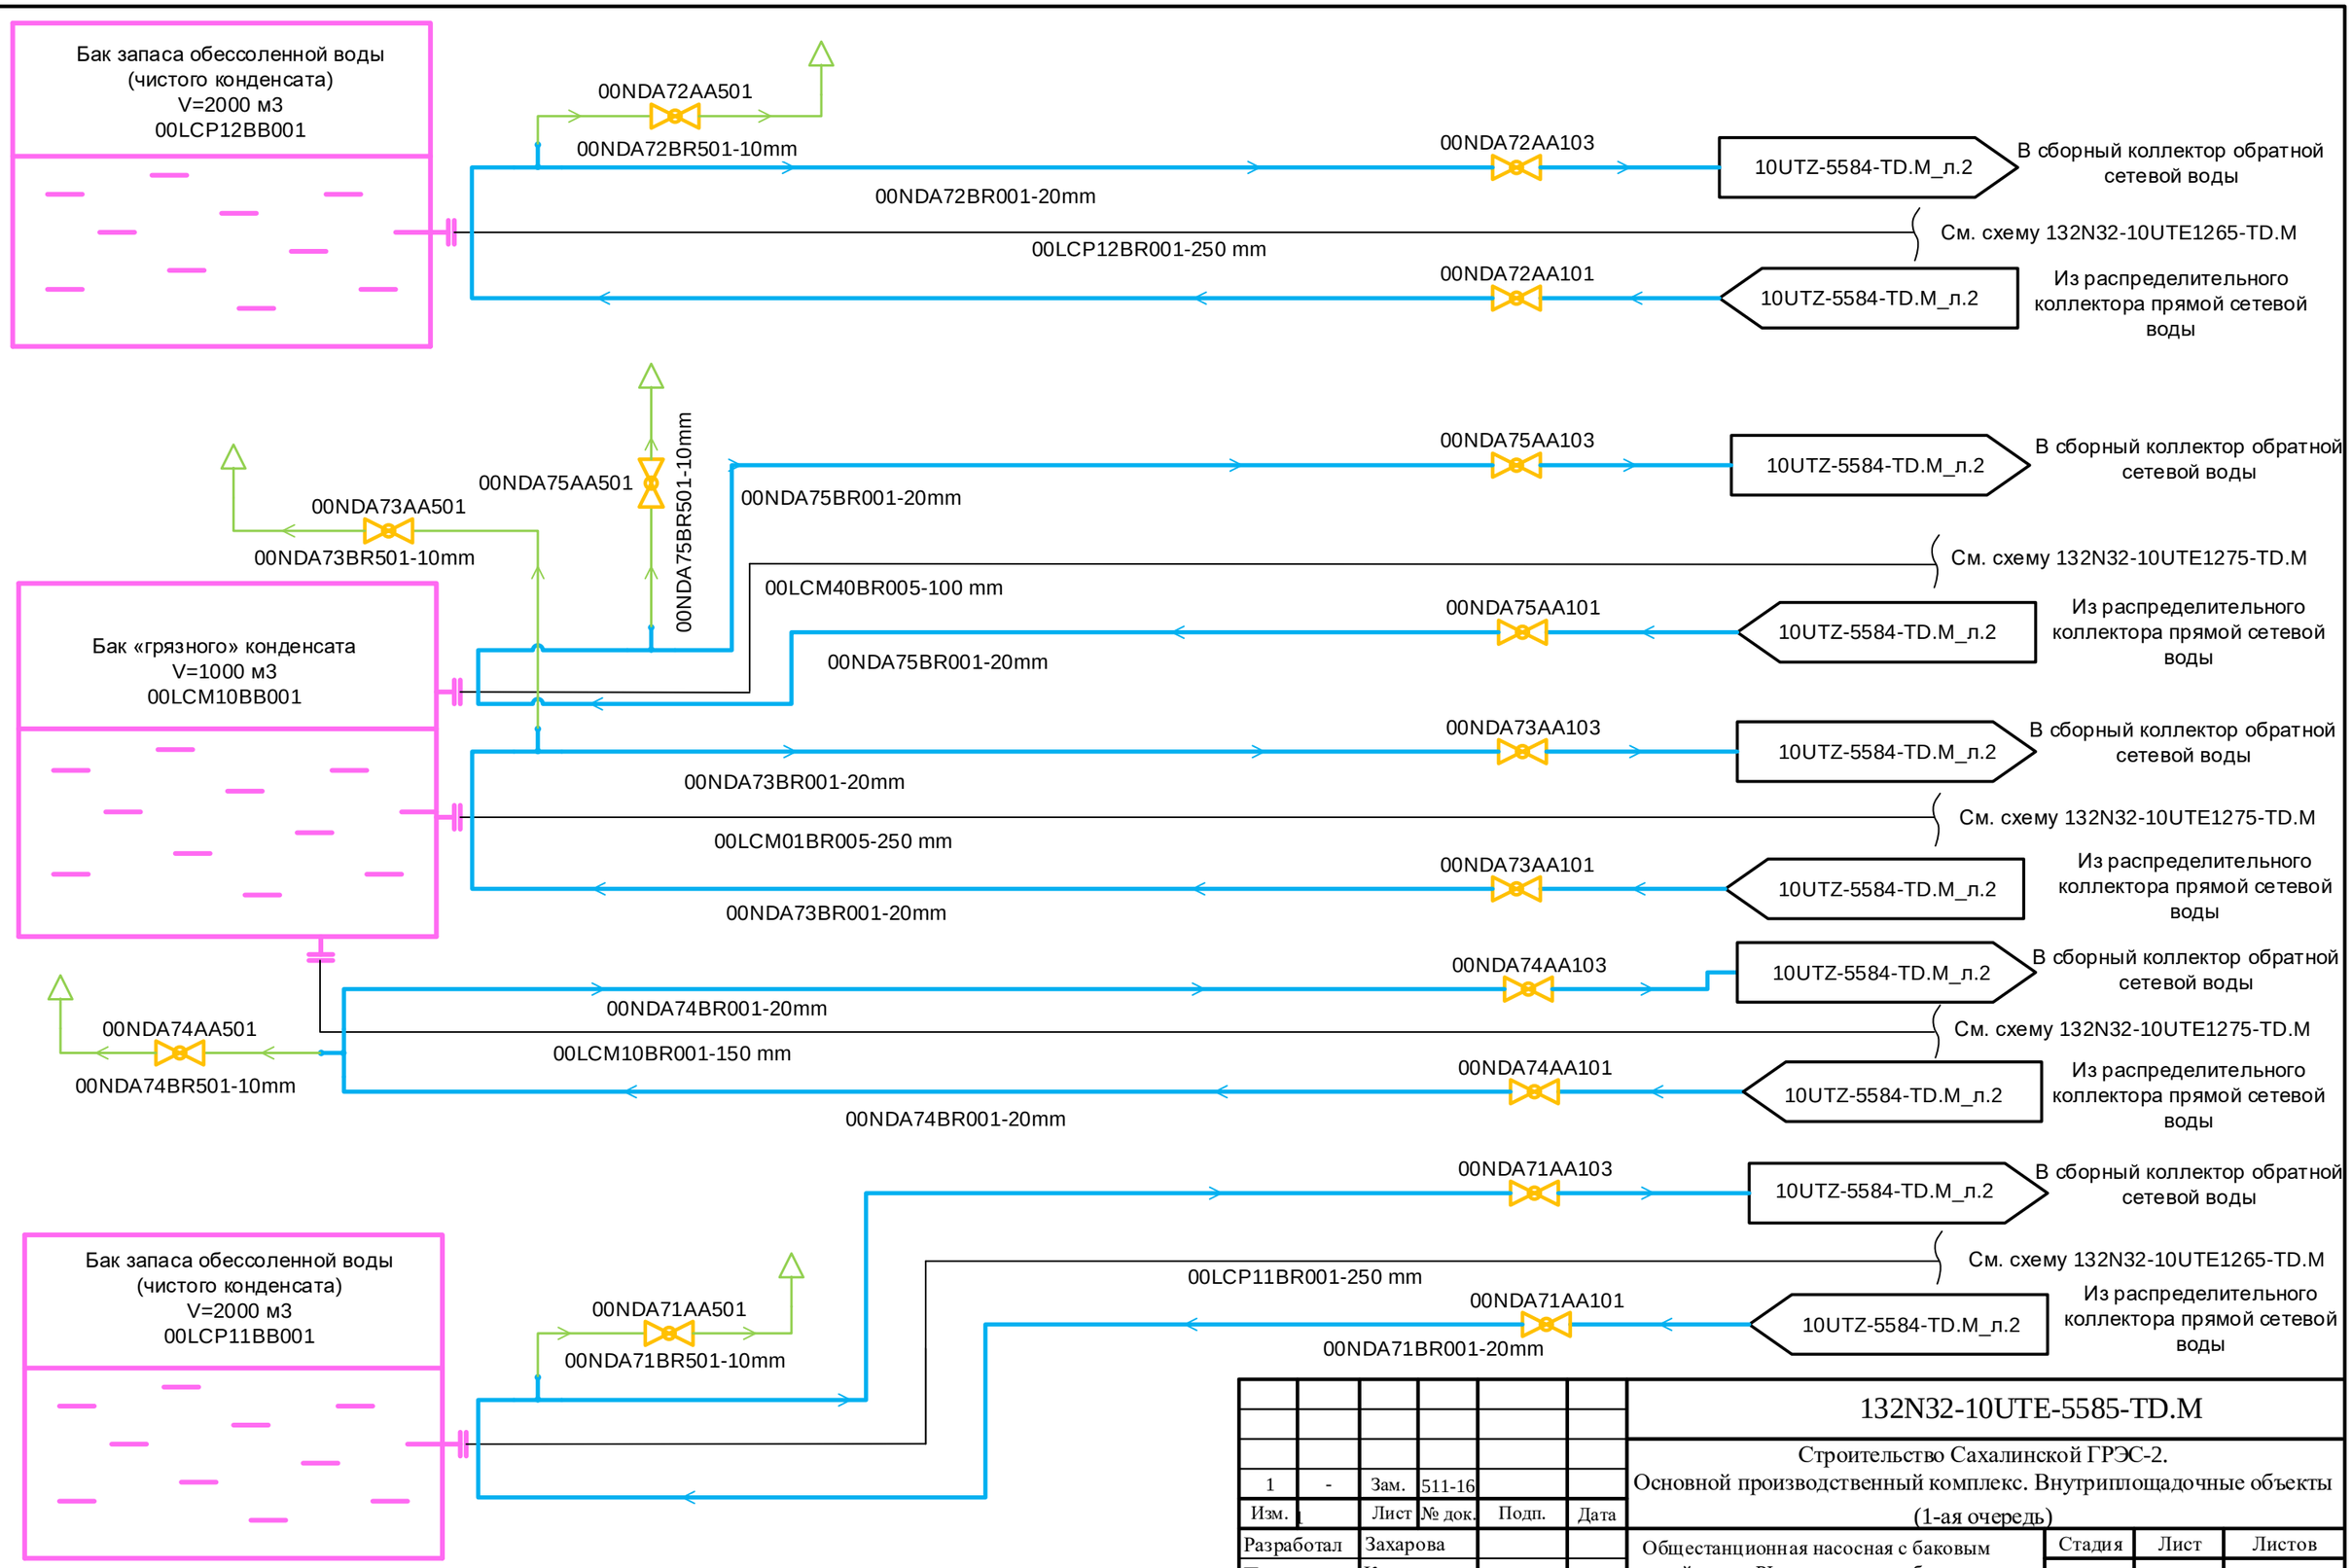

						132N32-10UTE-5585-TD.M		
						Строительство Сахалинской ГРЭС-2. Основной производственный комплекс. Внутриплощадочные объекты (1-ая очередь)		
1	-	Зам.	511-16					
Изм.		Лист	№ док.	Подп.	Дата			
Разработал		Захарова				Общестанционная насосная с баковым хозяйством. PI-диаграмма трубопроводов водяного спутникового обогрева	Стадия	Лист	Листов
Проверил		Калинкина					Р	2	
Гл.спец.		Бакатин							
						PI-диаграмма трубопроводов водяного спутникового обогрева. Система NDA	АКЦИОНЕРНОЕ ОБЩЕСТВО ИНСТИТУТ ТЕПЛОЭЛЕКТРОПРОЕКТ Г. МОСКВА		
Н. контр.		Черемушкина							

Согласовано

Соболева

ОАСУ

Взам. инв. №

Подпись и дата

Инв. № подл.

Формат А3