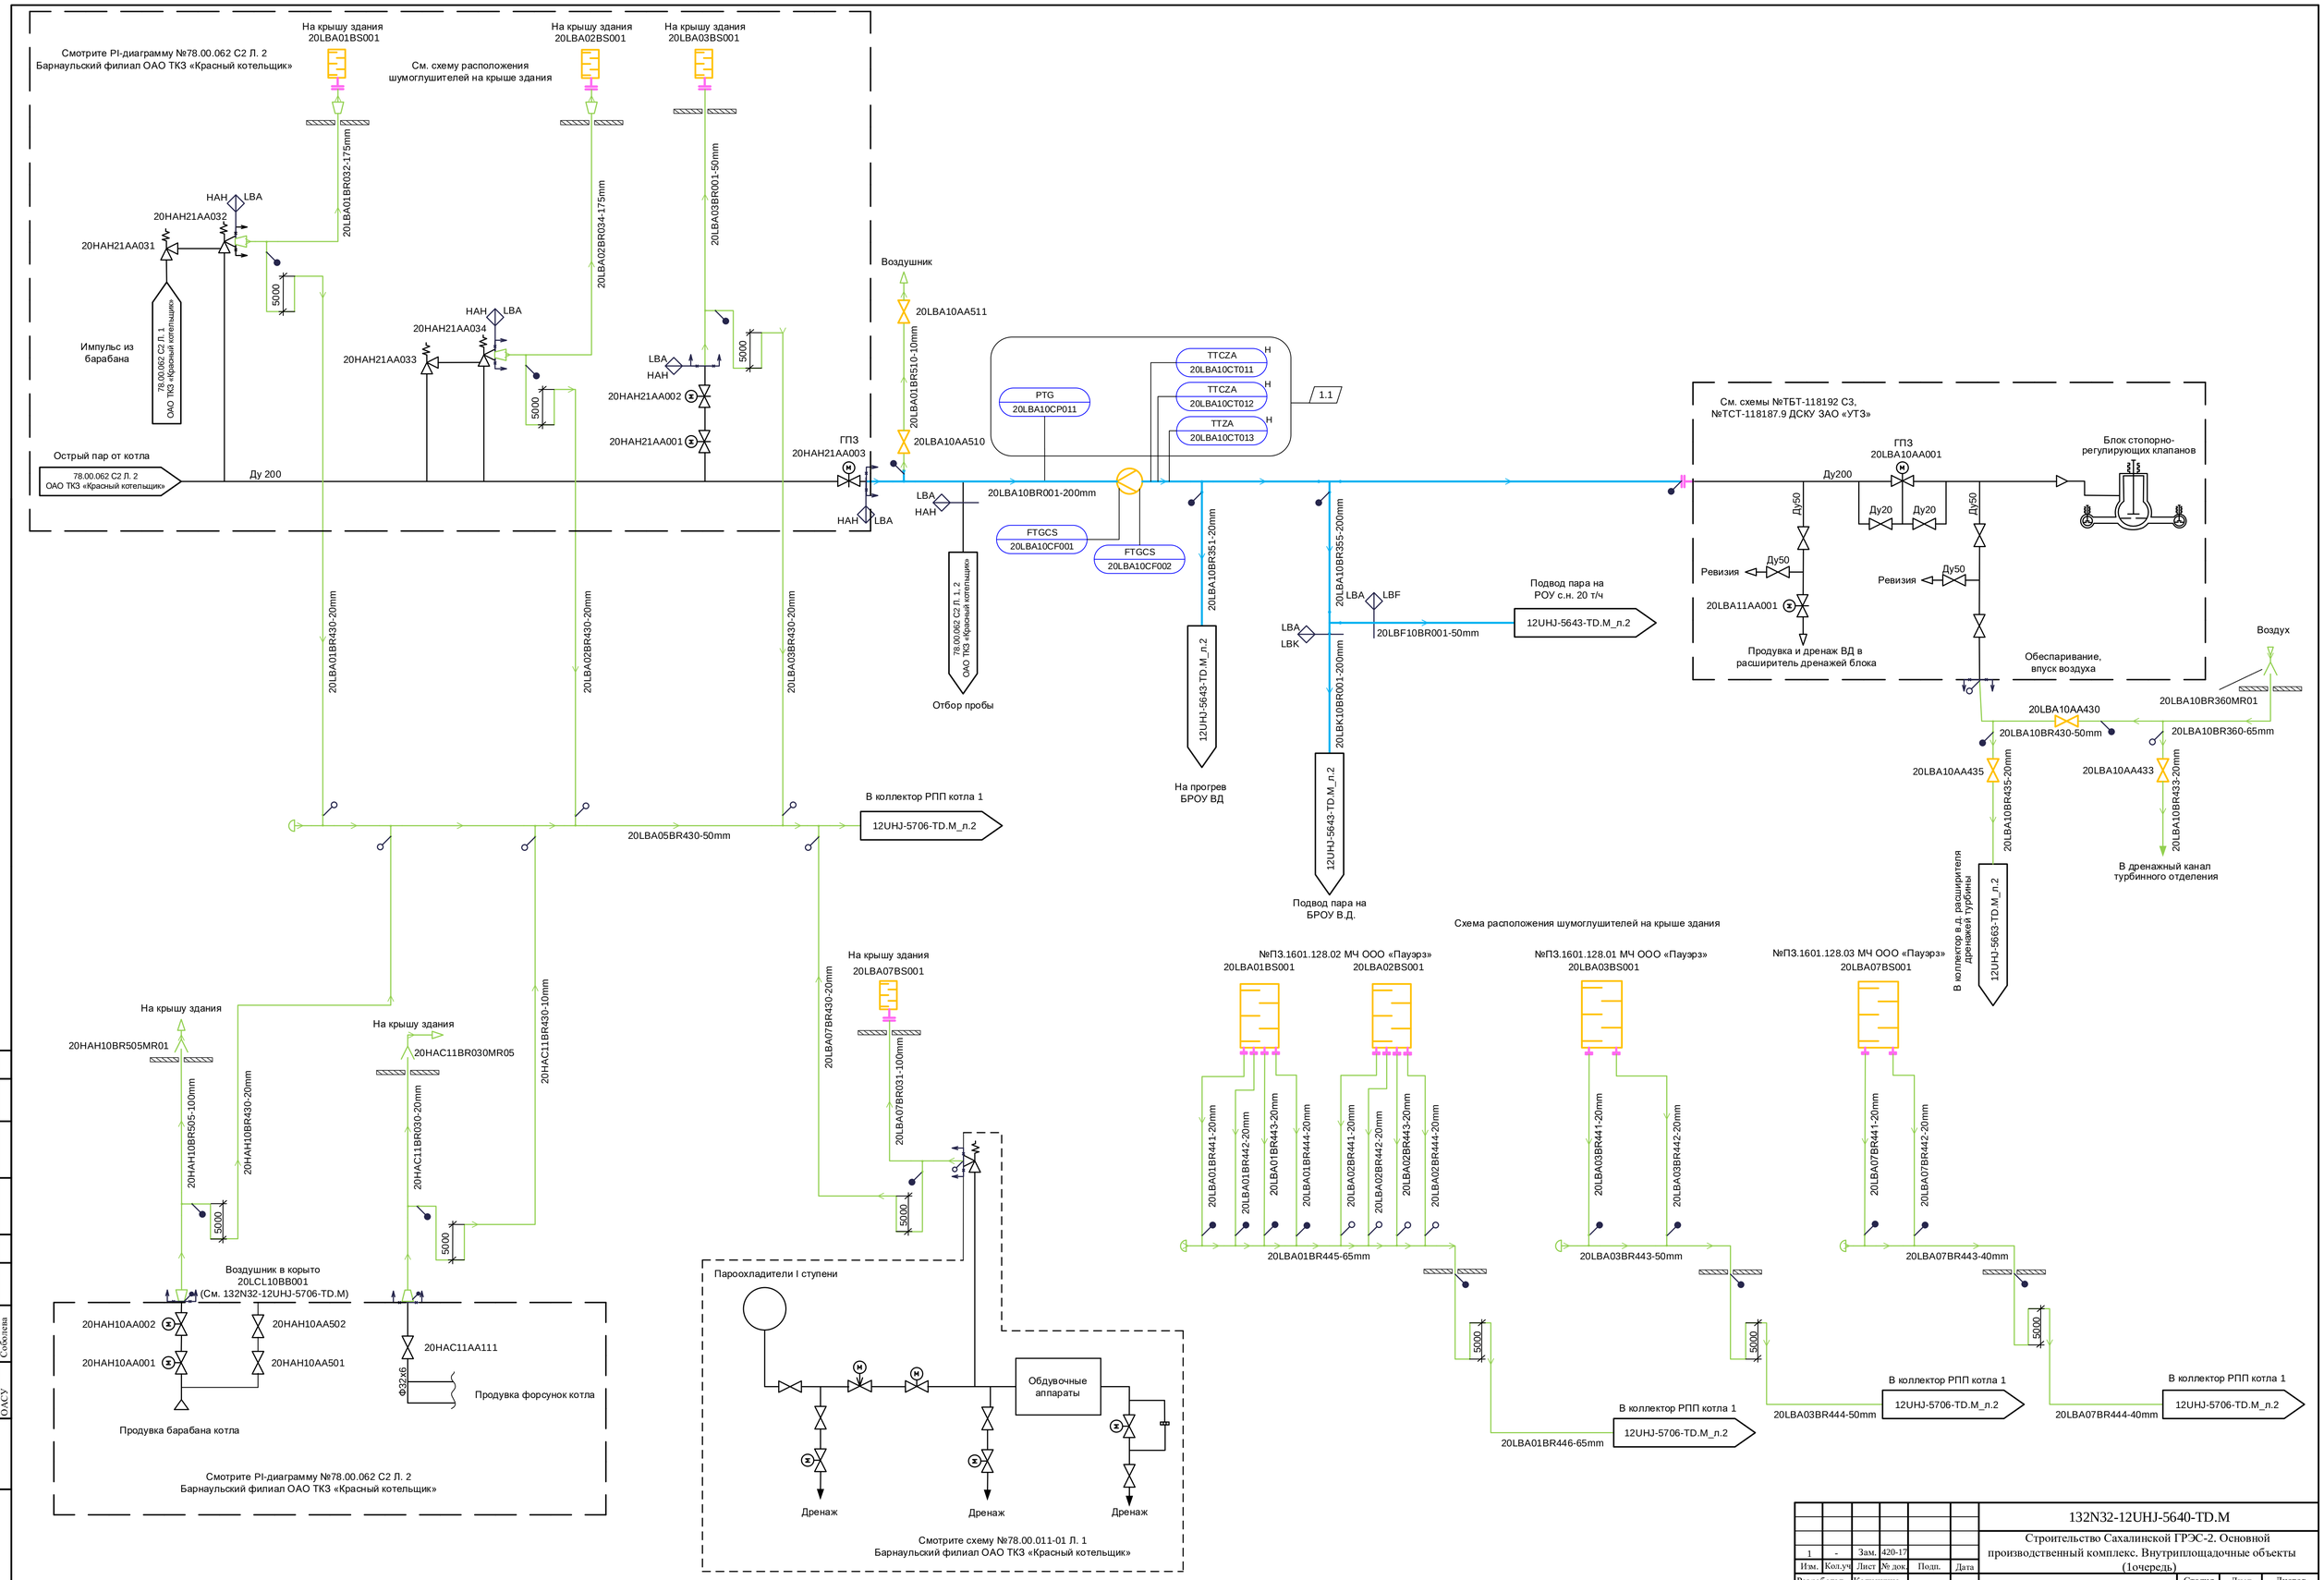

1	-	Зам.	420-17			132N32-12UHJ-5640-TD.M		
Изм.	Кол.уч	Лист	№ док.	Подп.	Дата	Строительство Сахалинской ГРЭС-2. Основной производственный комплекс. Внутриплощадочные объекты (1очередь)		
Разработал		Калинкина				Главный корпус. PI-диаграмма трубопроводов острого пара	Стадия	Лист	Листов
Гл. спец.		Сладков					Р	2	
Н. контр.		Гридчина				PI-диаграмма трубопроводов острого пара. Система LBA	АКЦИОНЕРНОЕ ОБЩЕСТВО «ВТИ» ТЕПЛОЭЛЕКТРОПРОЕКТ Г. МОСКВА	

Согласовано
ОАСУ Соболева
Взам. инв. №
Подпись и дата
Инв. № подл.

Формат А1