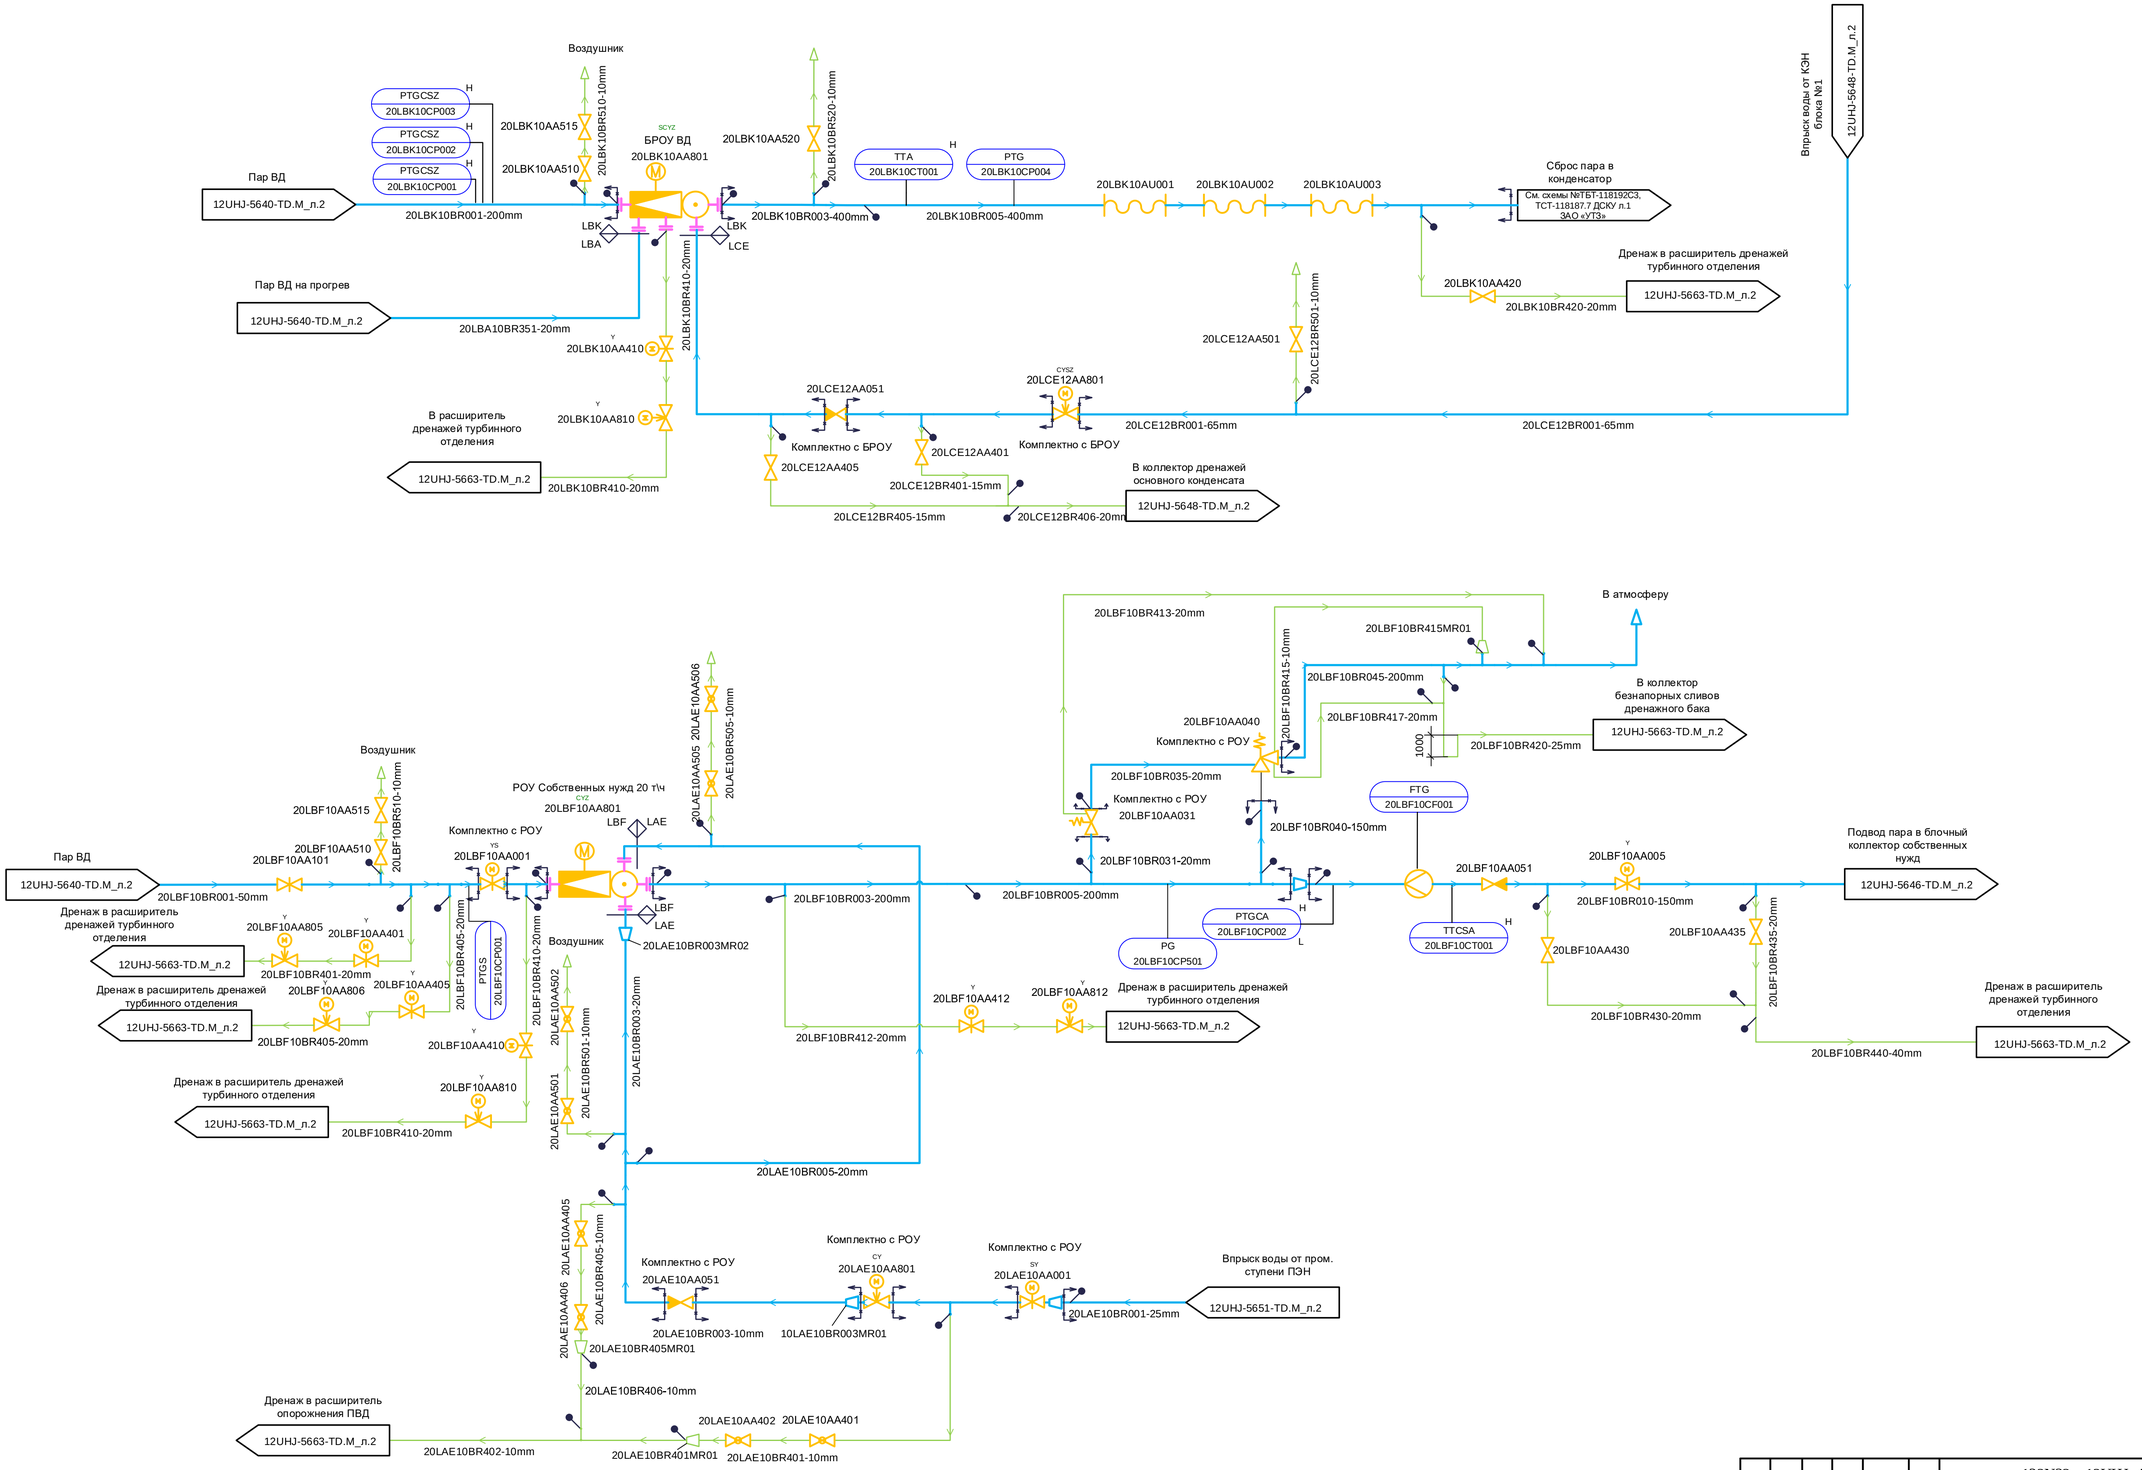

Изм.	Кол.уч	Лист	№ док.	Подп.	Дата	132N32 – 12UHJ –5643 – TD.M
						Строительство Сахалинской ГРЭС-2. Основной производственный комплекс. Внутриплощадочные объекты (1-ая очередь)
Разработал		Захарова				Главный корпус. Блок № 2 PI-диаграмма трубопроводов БРОУ и РОУ
Проверил		Калинкина				
Гл.спец.		Бакатин				
Н. контр.		Черемушкина				PI-диаграмма трубопроводов БРОУ и РОУ. Система LBK, LBF, LCE, LAE

Стадия	Лист	Листов
Р	2	

АКЦИОНЕРНОЕ ОБЩЕСТВО ВНИПИ ТЕПЛОЭЛЕКТРОПРОЕКТ г. Москва

Формат А1

Согласовано

ОАСУ | Соболева

Взам. инв. №

Подпись и дата

Инв. № подл.