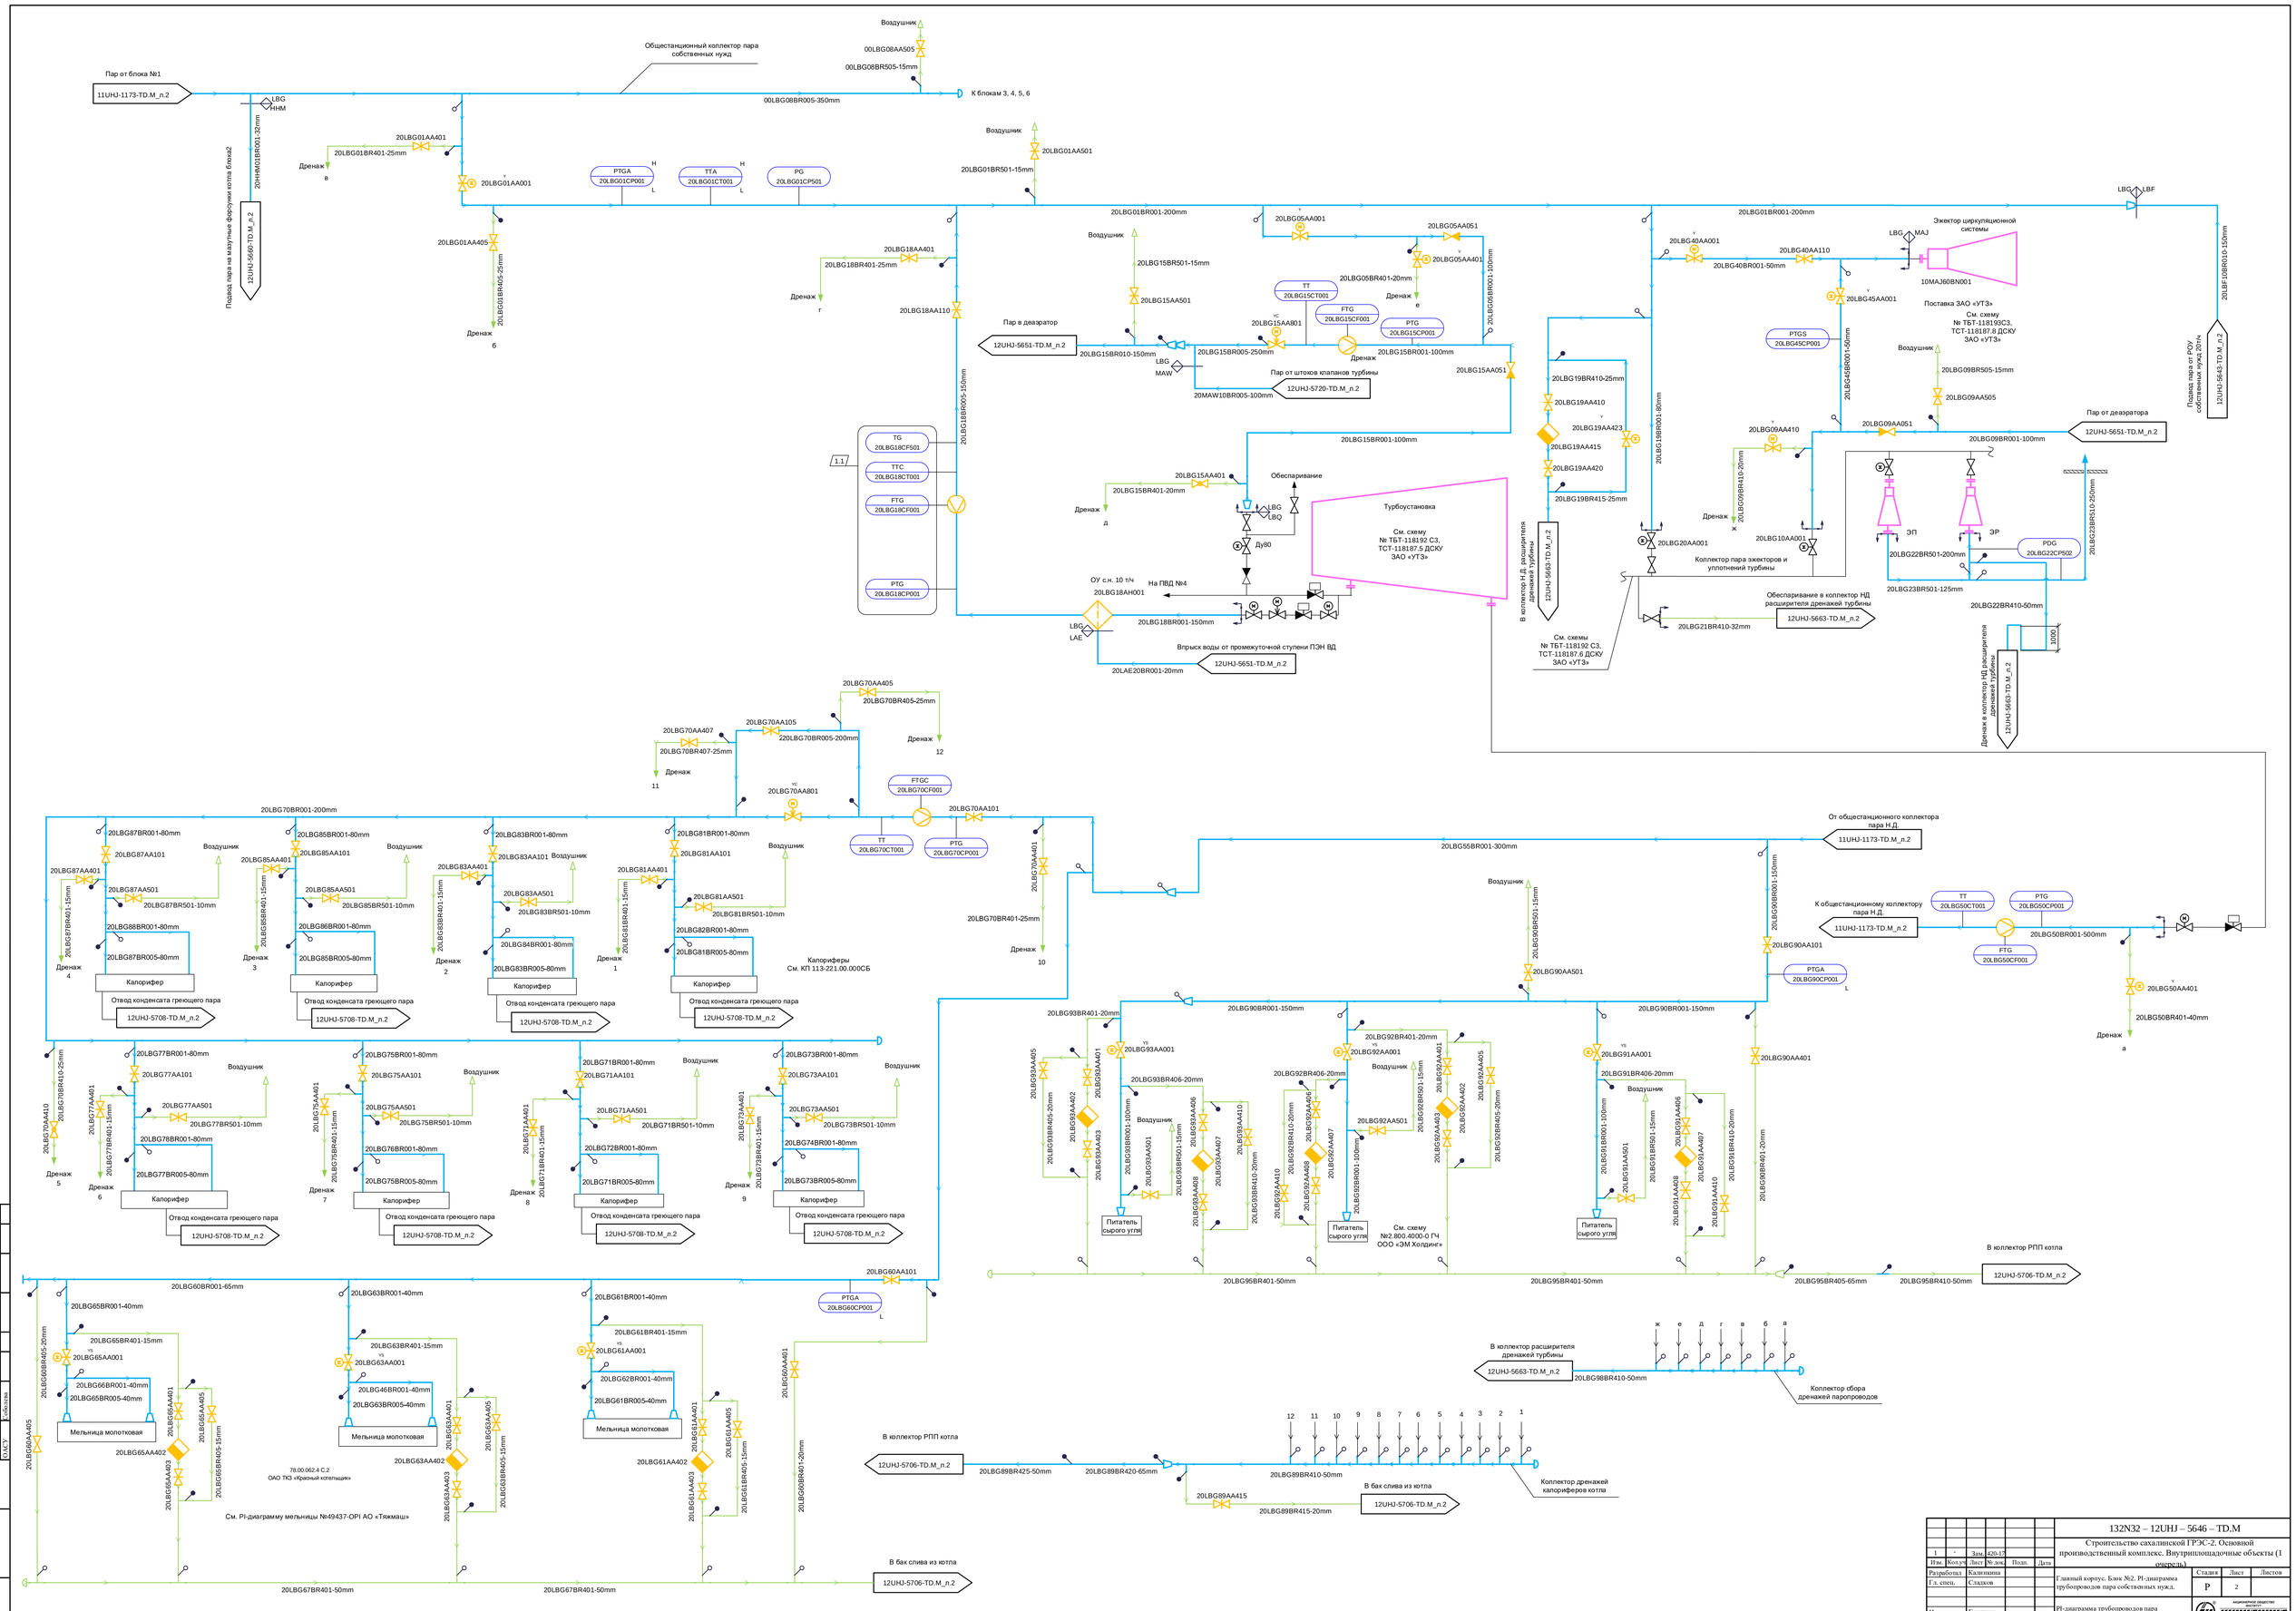

						132N32 – 12UHJ – 5646 – TD.M	
						Строительство сахалинской ГРЭС-2. Основной производственный комплекс. Внутриплощадочные объекты (1 очередь)	
1	–	Зам.	620-17				
Изм.	Кол.уч	Лист	№ док.	Подп.	Дата		
Разработал	Калинина					Главный корпус. Блок №2. PI-диаграмма трубопроводов пара собственных нужд.	Стадия: Р; Лист: 2; Листов:
Гл. спец.	Сладков						
Н. контр.	Гриднина					PI-диаграмма трубопроводов пара собственных нужд. Система LBG	Федеральное общество «Теплоэлектропроект» г. Москва

Согласовано

ОАО "Сибэнергомаш"

Формат А0