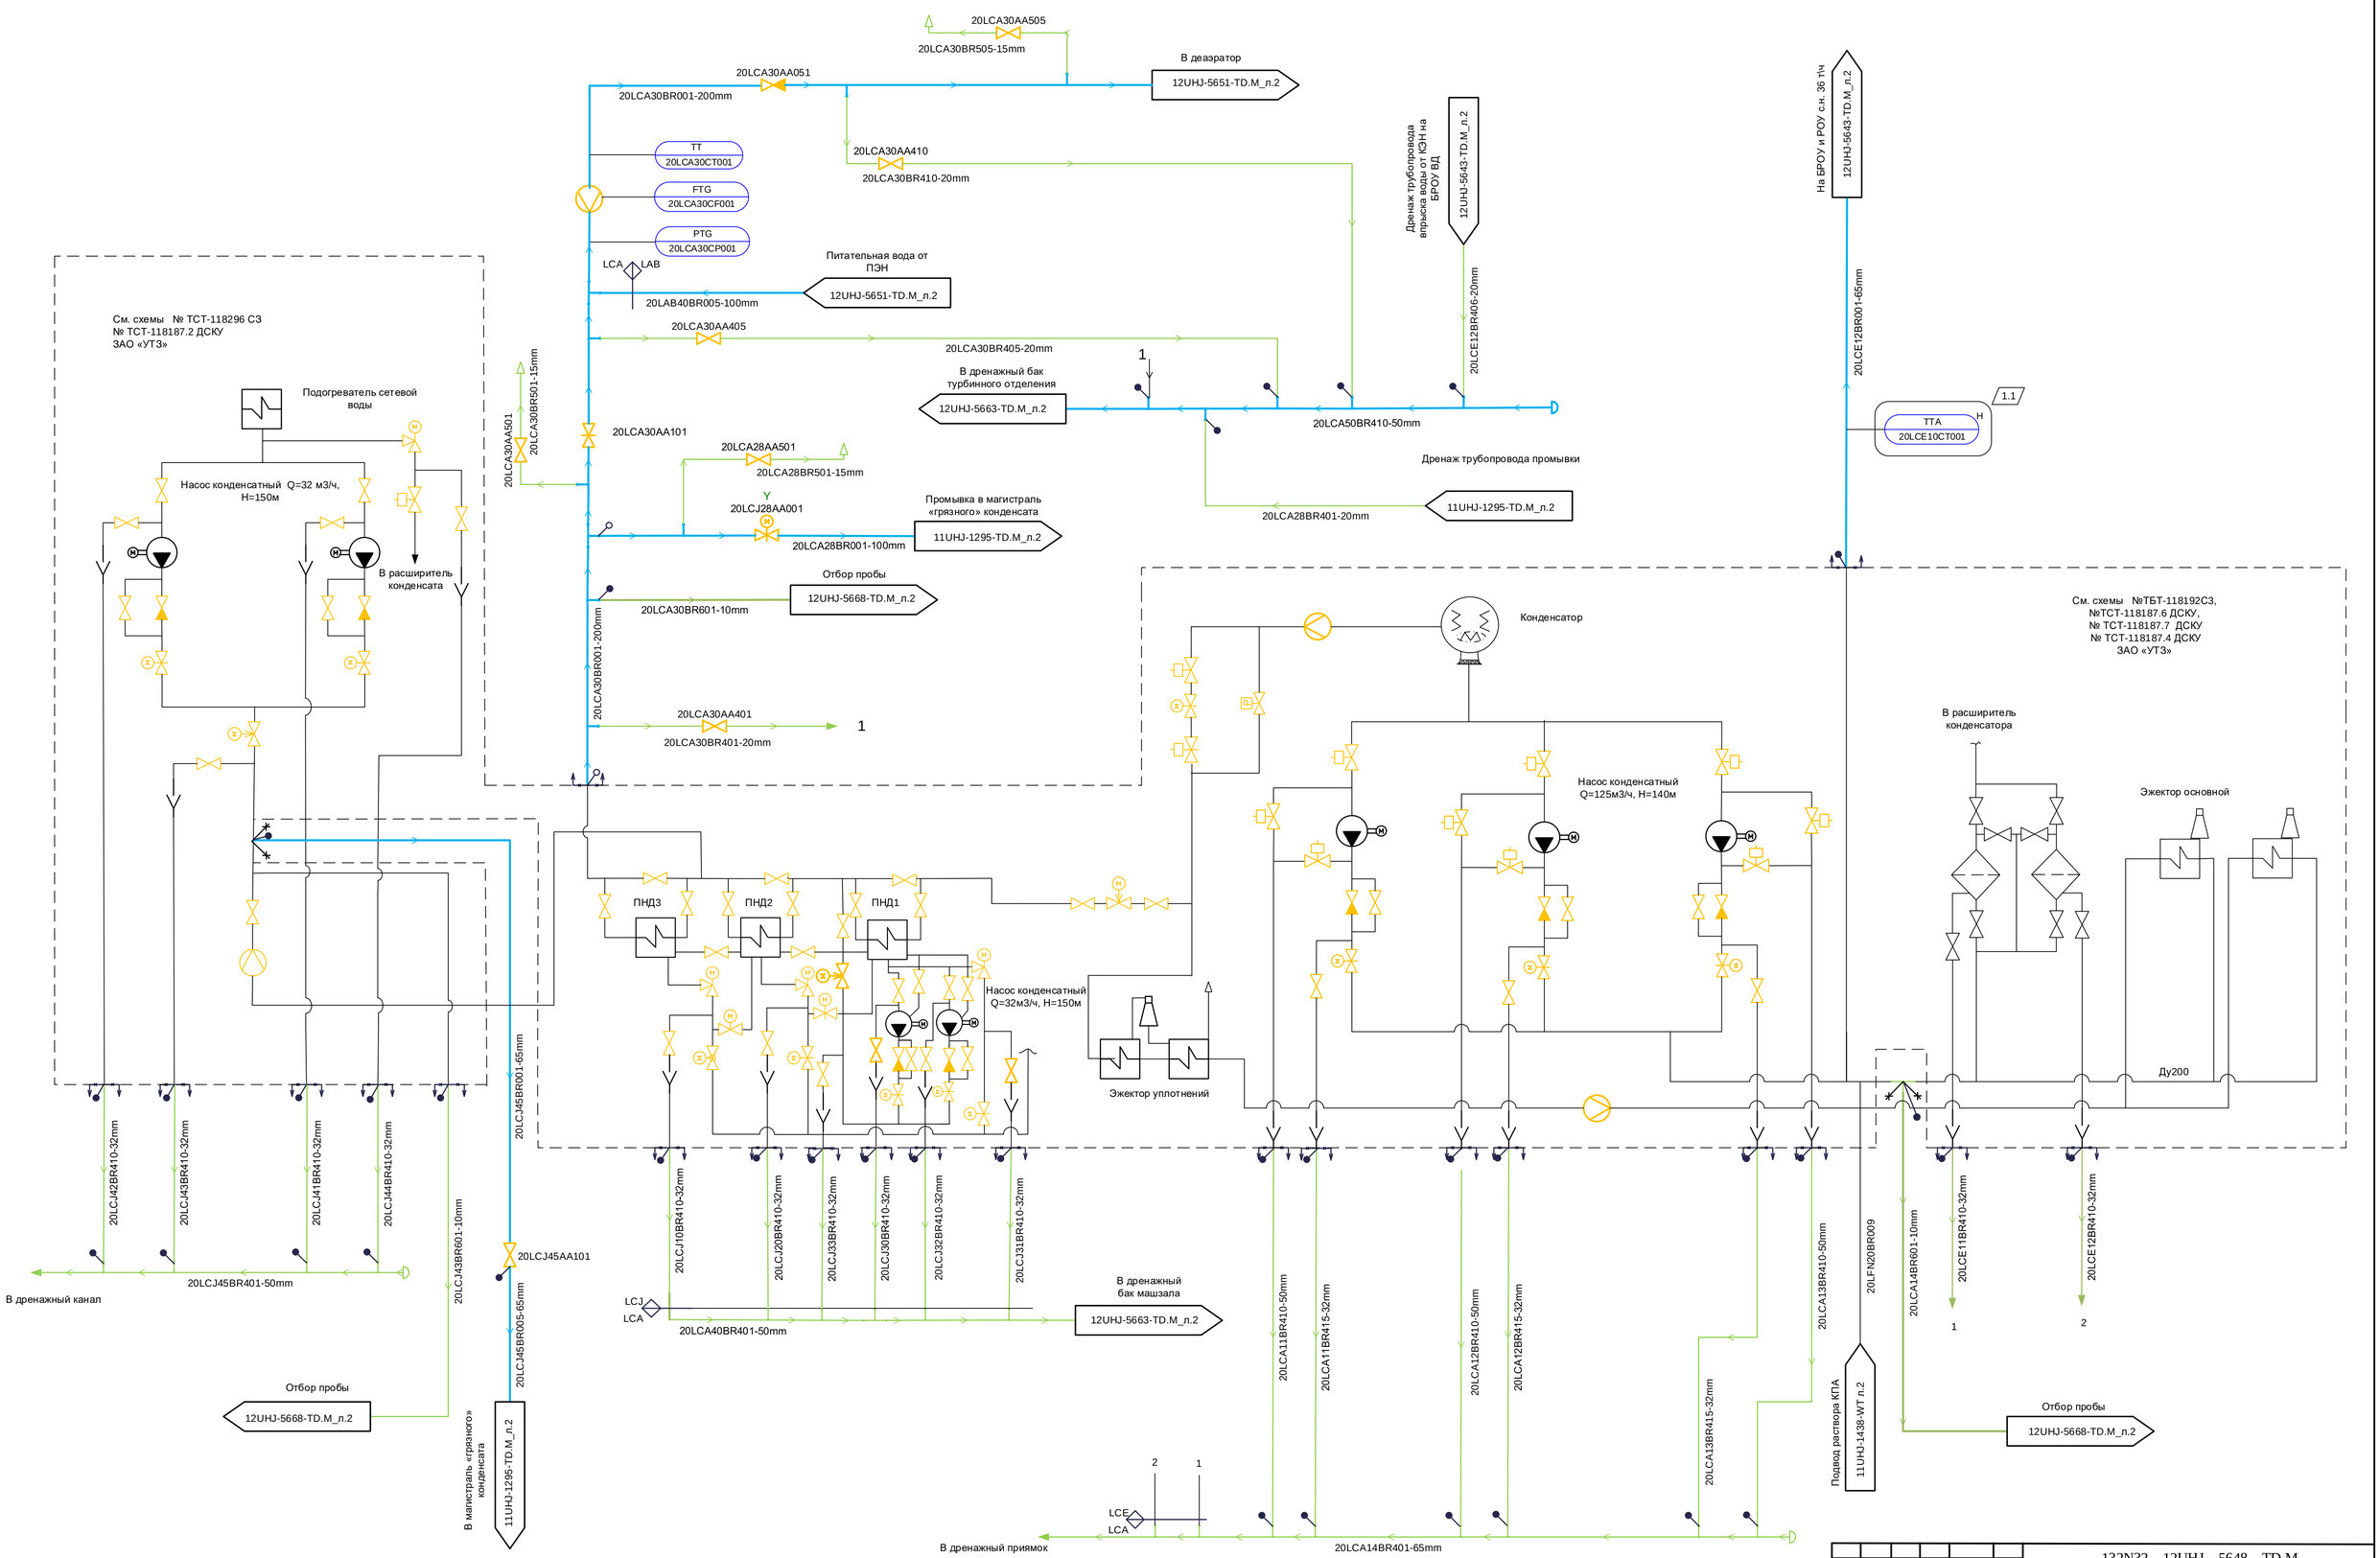

1	-	Зам.	420-17			
Изм.	Кол.уч	Лист	№ док.	Подп.	Дата	
Разработал		Калинкина				
Гл. спец.		Сладков				
Н. контр.		Гридчина				

132N32 – 12UHJ – 5648 – TD.M

Строительство Сахалинской ГРЭС-2. Основной производственный комплекс. Внутриплощадочные объекты (1-ая очередь)

Главный корпус. Блок №2. PI-диаграмма трубопроводов основного конденсата.

Стадия	Лист	Листов
Р	2	

PI-диаграмма трубопроводов основного конденсата. Система LCA, LCJ

АКЦИОНЕРНОЕ ОБЩЕСТВО ИНСТИТУТ ТЕПЛОЭЛЕКТРОПРОЕКТ г. МОСКВА

Согласовано

ОДСУ

Взам. инв. №

Подпись и дата

Инв. № подл.

Формат А1