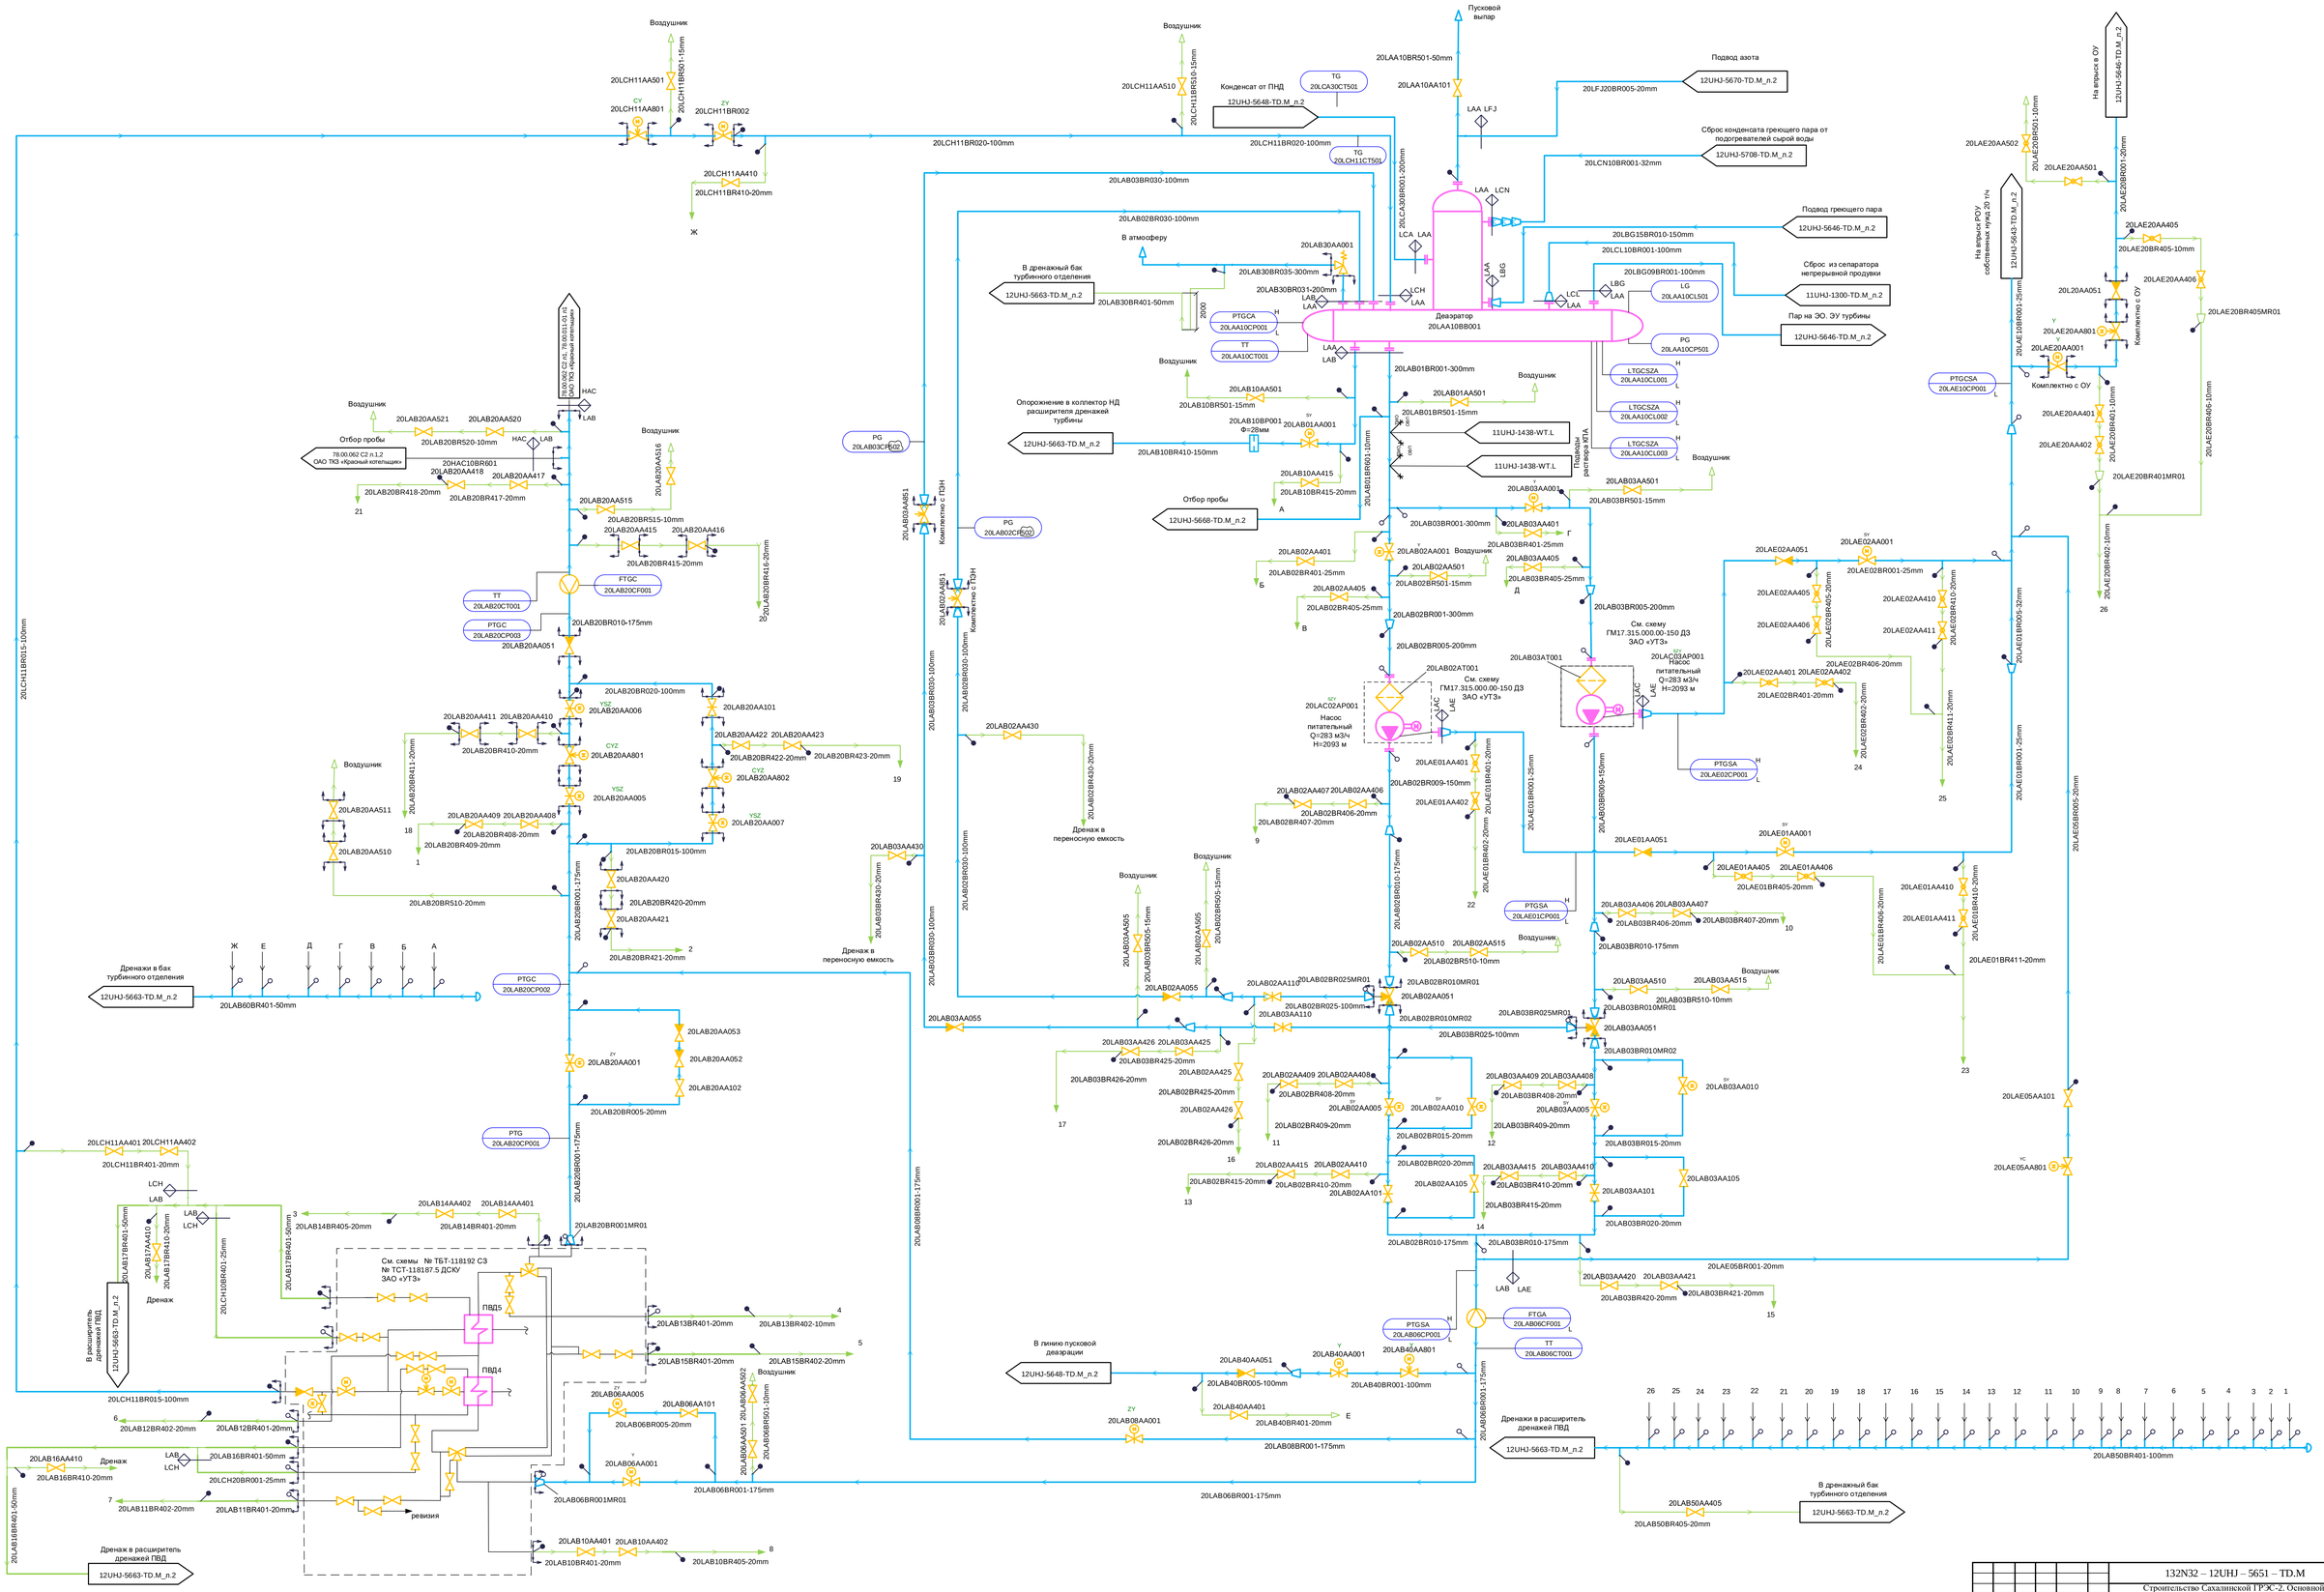

Изм.	Кол.уч	Лист	№ док.	Подп.	Дата	132N32 – 12UHJ – 5651 – TD.M
						Строительство Сахалинской ГРЭС-2. Основной производственный комплекс. Внутриплощадочные объекты (1 очередь)
Разработал		Федорцова				Главный корпус. Блок №2. PI-диаграмма трубопроводов питательной воды
Проверил		Калинкина				
Нач. гр.		Бобров				
Гл. спец.		Бакатин				PI-диаграмма трубопроводов питательной воды. Система LAB, LCH, LAE
Н. контр.		Гриднева				

Стадия	Лист	Листов
Р	2	

АКЦИОНЕРНОЕ ОБЩЕСТВО «ТЕХЭНЕРГОПРОЕКТ» г. МОСКВА

Согласовано

Взам. инв. №

Подпись и дата

Инв. № подл.

ОАО"УТ

Собственн

Формат А1