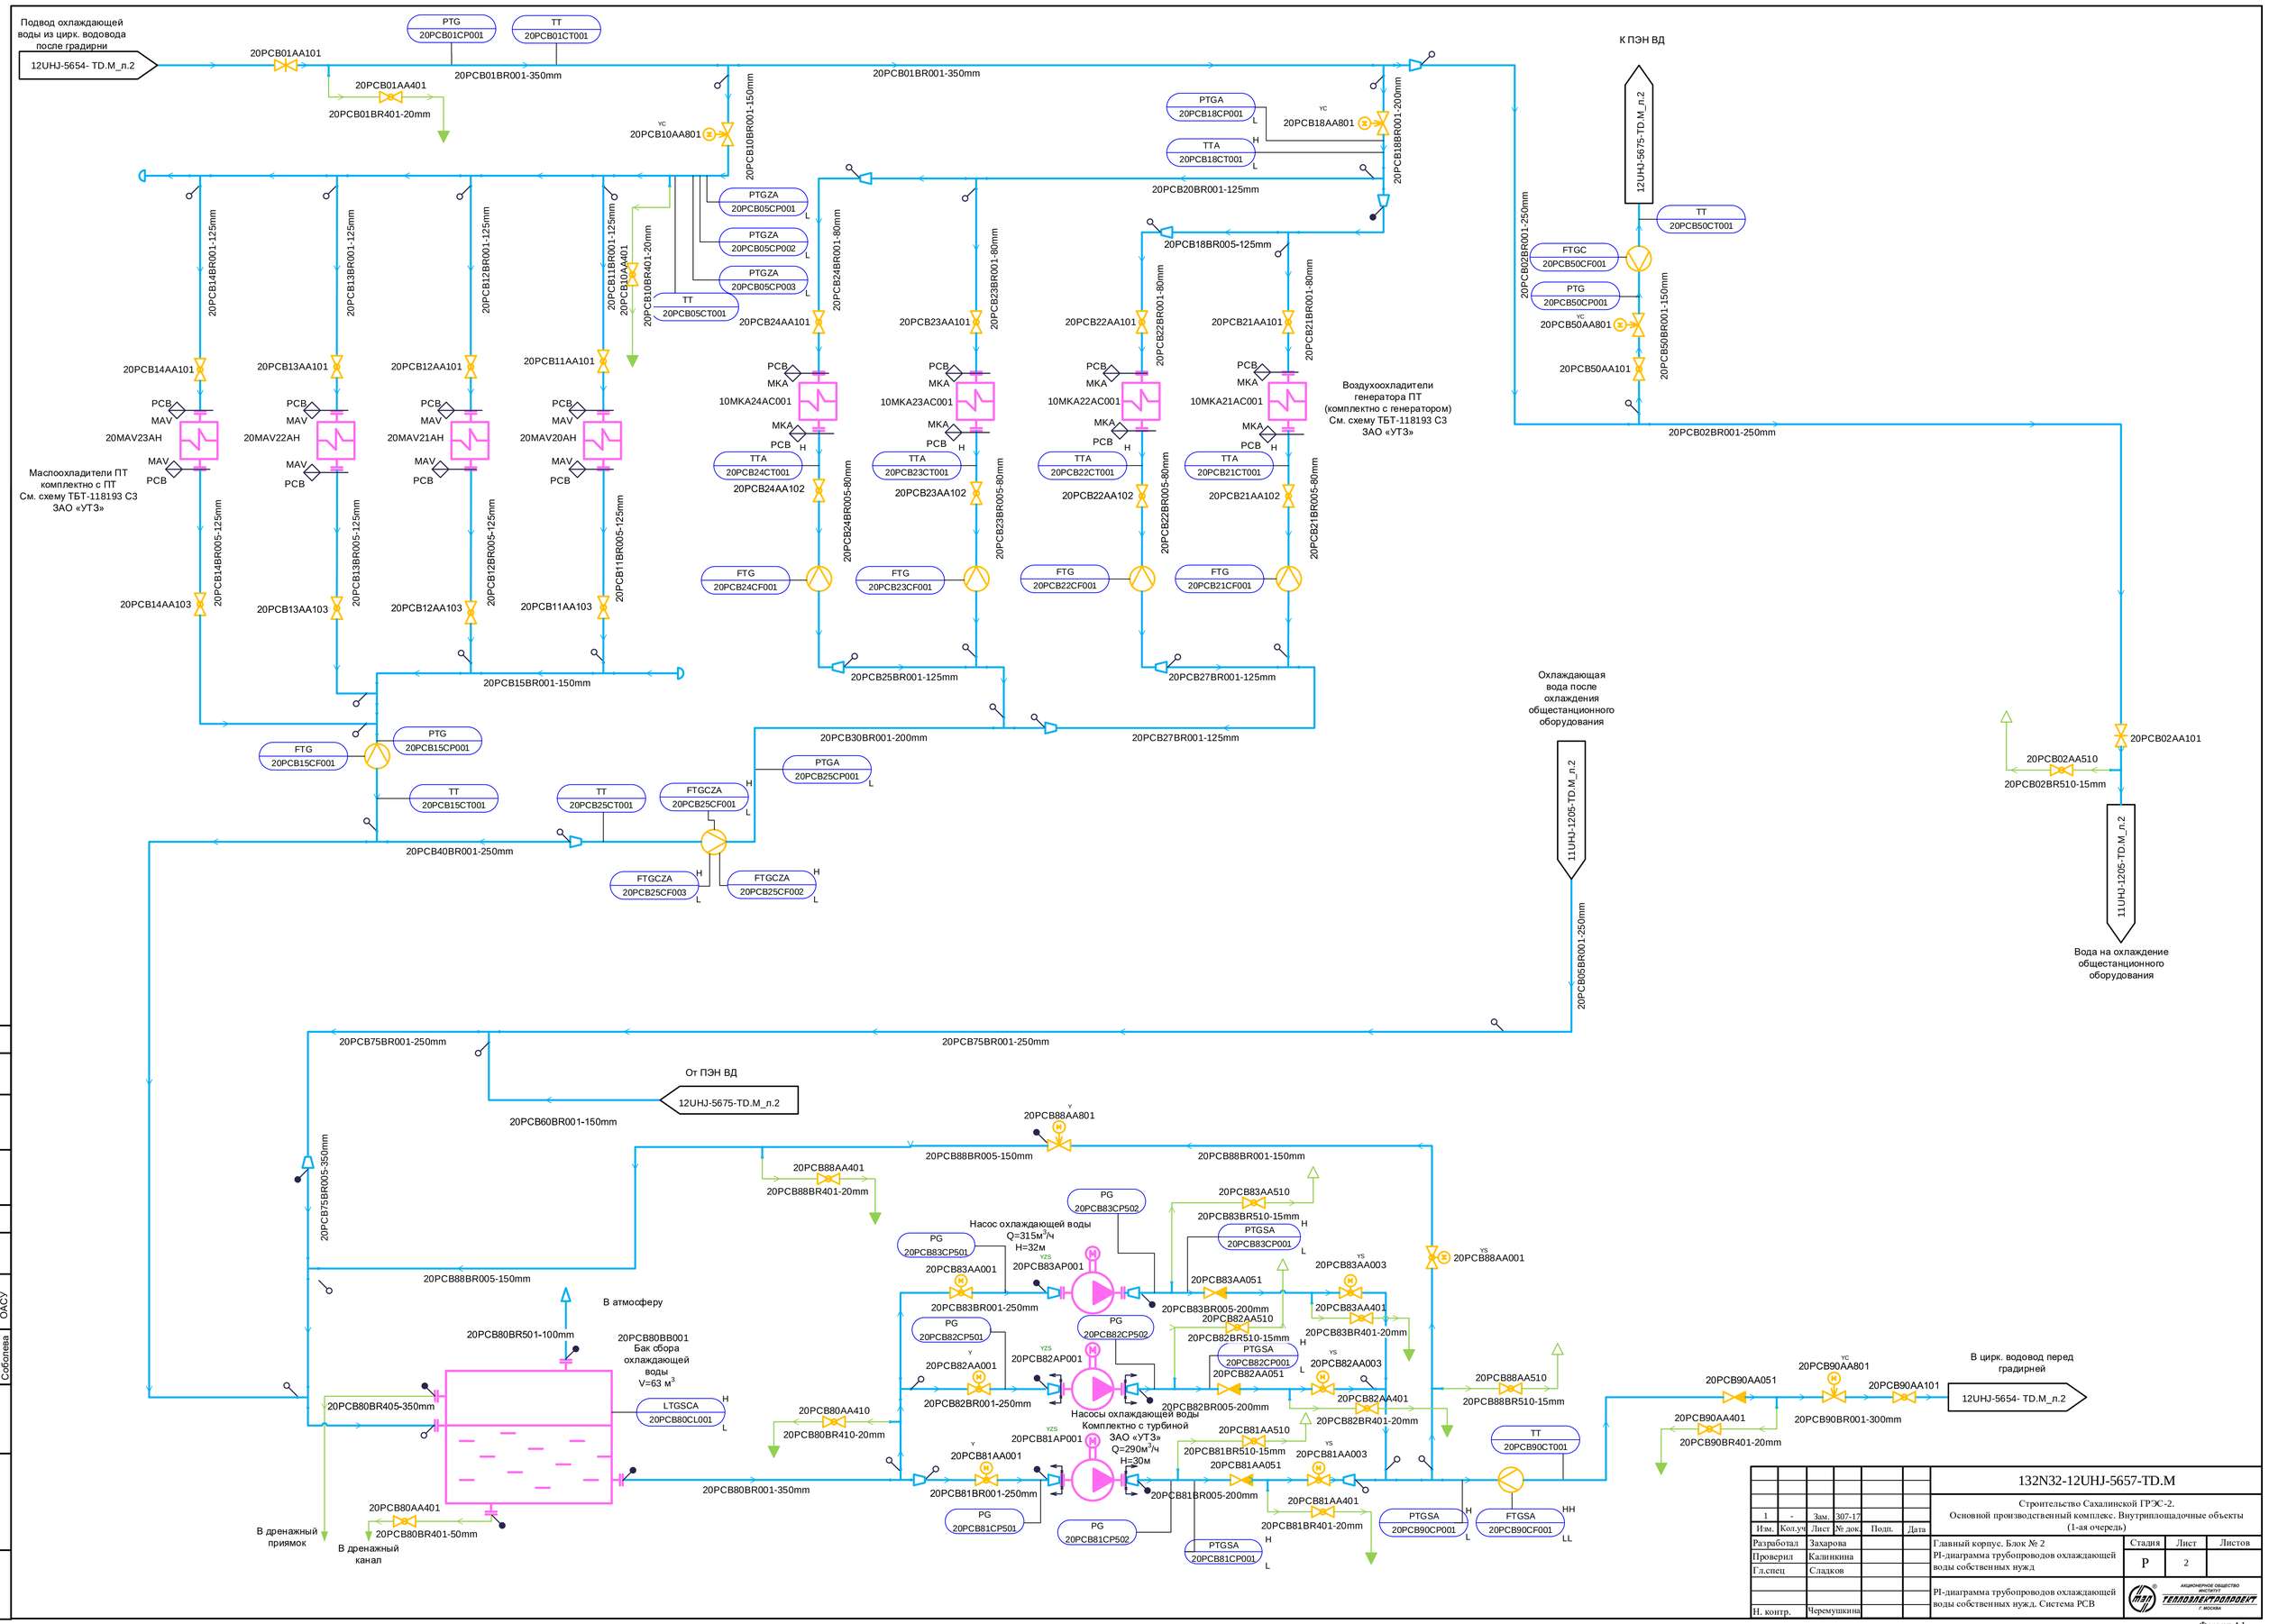
Подвод охлаждающей воды из цирк. водовода после градирни
12UHJ-5654- TD.M_л.2
20PCB01AA101
PTG 20PCB01CP001
TT 20PCB01CT001
20PCB01BR001-350mm
20PCB01AA401
20PCB01BR401-20mm
20PCB10AA801
20PCB10BR001-150mm
PTGA 20PCB18CP001
TTA 20PCB18CT001
20PCB18AA801
20PCB18BR001-200mm
20PCB20BR001-125mm
К ПЭН ВД
12UHJ-5675-TD.M_л.2
PTGZA 20PCB05CP001
PTGZA 20PCB05CP002
PTGZA 20PCB05CP003
TT 20PCB05CT001
20PCB10AA401
20PCB14BR001-125mm
20PCB13BR001-125mm
20PCB12BR001-125mm
20PCB11BR001-125mm
20PCB24BR001-80mm
20PCB23BR001-80mm
20PCB22BR001-80mm
20PCB21BR001-80mm
20PCB18BR005-125mm
20PCB02BR001-250mm
TT 20PCB50CT001
FTGC 20PCB50CF001
PTG 20PCB50CP001
20PCB50AA801
20PCB50BR001-150mm
20PCB50AA101
20PCB14AA101
20PCB13AA101
20PCB12AA101
20PCB11AA101
20PCB24AA101
20PCB23AA101
20PCB22AA101
20PCB21AA101
PCB
MAV
MKA
20MAV23AH
20MAV22AH
20MAV21AH
20MAV20AH
10MKA24AC001
10MKA23AC001
10MKA22AC001
10MKA21AC001
Воздухоохладители генератора ПТ (комплектно с генератором) См. схему ТБТ-118193 С3 ЗАО «УТЗ»
Маслоохладители ПТ комплектно с ПТ См. схему ТБТ-118193 С3 ЗАО «УТЗ»
TTA 20PCB24CT001
TTA 20PCB23CT001
TTA 20PCB22CT001
TTA 20PCB21CT001
20PCB24AA102
20PCB23AA102
20PCB22AA102
20PCB21AA102
20PCB14BR005-125mm
20PCB13BR005-125mm
20PCB12BR005-125mm
20PCB11BR005-125mm
20PCB24BR005-80mm
20PCB23BR005-80mm
20PCB22BR005-80mm
20PCB21BR005-80mm
20PCB14AA103
20PCB13AA103
20PCB12AA103
20PCB11AA103
FTG 20PCB24CF001
FTG 20PCB23CF001
FTG 20PCB22CF001
FTG 20PCB21CF001
20PCB15BR001-150mm
20PCB25BR001-125mm
20PCB27BR001-125mm
20PCB30BR001-200mm
20PCB27BR001-125mm
Охлаждающая вода после охлаждения общестанционного оборудования
11UHJ-1205-TD.M_л.2
20PCB02AA101
20PCB02AA510
20PCB02BR510-15mm
11UHJ-1205-TD.M_л.2
Вода на охлаждение общестанционного оборудования
FTG 20PCB15CF001
PTG 20PCB15CP001
TT 20PCB15CT001
TT 20PCB25CT001
FTGCZA 20PCB25CF001
PTGA 20PCB25CP001
20PCB40BR001-250mm
FTGCZA 20PCB25CF003
FTGCZA 20PCB25CF002
20PCB05BR001-250mm
20PCB75BR001-250mm
20PCB75BR001-250mm
От ПЭН ВД
12UHJ-5675-TD.M_л.2
20PCB60BR001-150mm
20PCB88AA801
20PCB88BR005-150mm
20PCB88BR001-150mm
20PCB88AA401
20PCB88BR401-20mm
20PCB75BR005-350mm
20PCB88BR005-150mm
PG 20PCB83CP502
20PCB83AA510
20PCB83BR510-15mm
PTGSA 20PCB83CP001
Насос охлаждающей воды Q=315м³/ч H=32м
PG 20PCB83CP501
20PCB83AP001
20PCB83AA001
20PCB83BR001-250mm
20PCB83AA051
20PCB83BR005-200mm
20PCB83AA003
20PCB88AA001
20PCB83AA401
20PCB83BR401-20mm
В атмосферу
20PCB80BR501-100mm
20PCB80BB001 Бак сбора охлаждающей воды V=63 м³
PG 20PCB82CP501
PG 20PCB82CP502
20PCB82AA510
20PCB82BR510-15mm
PTGSA 20PCB82CP001
20PCB82AP001
20PCB82AA001
20PCB82BR001-250mm
20PCB82AA051
20PCB82AA003
20PCB82BR005-200mm
20PCB82AA401
20PCB82BR401-20mm
20PCB88AA510
20PCB88BR510-15mm
20PCB90AA051
20PCB90AA801
20PCB90AA101
В цирк. водовод перед градирней
12UHJ-5654- TD.M_л.2
20PCB90AA401
20PCB90BR401-20mm
20PCB90BR001-300mm
20PCB80BR405-350mm
LTGSCA 20PCB80CL001
20PCB80AA410
20PCB80BR410-20mm
Насосы охлаждающей воды Комплектно с турбиной ЗАО «УТЗ» Q=290м³/ч H=30м
20PCB81AP001
20PCB81AA001
20PCB81BR001-250mm
20PCB81AA510
20PCB81BR510-15mm
20PCB81AA051
20PCB81AA003
20PCB81BR005-200mm
20PCB81AA401
20PCB81BR401-20mm
20PCB80BB501-350mm
TT 20PCB90CT001
PG 20PCB81CP501
PG 20PCB81CP502
PTGSA 20PCB81CP001
PTGSA 20PCB90CP001
FTGSA 20PCB90CF001
20PCB80AA401
20PCB80BR401-50mm
В дренажный приямок
В дренажный канал
Согласовано
Взам. инв. №
Подпись и дата
Инв. № подл.
ОАСУ
Соболева
132N32-12UHJ-5657-TD.M
Строительство Сахалинской ГРЭС-2.
Основной производственный комплекс. Внутриплощадочные объекты (1-ая очередь)
Изм. Кол.уч Лист № док. Подп. Дата
Разработал Захарова
Проверил Калинкина
Гл.спец Сладков
Н. контр. Черемушкина
Главный корпус. Блок № 2
PI-диаграмма трубопроводов охлаждающей воды собственных нужд
Стадия Лист Листов
Р 2
PI-диаграмма трубопроводов охлаждающей воды собственных нужд. Система РСВ
АКЦИОНЕРНОЕ ОБЩЕСТВО ВНИИПИ ТЕПЛОЭЛЕКТРОПРОЕКТ Г. МОСКВА
Формат А1