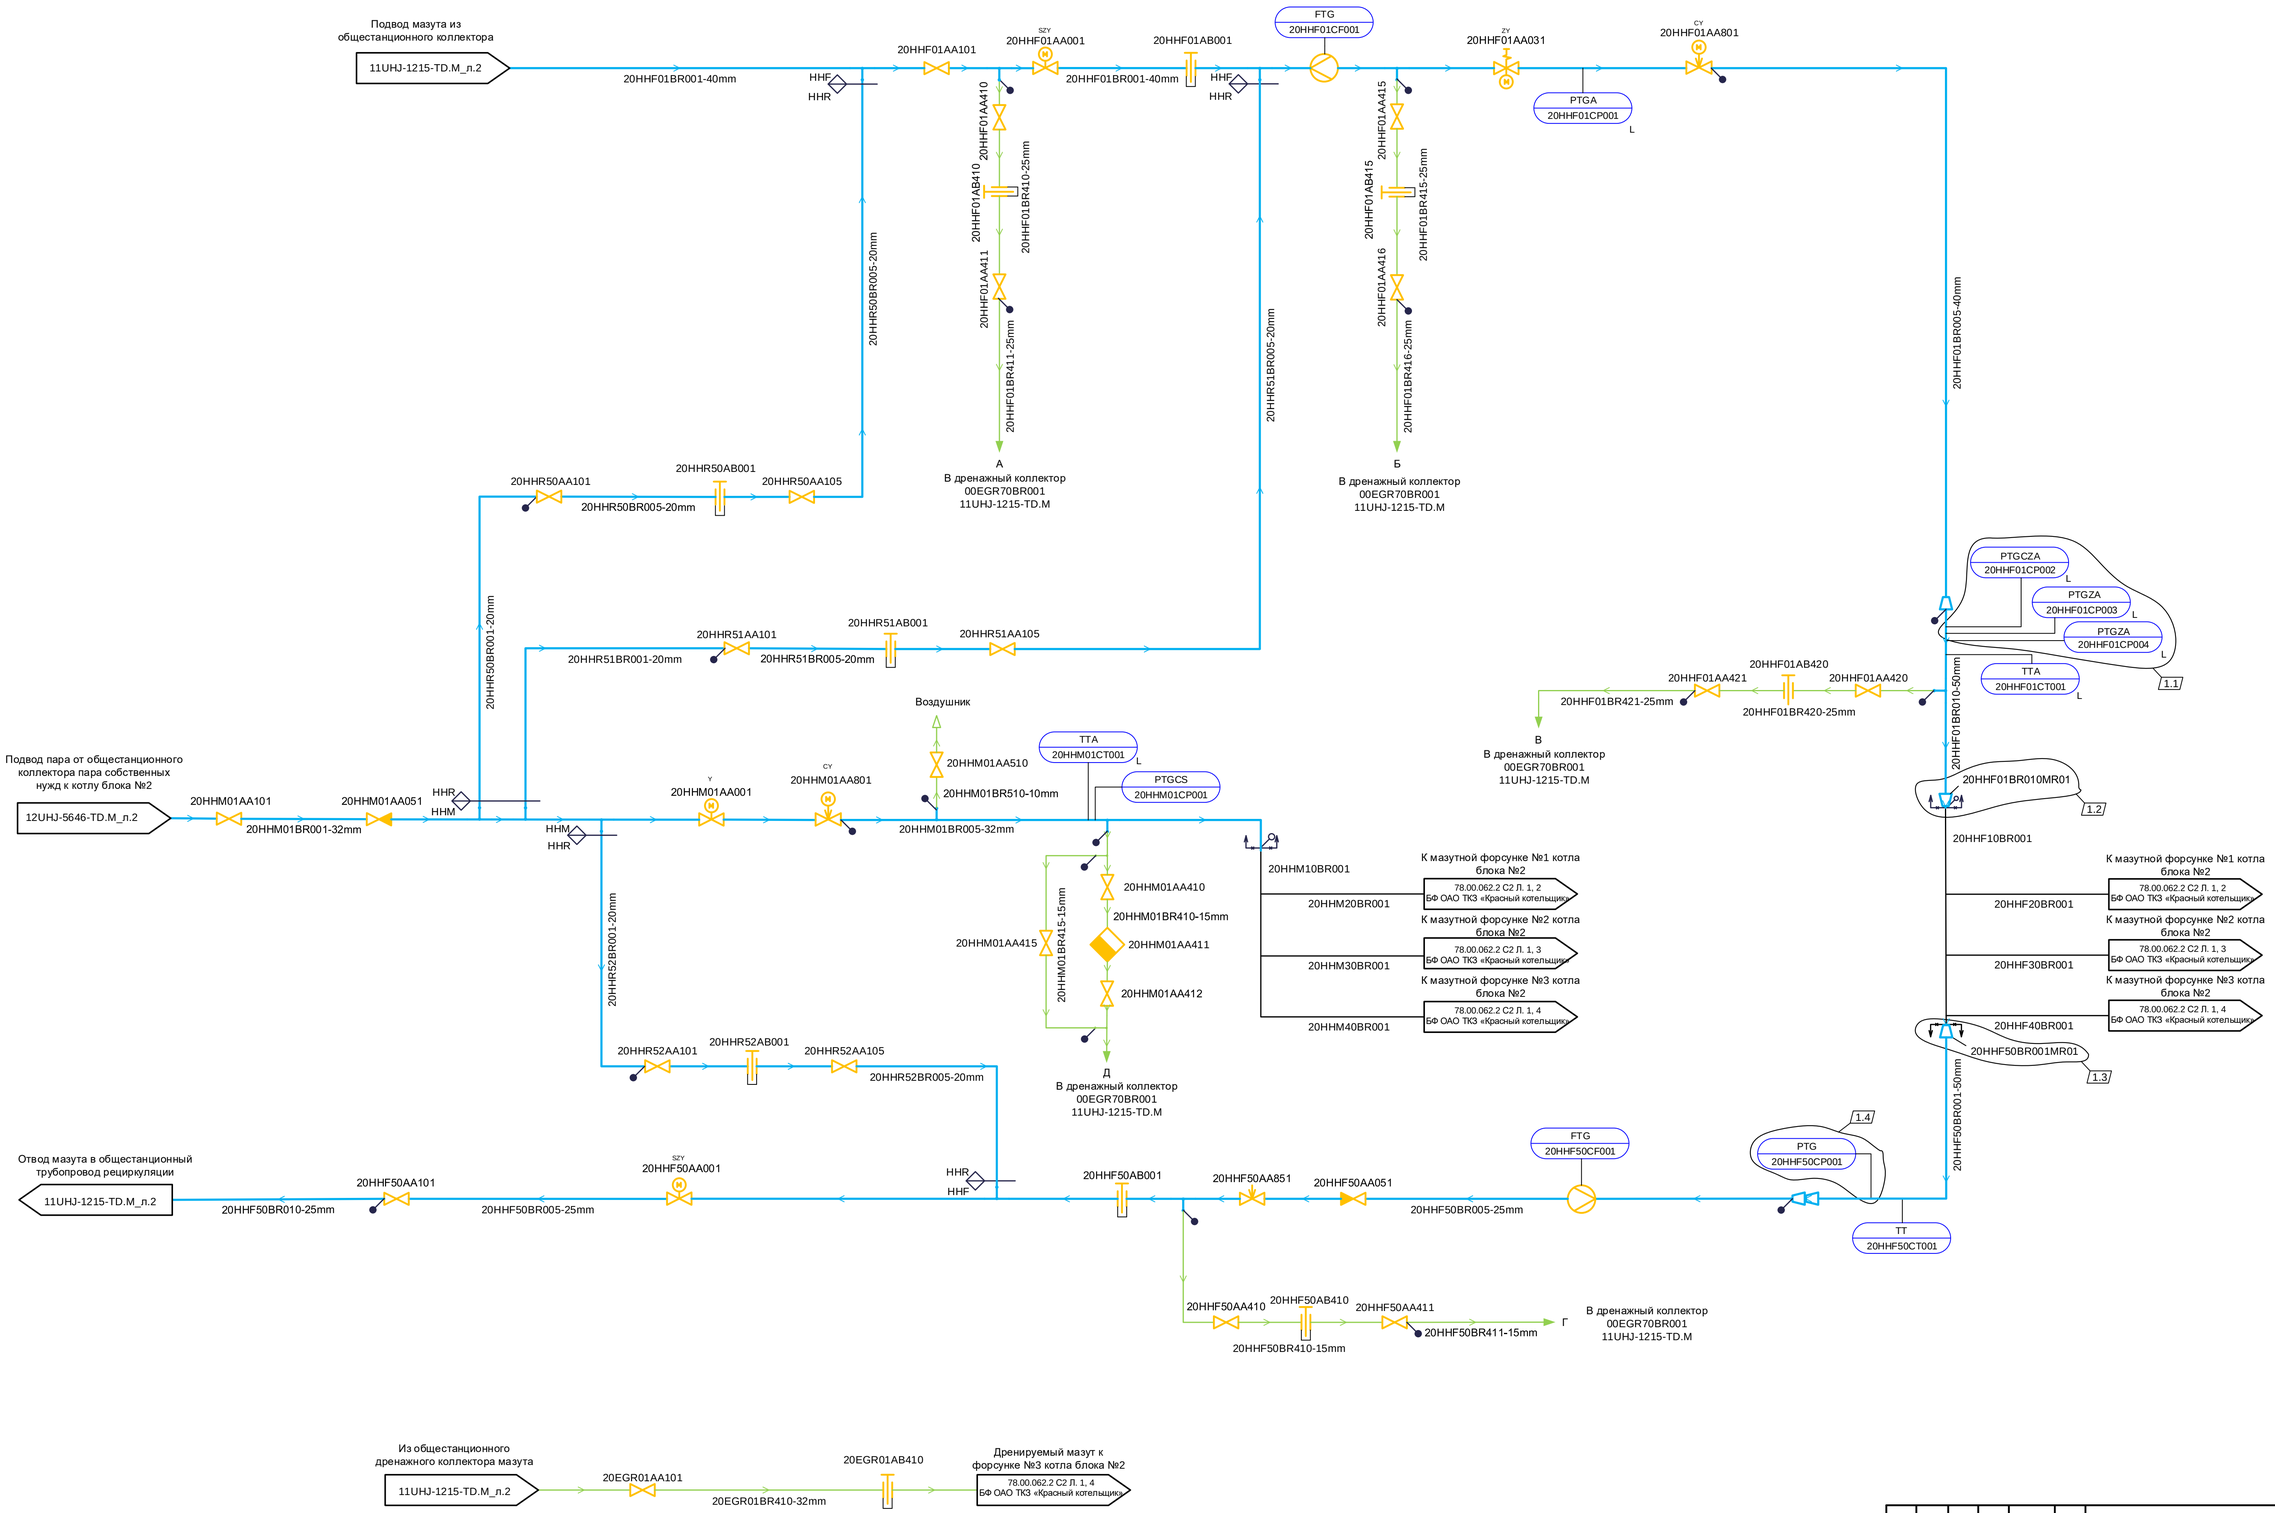

1	4	Зам.	16-17		01.17	
Изм.	Кол.уч	Лист	№ док.	Подп.	Дата	
Разработал		Калинкина				
Проверил		Бобров				
Н. контр.		Грядчина				

132N32-12UHJ-5660-TD.M

Строительство Сахалинской ГРЭС-2. Основной производственный комплекс. Внутриплощадочные объекты (1очередь)

Главный корпус. Блок №2. PI-диаграмма паромазутопроводов

Стадия	Лист	Листов
Р	2	

PI-диаграмма паромазутопроводов. Система HHF, HHM, HHR, EGR

АКЦИОНЕРНОЕ ОБЩЕСТВО ИНСТИТУТ ТЕПЛОЭЛЕКТРОПРОЕКТ г. МОСКВА

Согласовано

ОАСУ Соболева

Взам. инв. №

Подпись и дата

Инв. № подл.

Формат А1