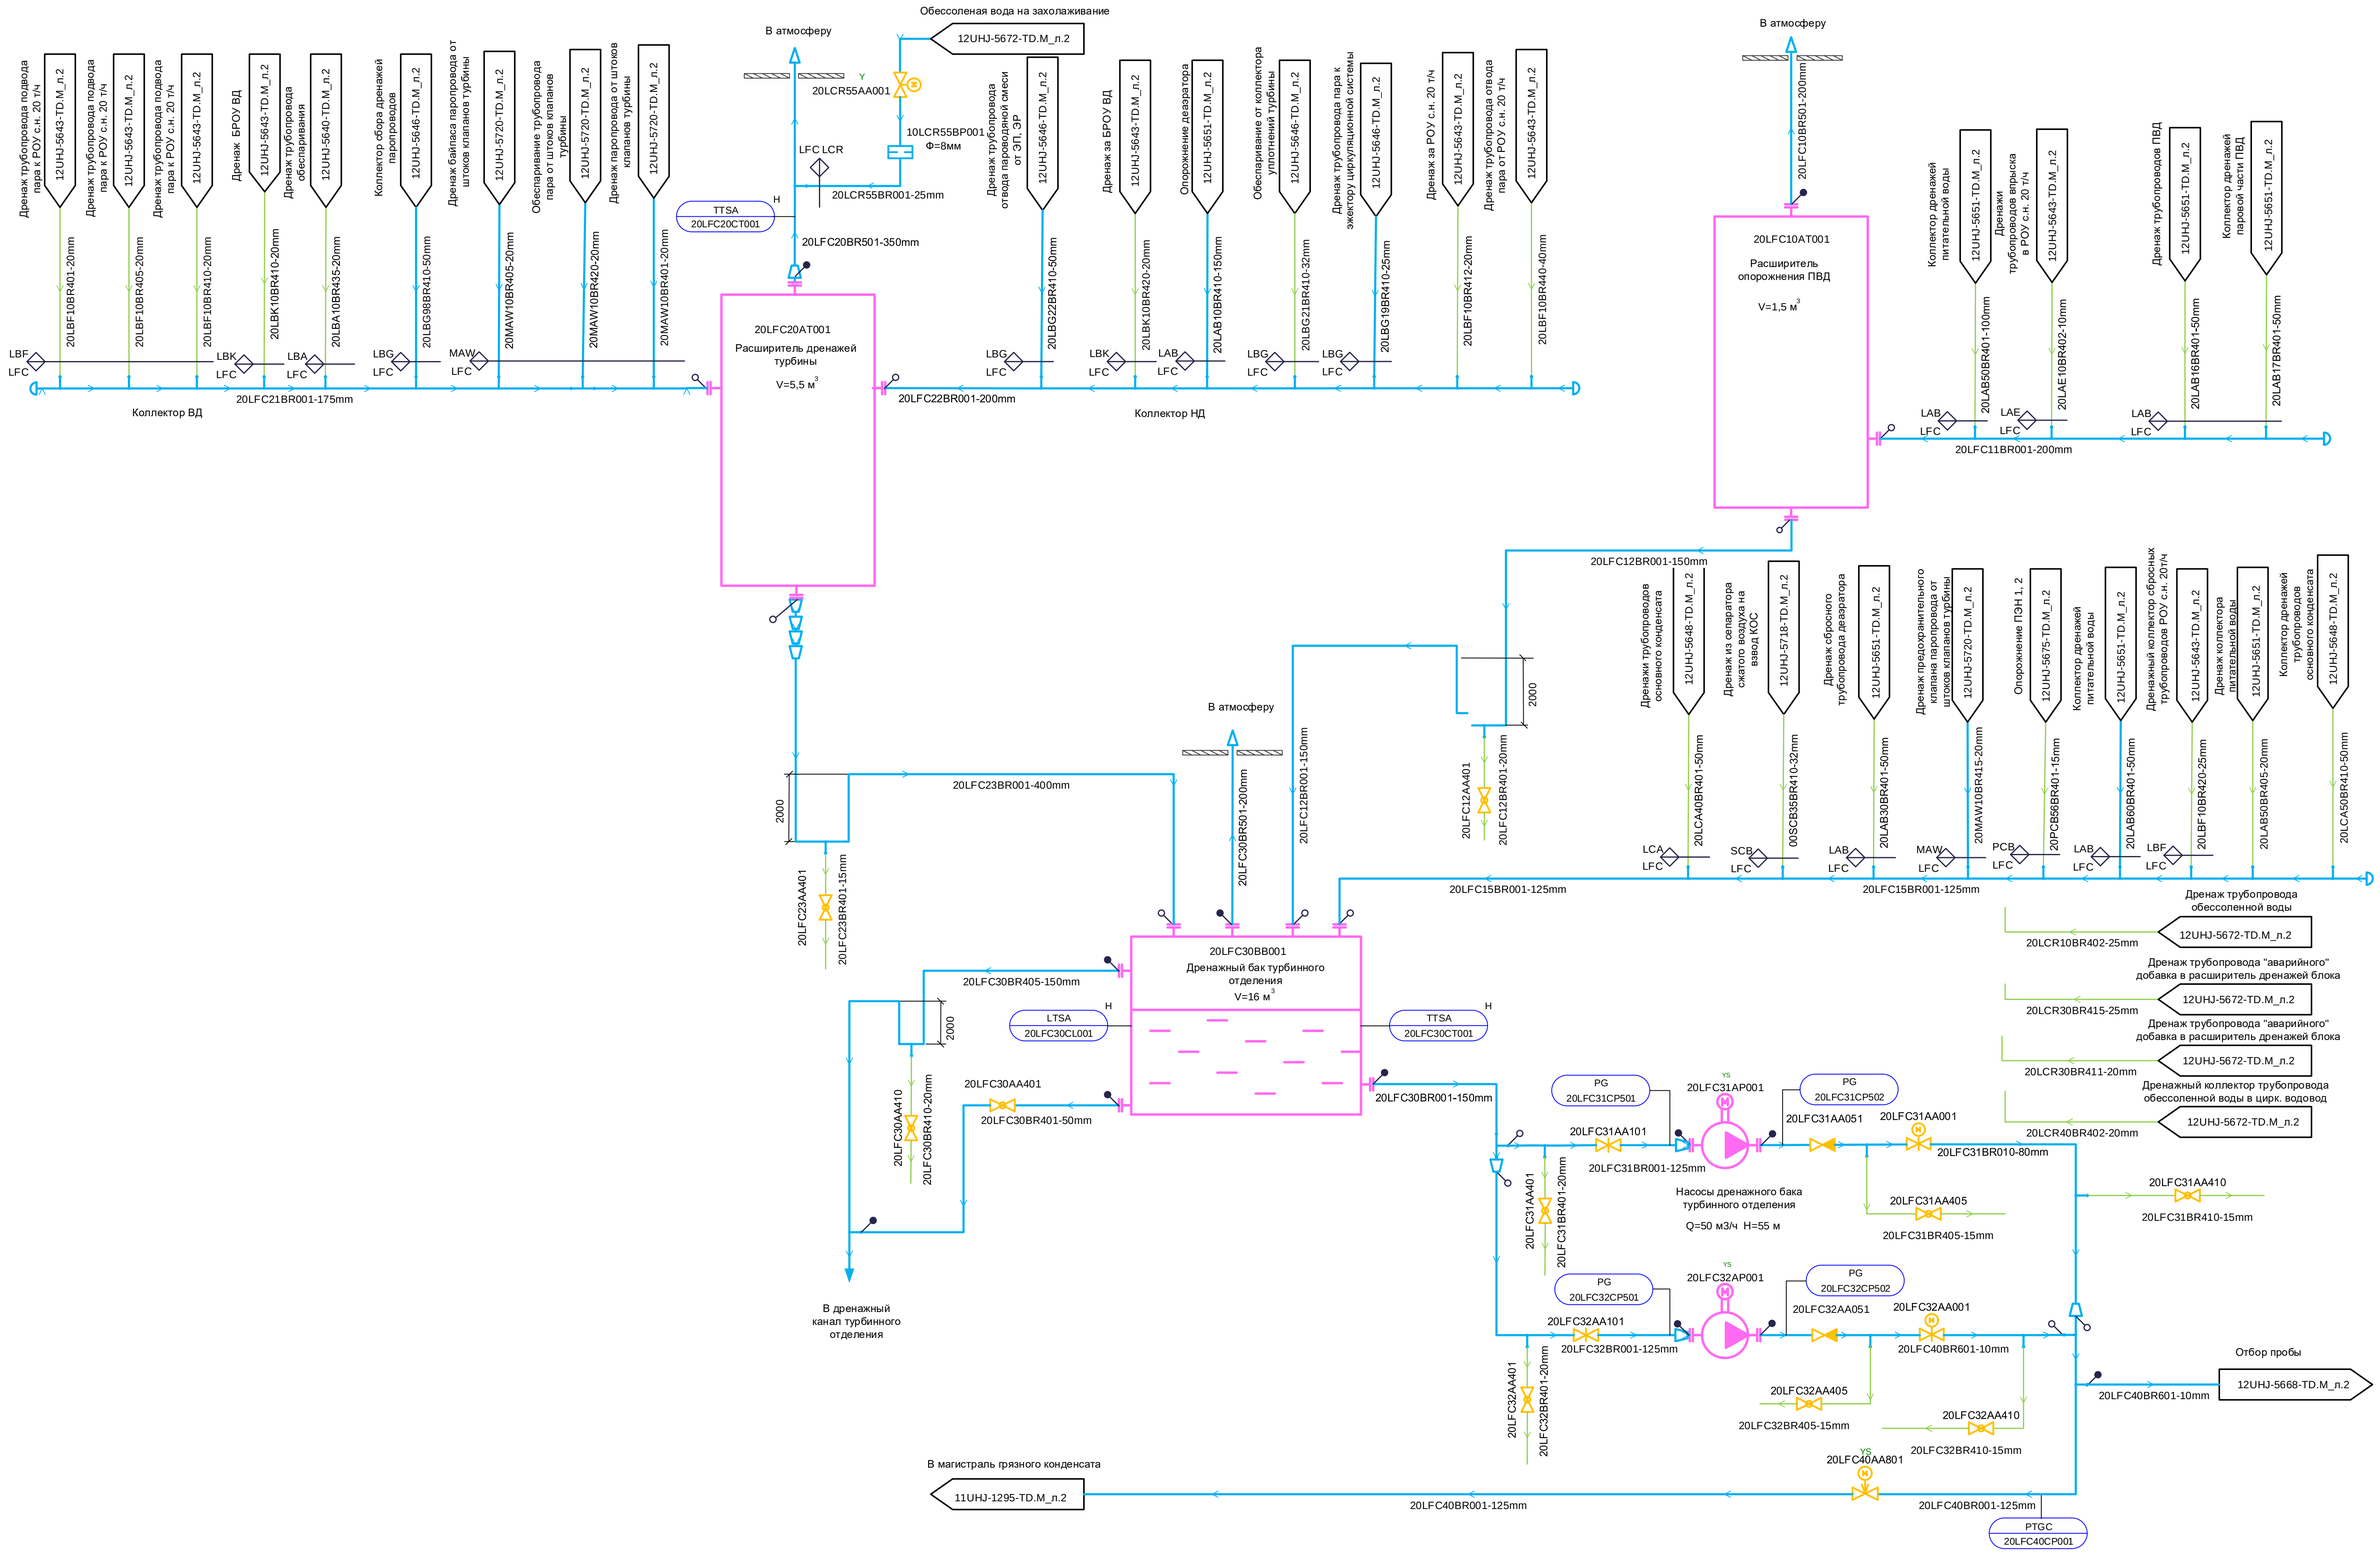

Изм.	Кол.уч.	Лист	№ док.	Подп.	Дата
Разработал		Федорцова			
Проверил		Калинкина			
Нач.гр.		Бобров			
Гл.спец.		Бакатин			
Н. контр.		Гридчина			

132N32 – 11UHJ – 5663 – TD.M

Строительство Сахалинской ГРЭС-2. Основной производственный комплекс. Внутриплощадочные объекты (1очередь)

Главный корпус. Блок №2.
PI-диаграмма трубопроводов дренажей турбинного отделения

Стадия	Лист	Листов
Р	2	

PI-диаграмма трубопроводов дренажей турбинного отделения. Система LFC , LCM

АКЦИОНЕРНОЕ ОБЩЕСТВО ИНСТИТУТ ТЕПЛОЭЛЕКТРОПРОЕКТ г. МОСКВА

Согласовано
ОАСУ Соболева

Взам. инв. №
Подпись и дата
Инв. № подл.

Формат А1