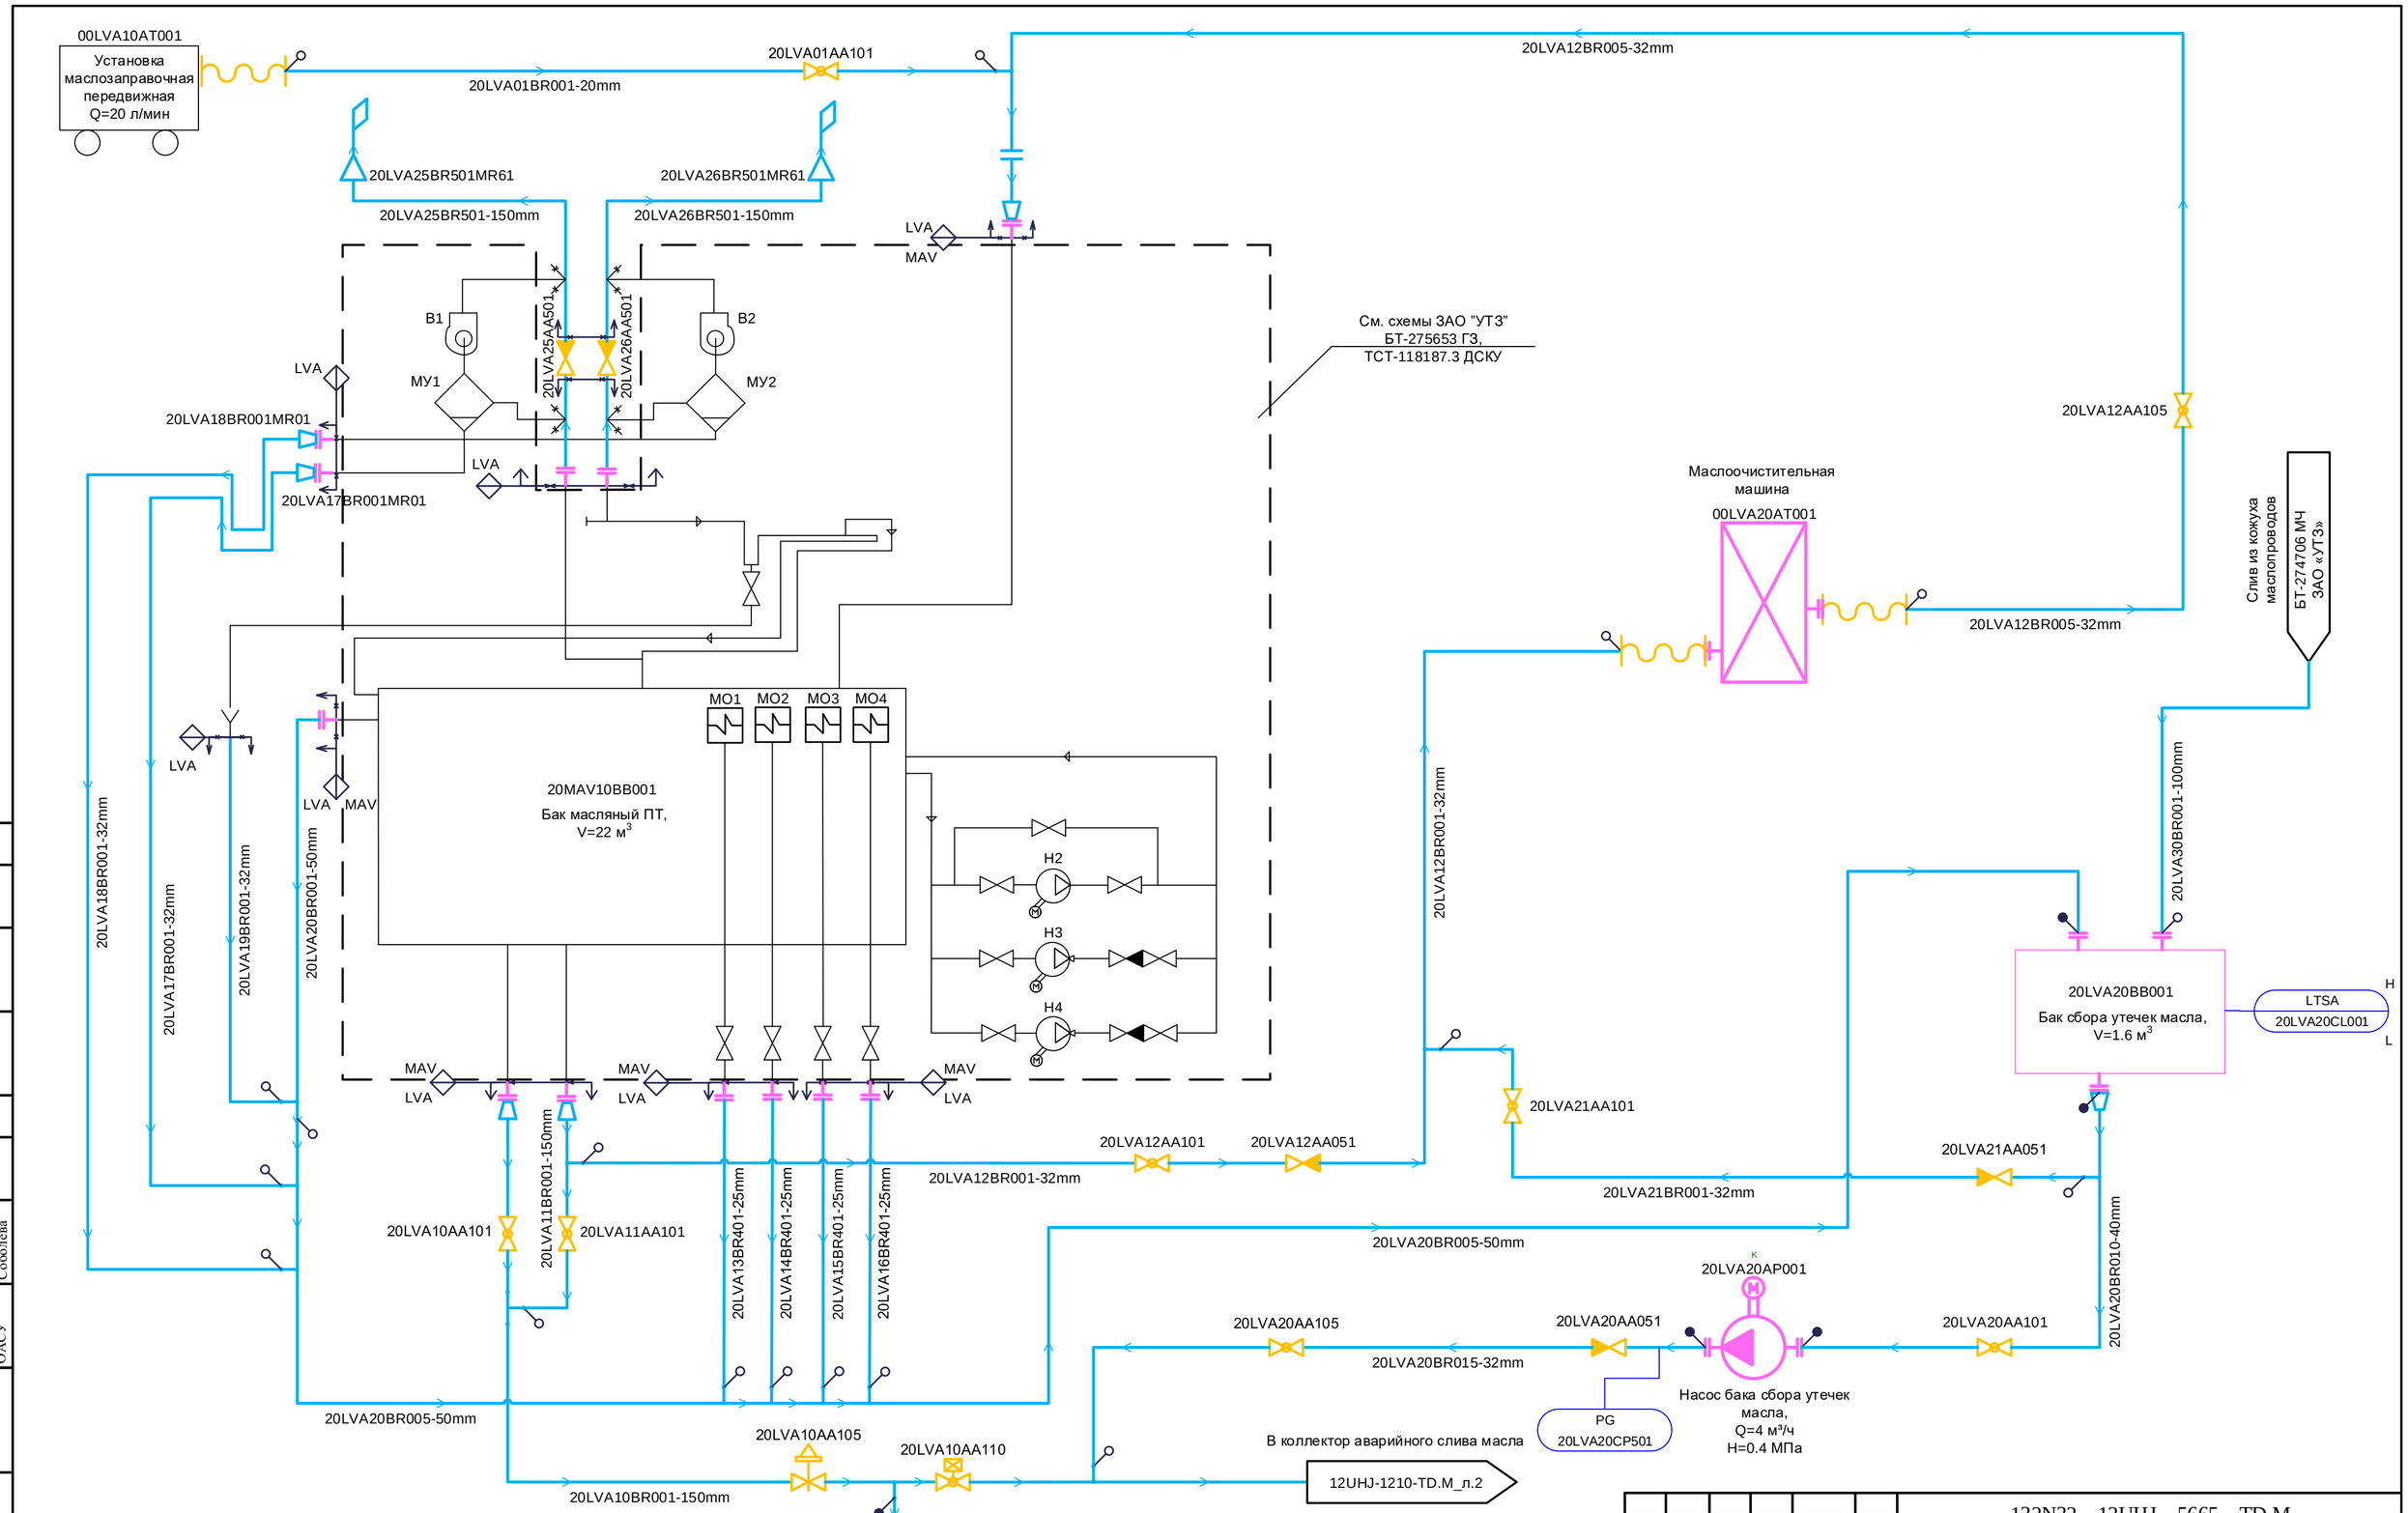

Примечание:
1. Управление насосом 20LVA20AP001 по месту.
2. При снижении уровня в баке сбора утечек масла 20LVA20BB001 до min значения отключение насоса 20LVA20AP001.
3. Сигнализация высокого уровня в баке сбора утечек масла 20LVA20BB001.
4. Задвижка 20LVA10AA105 оснащена колонковым приводом.
5. Задвижка 20LVA10AA110 оснащена замковым устройством.

Изм.	Кол.уч	Лист	№ док.	Подп.	Дата
Разработал		Тян			
Проверил		Калинкина			
Нач. гр.		Бобров			
Гл. спец.		Бакатин			
Н. контр.		Гридчина			

132N32 – 12UHJ – 5665 – TD.M

Строительство Сахалинской ГРЭС-2. Основной производственный комплекс. Внутриплощадочные объекты (1очередь)

Главный корпус. Блок №2. PI-диаграмма трубопроводов маслосистемы

Стадия	Лист	Листов
Р	2	

PI-диаграмма трубопроводов маслосистемы. Система LVA

АКЦИОНЕРНОЕ ОБЩЕСТВО ИНСТИТУТ ТЕПЛОЭЛЕКТРОПРОЕКТ Г. МОСКВА

Согласовано: ОАСУ Соболева

Взам. инв. № | Подпись и дата | Инв. № подл.

Формат А2