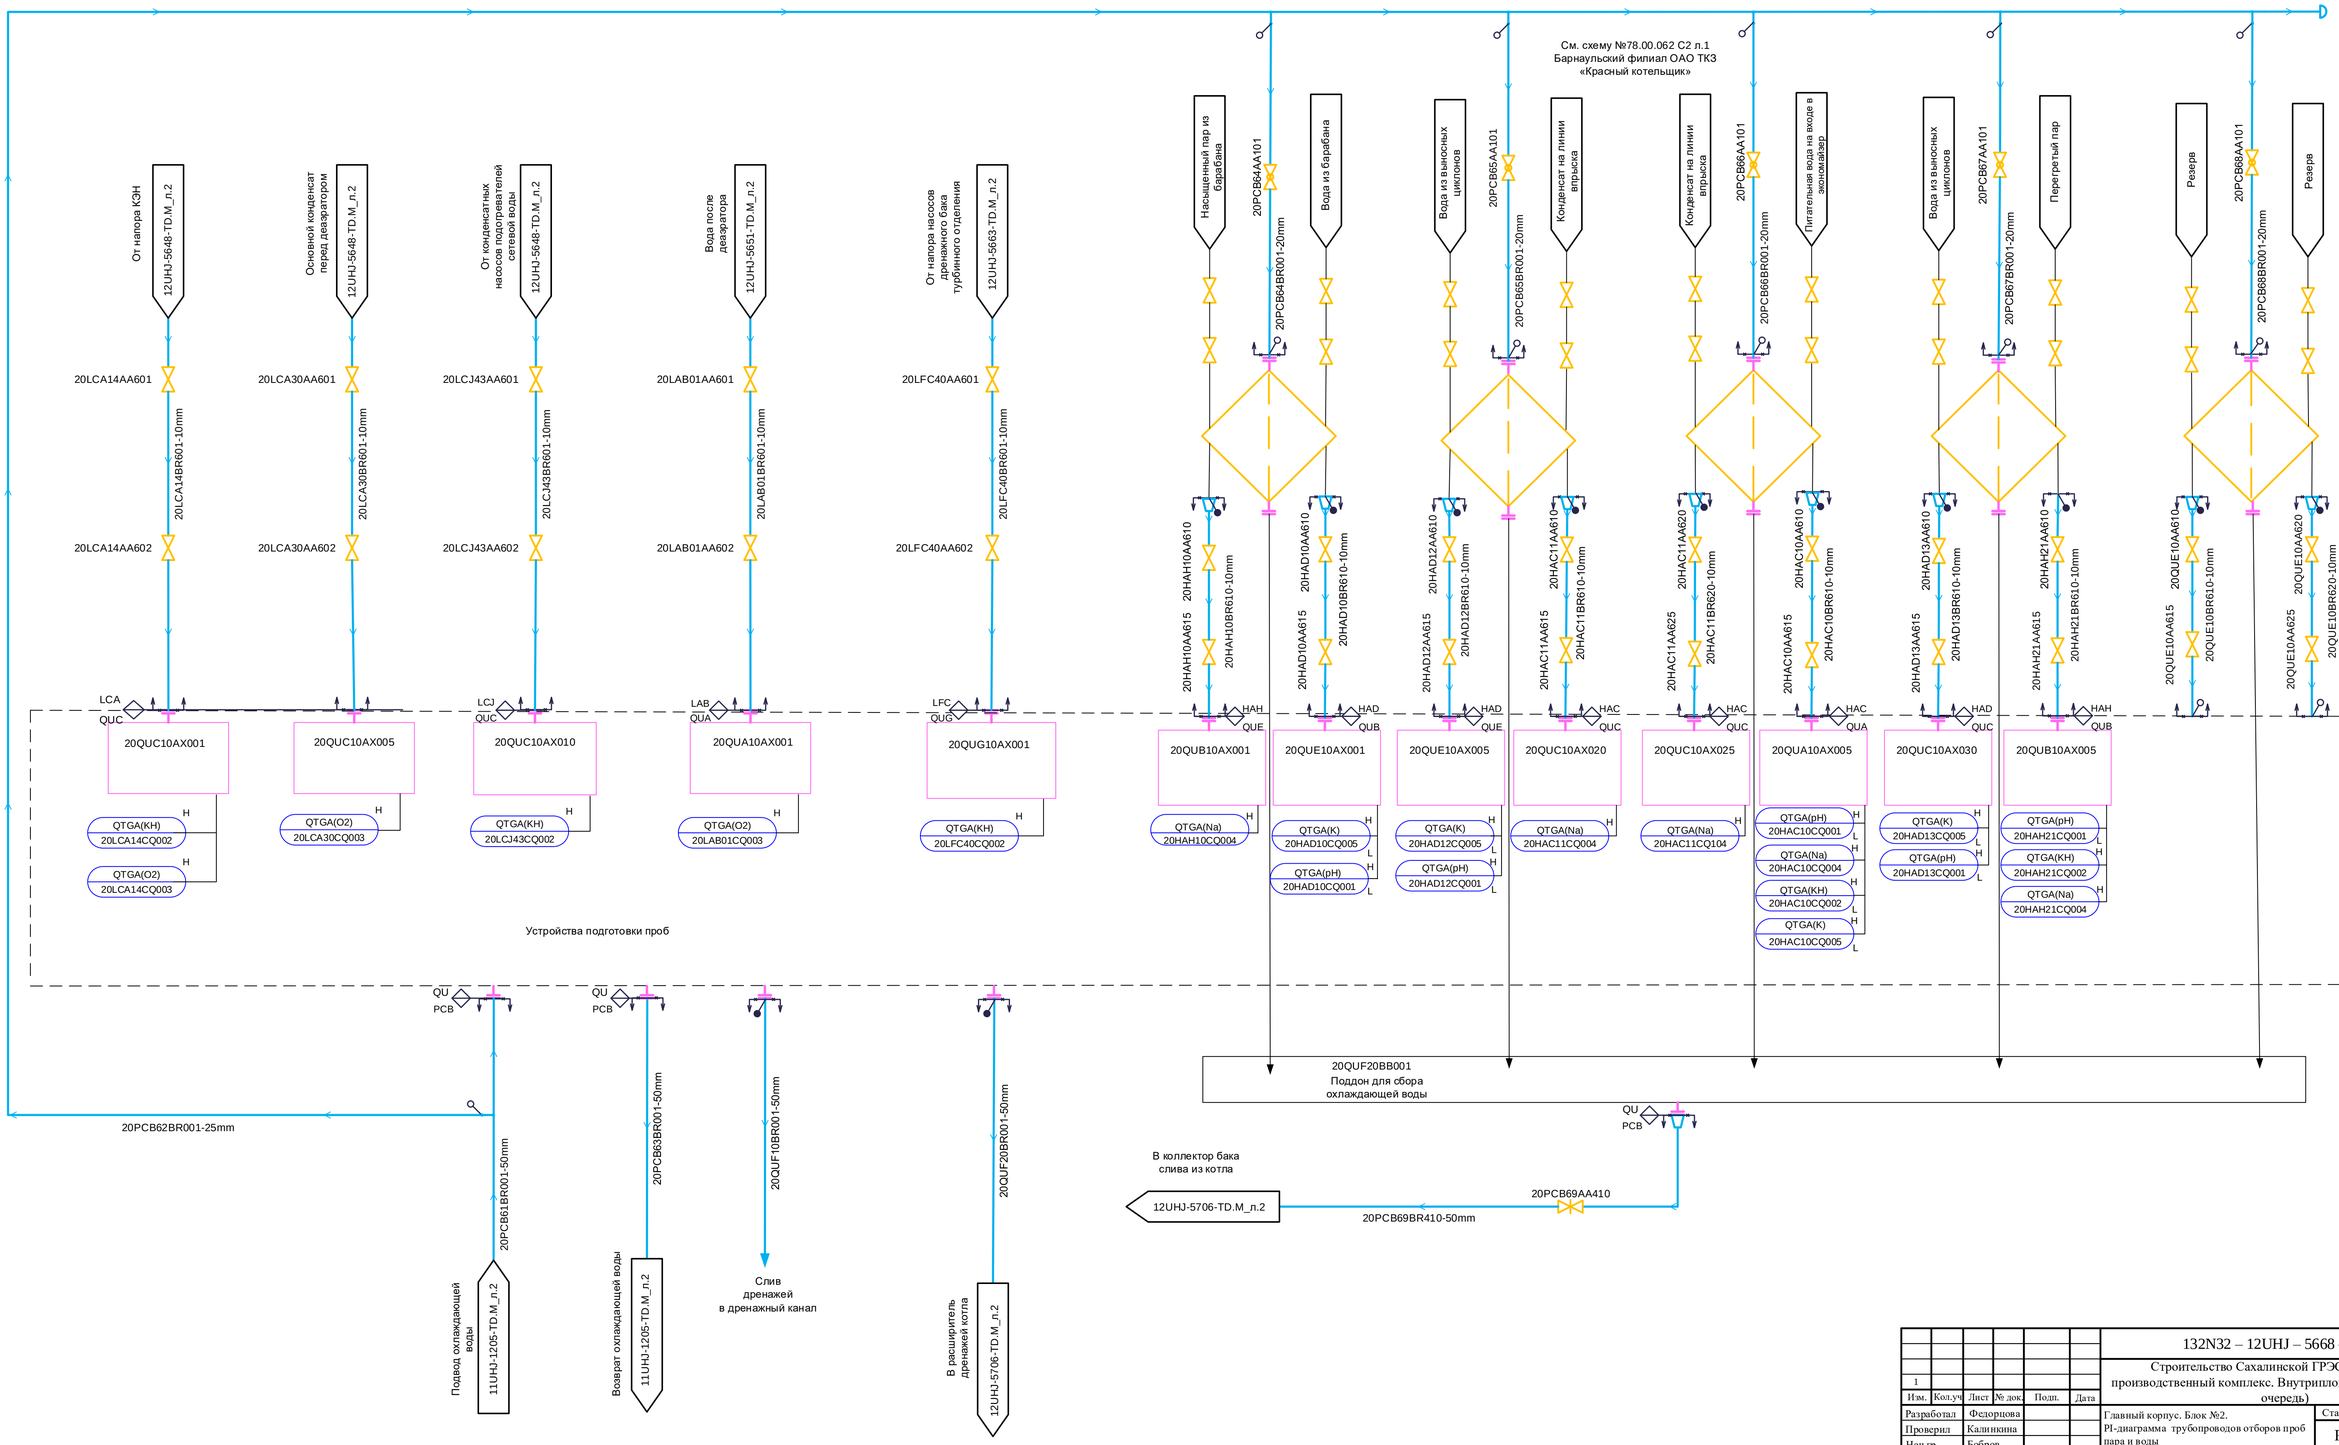

						132N32 – 12UHJ – 5668 – TD.M
1						Строительство Сахалинской ГРЭС-2. Основной производственный комплекс. Внутриплощадочные объекты (1 очередь)
Изм.	Кол.уч	Лист	№ док.	Подп.	Дата	
Разработал		Федорцова				Главный корпус. Блок №2. PI-диаграмма трубопроводов отборов проб пара и воды
Проверил		Калинкина				
Нач.гр.		Бобров				
Гл.спец.		Бакатин				PI-диаграмма трубопроводов отборов проб пара и воды. Системы QUC, QUA, QUD, QUG,QUF, PCB
Н. контр.		Гридчина				

Стадия	Лист	Листов
Р	2	

АКЦИОНЕРНОЕ ОБЩЕСТВО ИНСТИТУТ ТЕПЛОЭЛЕКТРОПРОЕКТ г. МОСКВА

Согласовано

ОАСУ Морозова

Взам. инв. №

Подпись и дата

Инв. № подл.

Формат А1