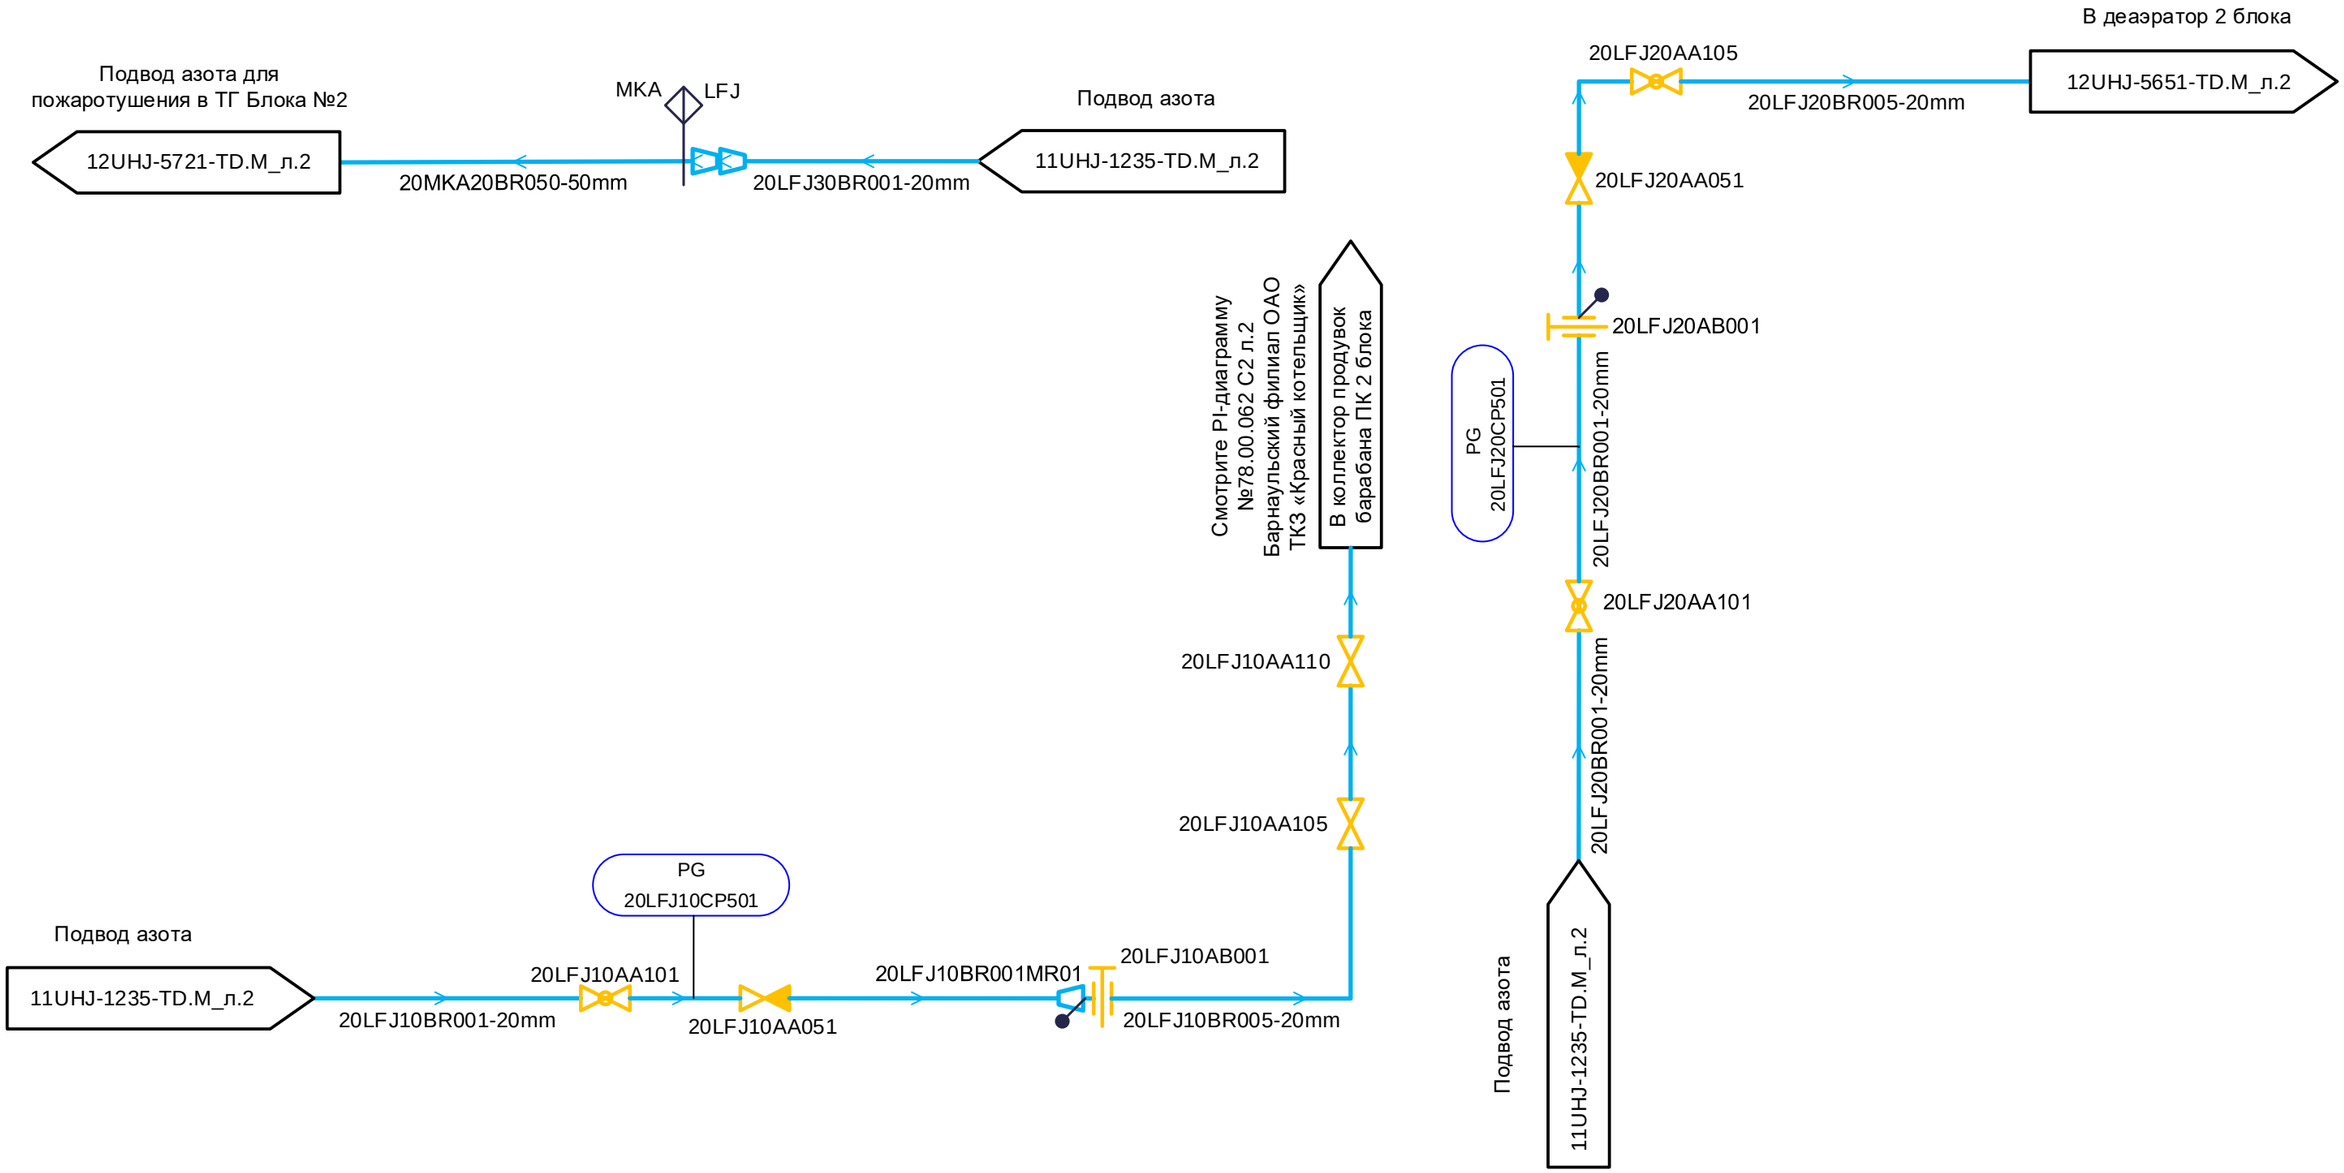

Примечание:

После заполнения системы азотом поддерживать давление 0,035 МПа (изб).

Изм.	Кол.уч	Лист	№ док.	Подп.	Дата
Разработал		Тян			
Проверил		Калинкина			
Нач. гр.		Бобров			
Гл. спец.		Бакатин			
Н. контр.		Гридчина			

132N32 – 11UHJ – 5670 – TD.M

Строительство Сахалинской ГРЭС-2. Основной производственный комплекс. Внутриплощадочные объекты (1очередь)

Главный корпус. Блок №2. PI-диаграмма трубопроводов азотной консервации

Стадия	Лист	Листов
Р	2	

PI-диаграмма трубопроводов азотной консервации.
Система LFJ

АКЦИОНЕРНОЕ ОБЩЕСТВО ИНСТИТУТ ТЕПЛОЭЛЕКТРОПРОЕКТ г. МОСКВА

Согласовано

ОАСУ Соболева

Взам. инв. №

Подпись и дата

Инв. № подл.

Формат А3