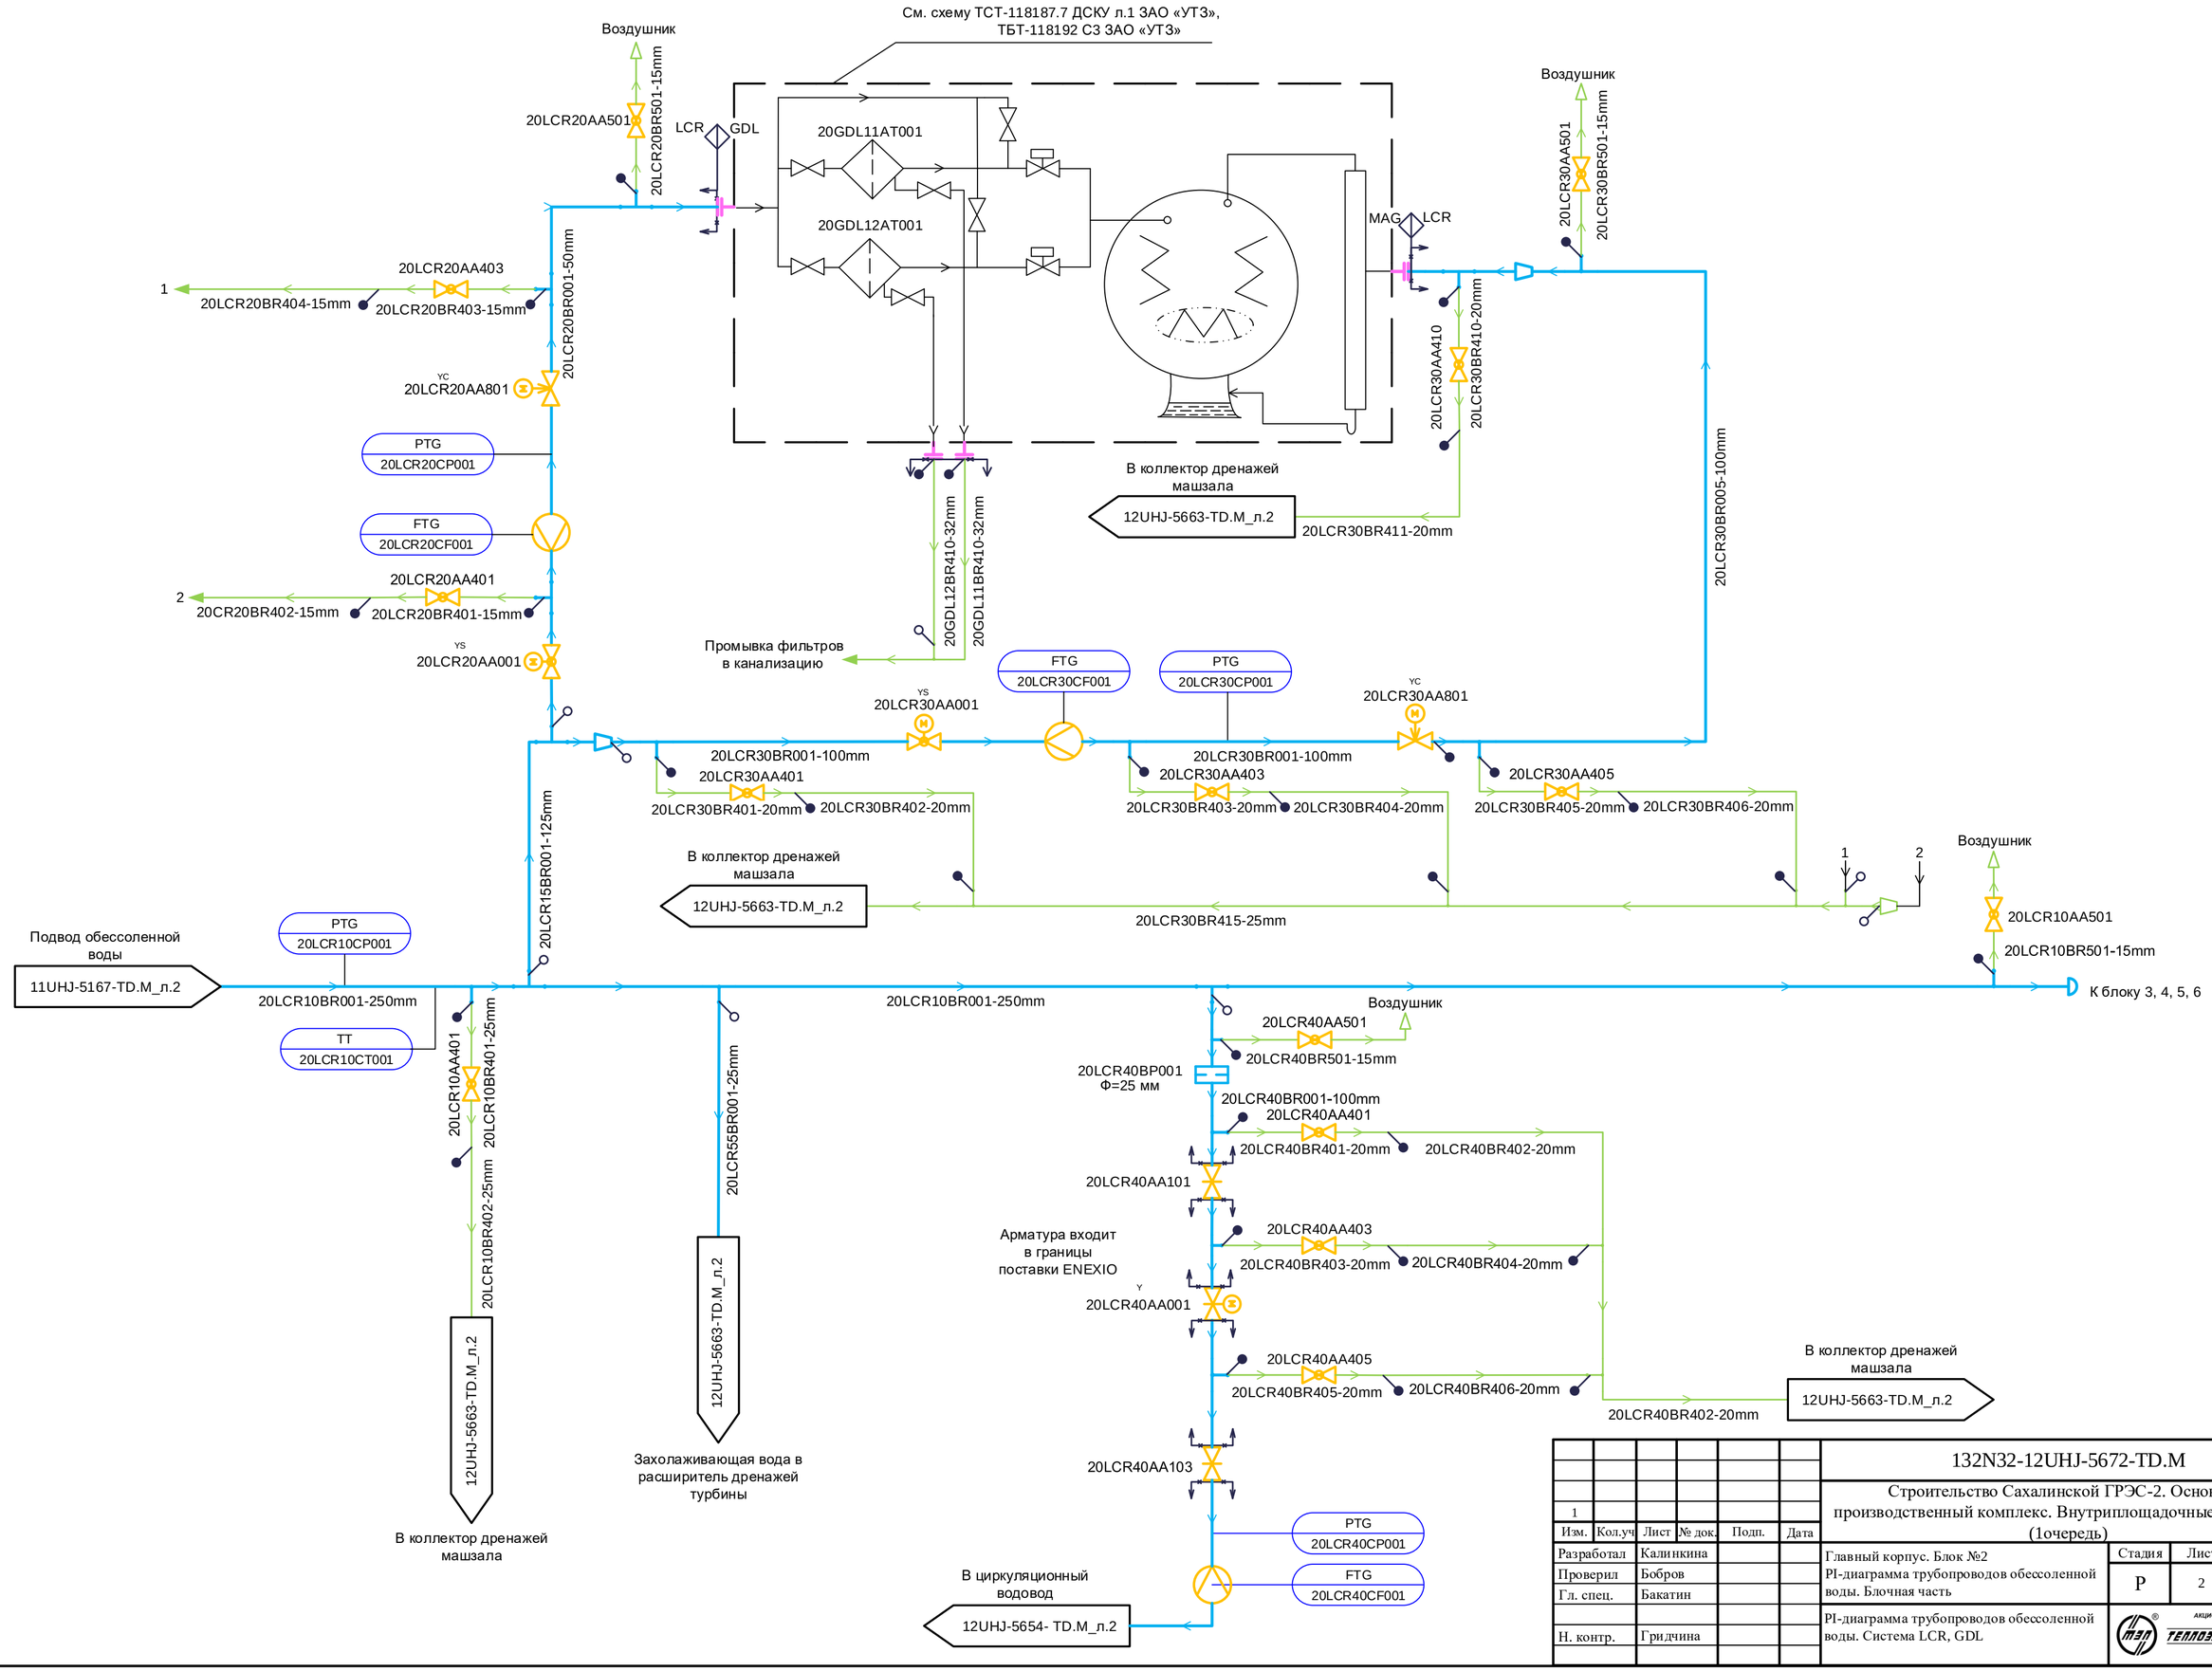

1						132N32-12UHJ-5672-TD.M
Изм.	Кол.уч	Лист	№ док.	Подп.	Дата	Строительство Сахалинской ГРЭС-2. Основной производственный комплекс. Внутриплощадочные объекты (1очередь)
Разработал		Калинкина				Главный корпус. Блок №2 PI-диаграмма трубопроводов обессоленной воды. Блочная часть
Проверил		Бобров				
Гл. спец.		Бакатин				
Н. контр.		Гридчина				PI-диаграмма трубопроводов обессоленной воды. Система LCR, GDL

Стадия	Лист	Листов
Р	2	

АКЦИОНЕРНОЕ ОБЩЕСТВО ИНСТИТУТ ТЕПЛОЭЛЕКТРОПРОЕКТ г. МОСКВА

Согласовано
ОАСУ Соболева

Взам. инв. №
Подпись и дата
Инв. № подл.

Формат А2