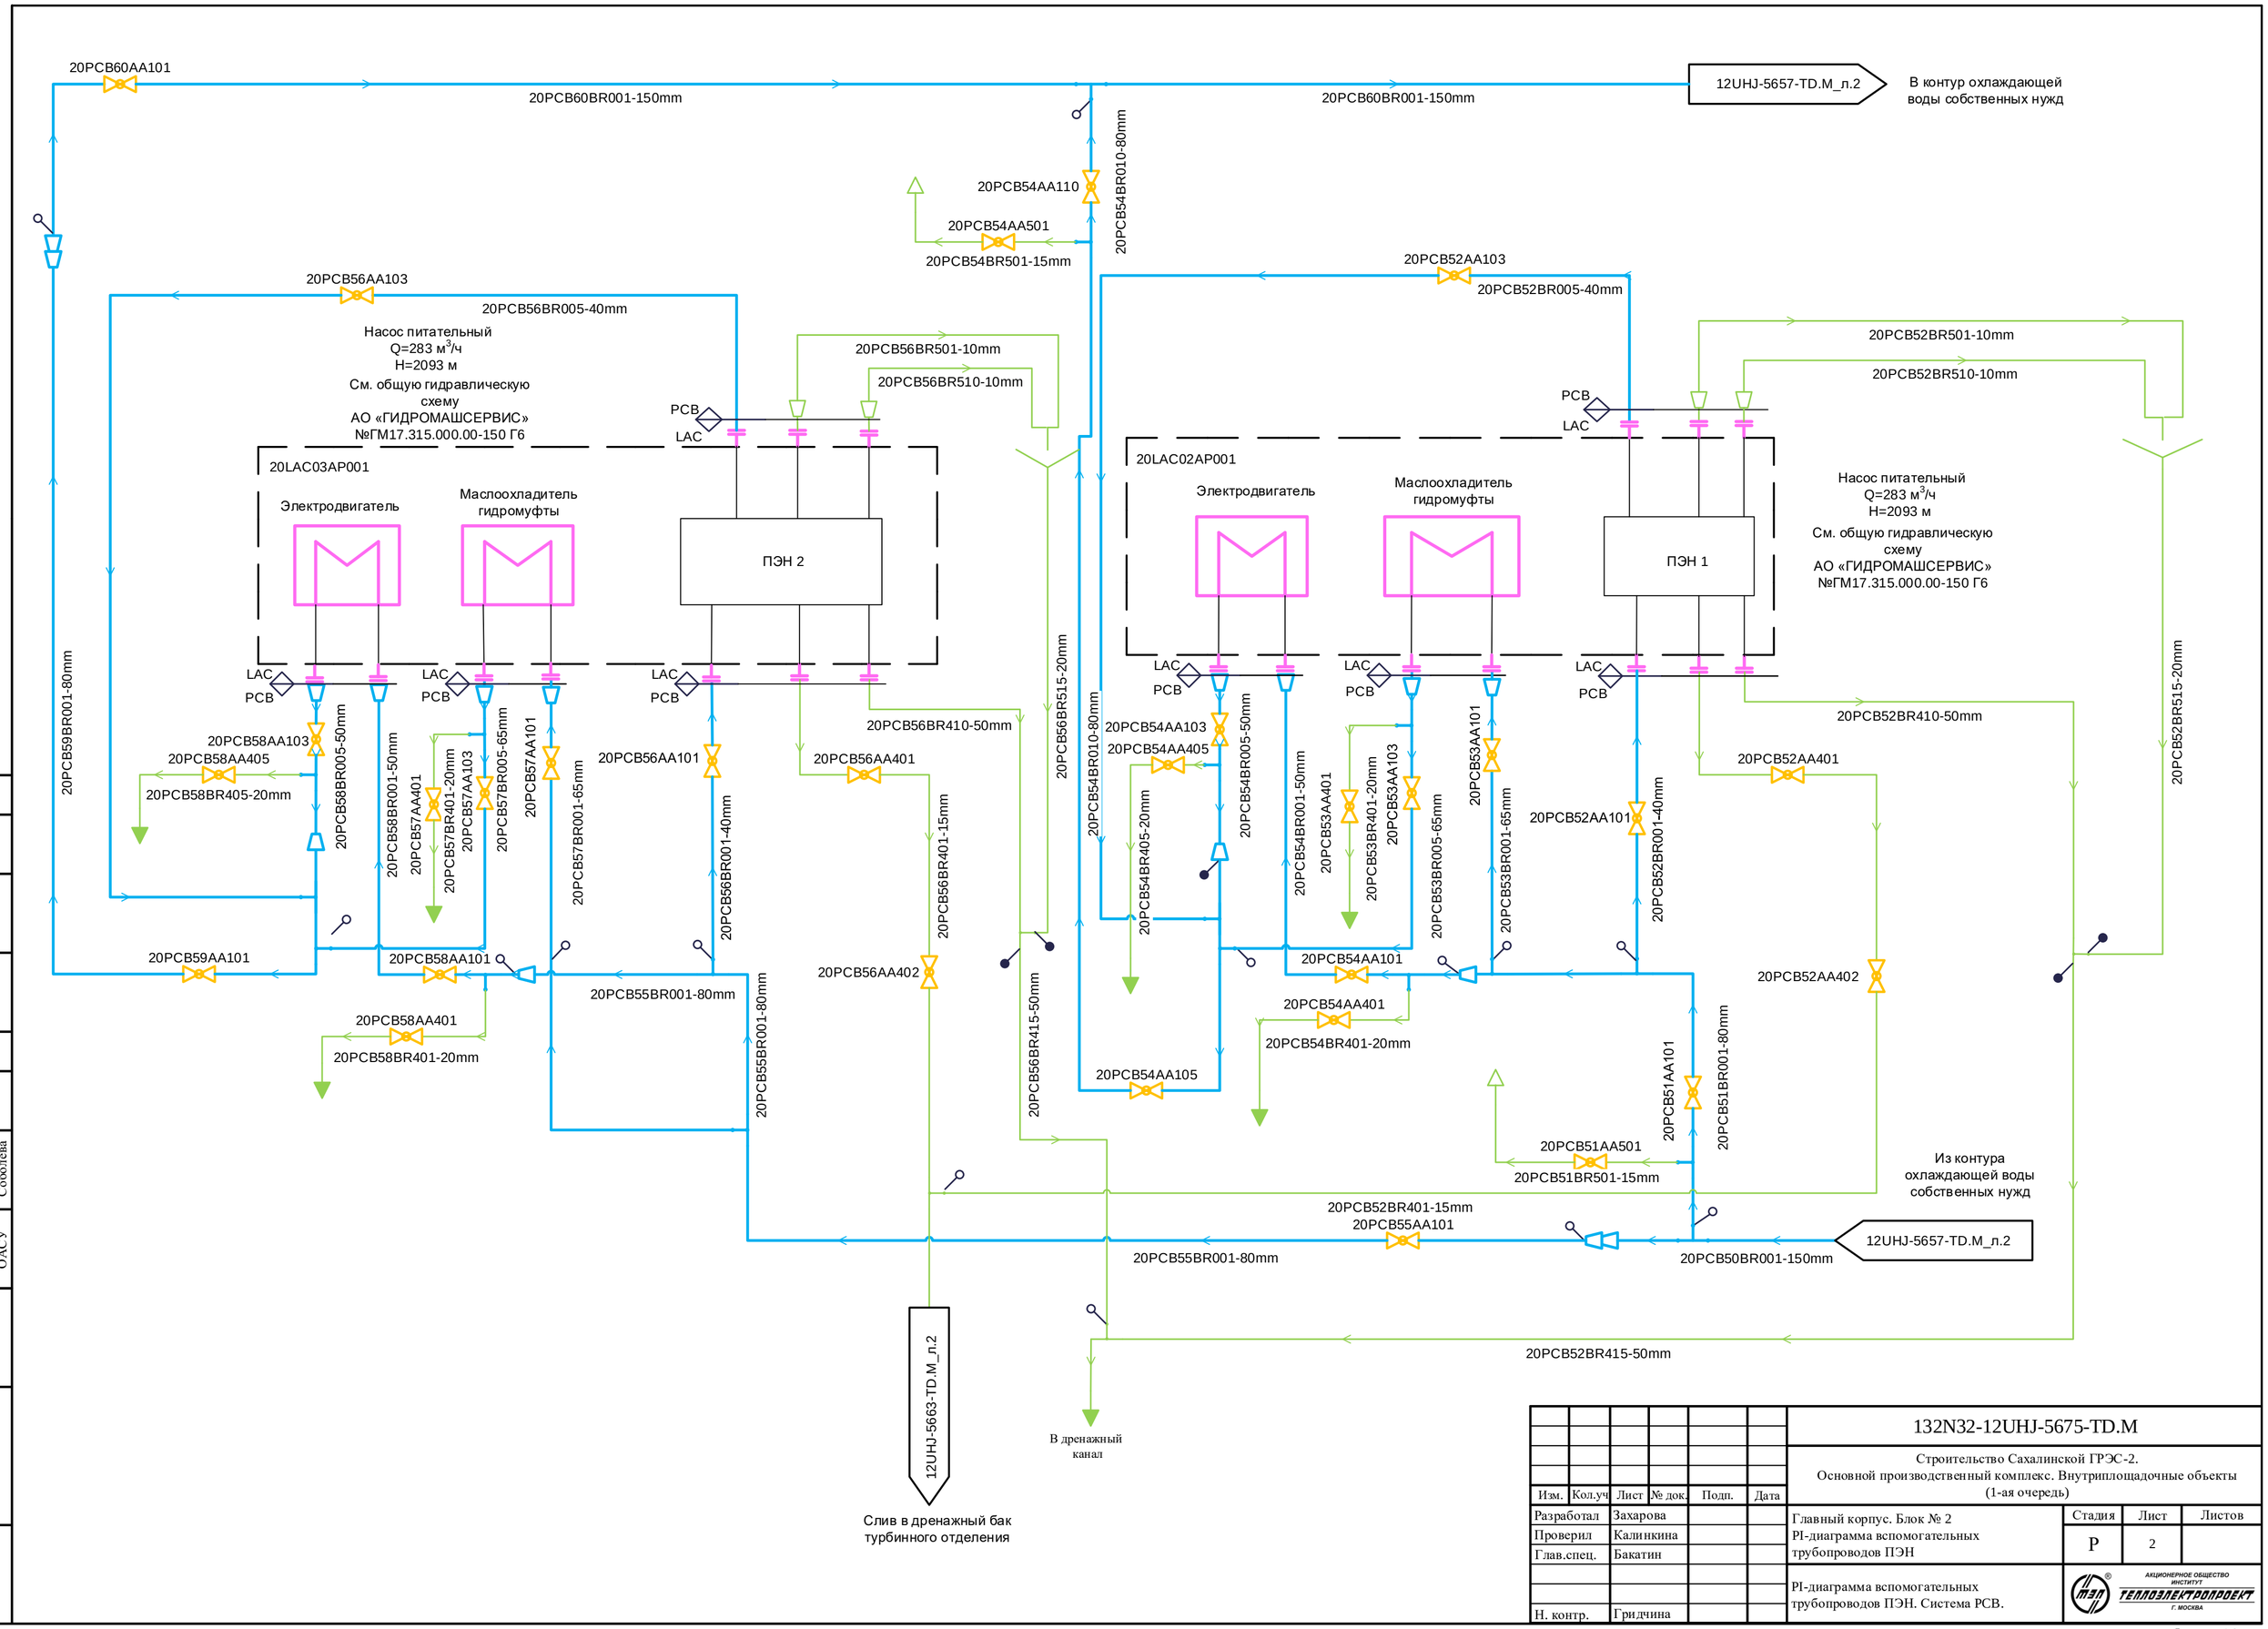

Изм.	Кол.уч	Лист	№ док.	Подп.	Дата	132N32-12UHJ-5675-TD.M
						Строительство Сахалинской ГРЭС-2. Основной производственный комплекс. Внутриплощадочные объекты (1-ая очередь)
Разработал		Захарова				Главный корпус. Блок № 2 PI-диаграмма вспомогательных трубопроводов ПЭН
Проверил		Калинкина				Стадия: Р; Лист: 2; Листов:
Глав.спец.		Бакатин				
						PI-диаграмма вспомогательных трубопроводов ПЭН. Система PCB.
Н. контр.		Гридчина				АКЦИОНЕРНОЕ ОБЩЕСТВО ИНСТИТУТ ТЕПЛОЭЛЕКТРОПРОЕКТ г. МОСКВА

Согласовано: ОАСУ, Соболева

Взам. инв. №

Подпись и дата

Инв. № подл.

Формат А2