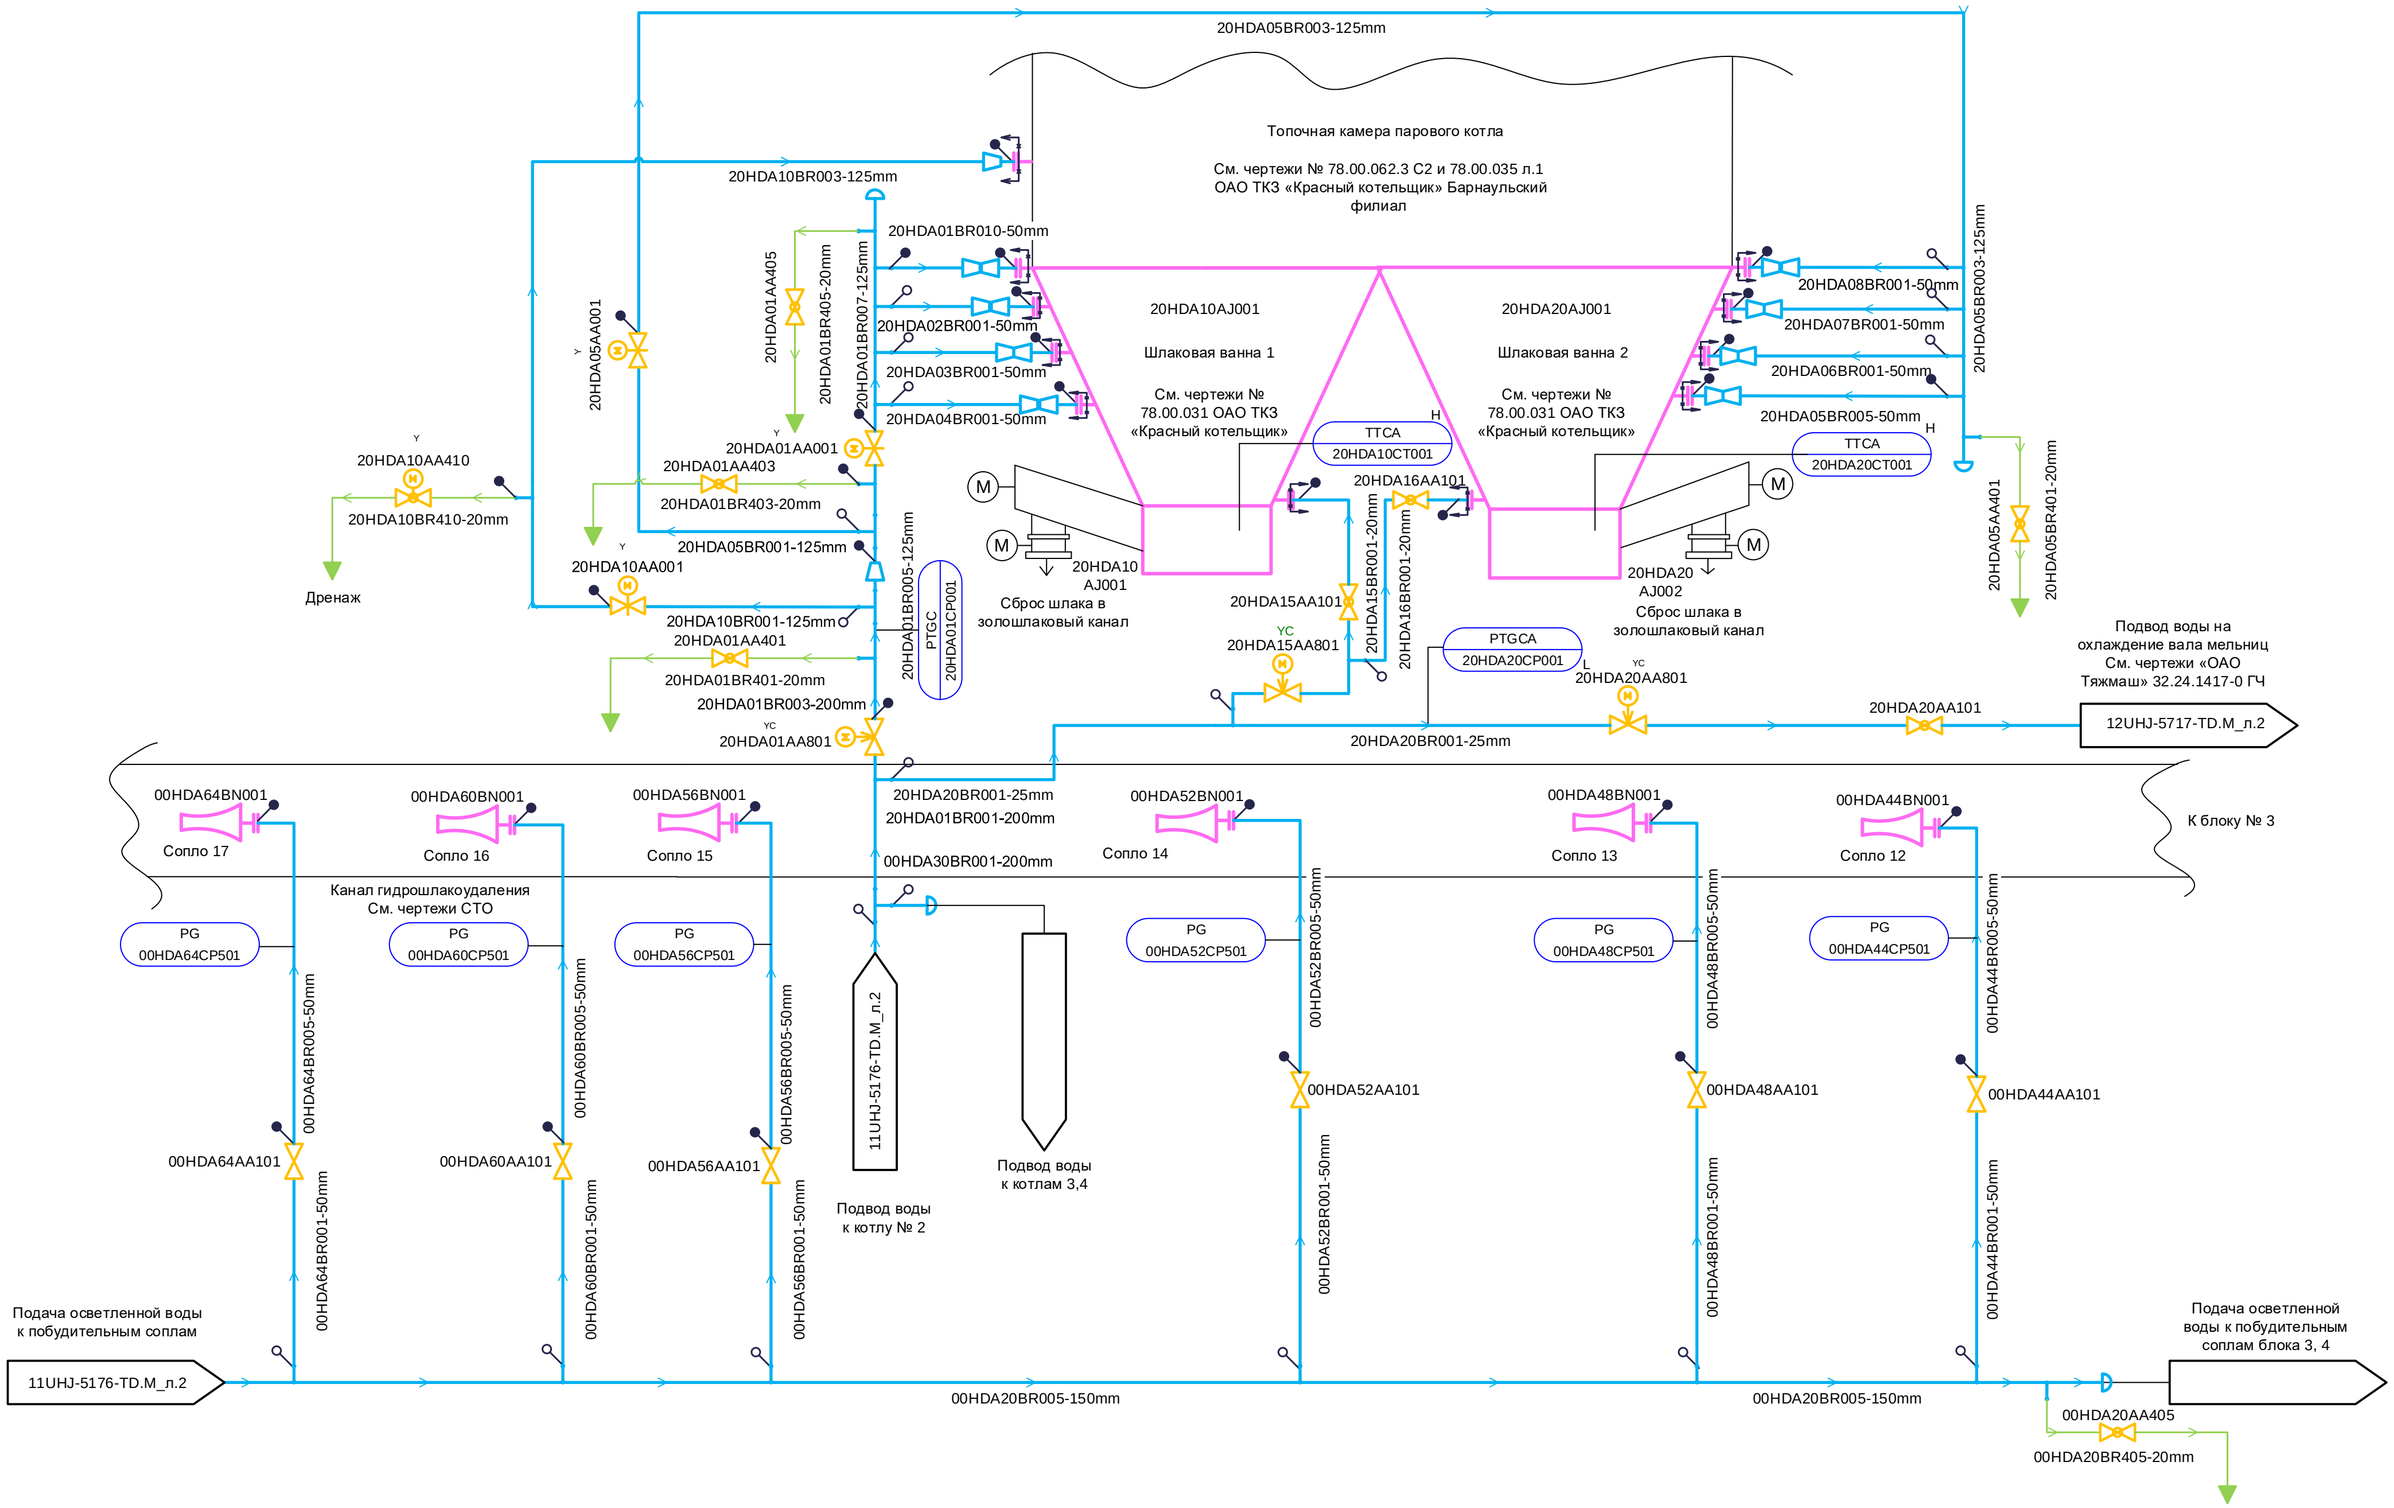

Изм.	Кол.уч	Лист	№ док.	Подп.	Дата	132N32-12UHJ-5678-TD.M
						Строительство Сахалинской ГРЭС-2. Основной производственный комплекс. Внутриплощадочные объекты (1-ая очередь)
Разработал		Захарова				Главный корпус. Блок № 2 PI-диаграмма трубопроводов гидрошлакоудаления
Проверил		Бобров				Стадия: Р; Лист: 2; Листов:
Гл.спец.		Бакатин				
Н. контр.		Гридчина				PI-диаграмма трубопроводов гидрошлакоудаления. Система HDA.

АКЦИОНЕРНОЕ ОБЩЕСТВО ИНСТИТУТ ТЕПЛОЭЛЕКТРОПРОЕКТ Г. МОСКВА

Согласовано: ОАСУ Соболева

Взам. инв. №

Подпись и дата

Инв. № подл.

Формат А2