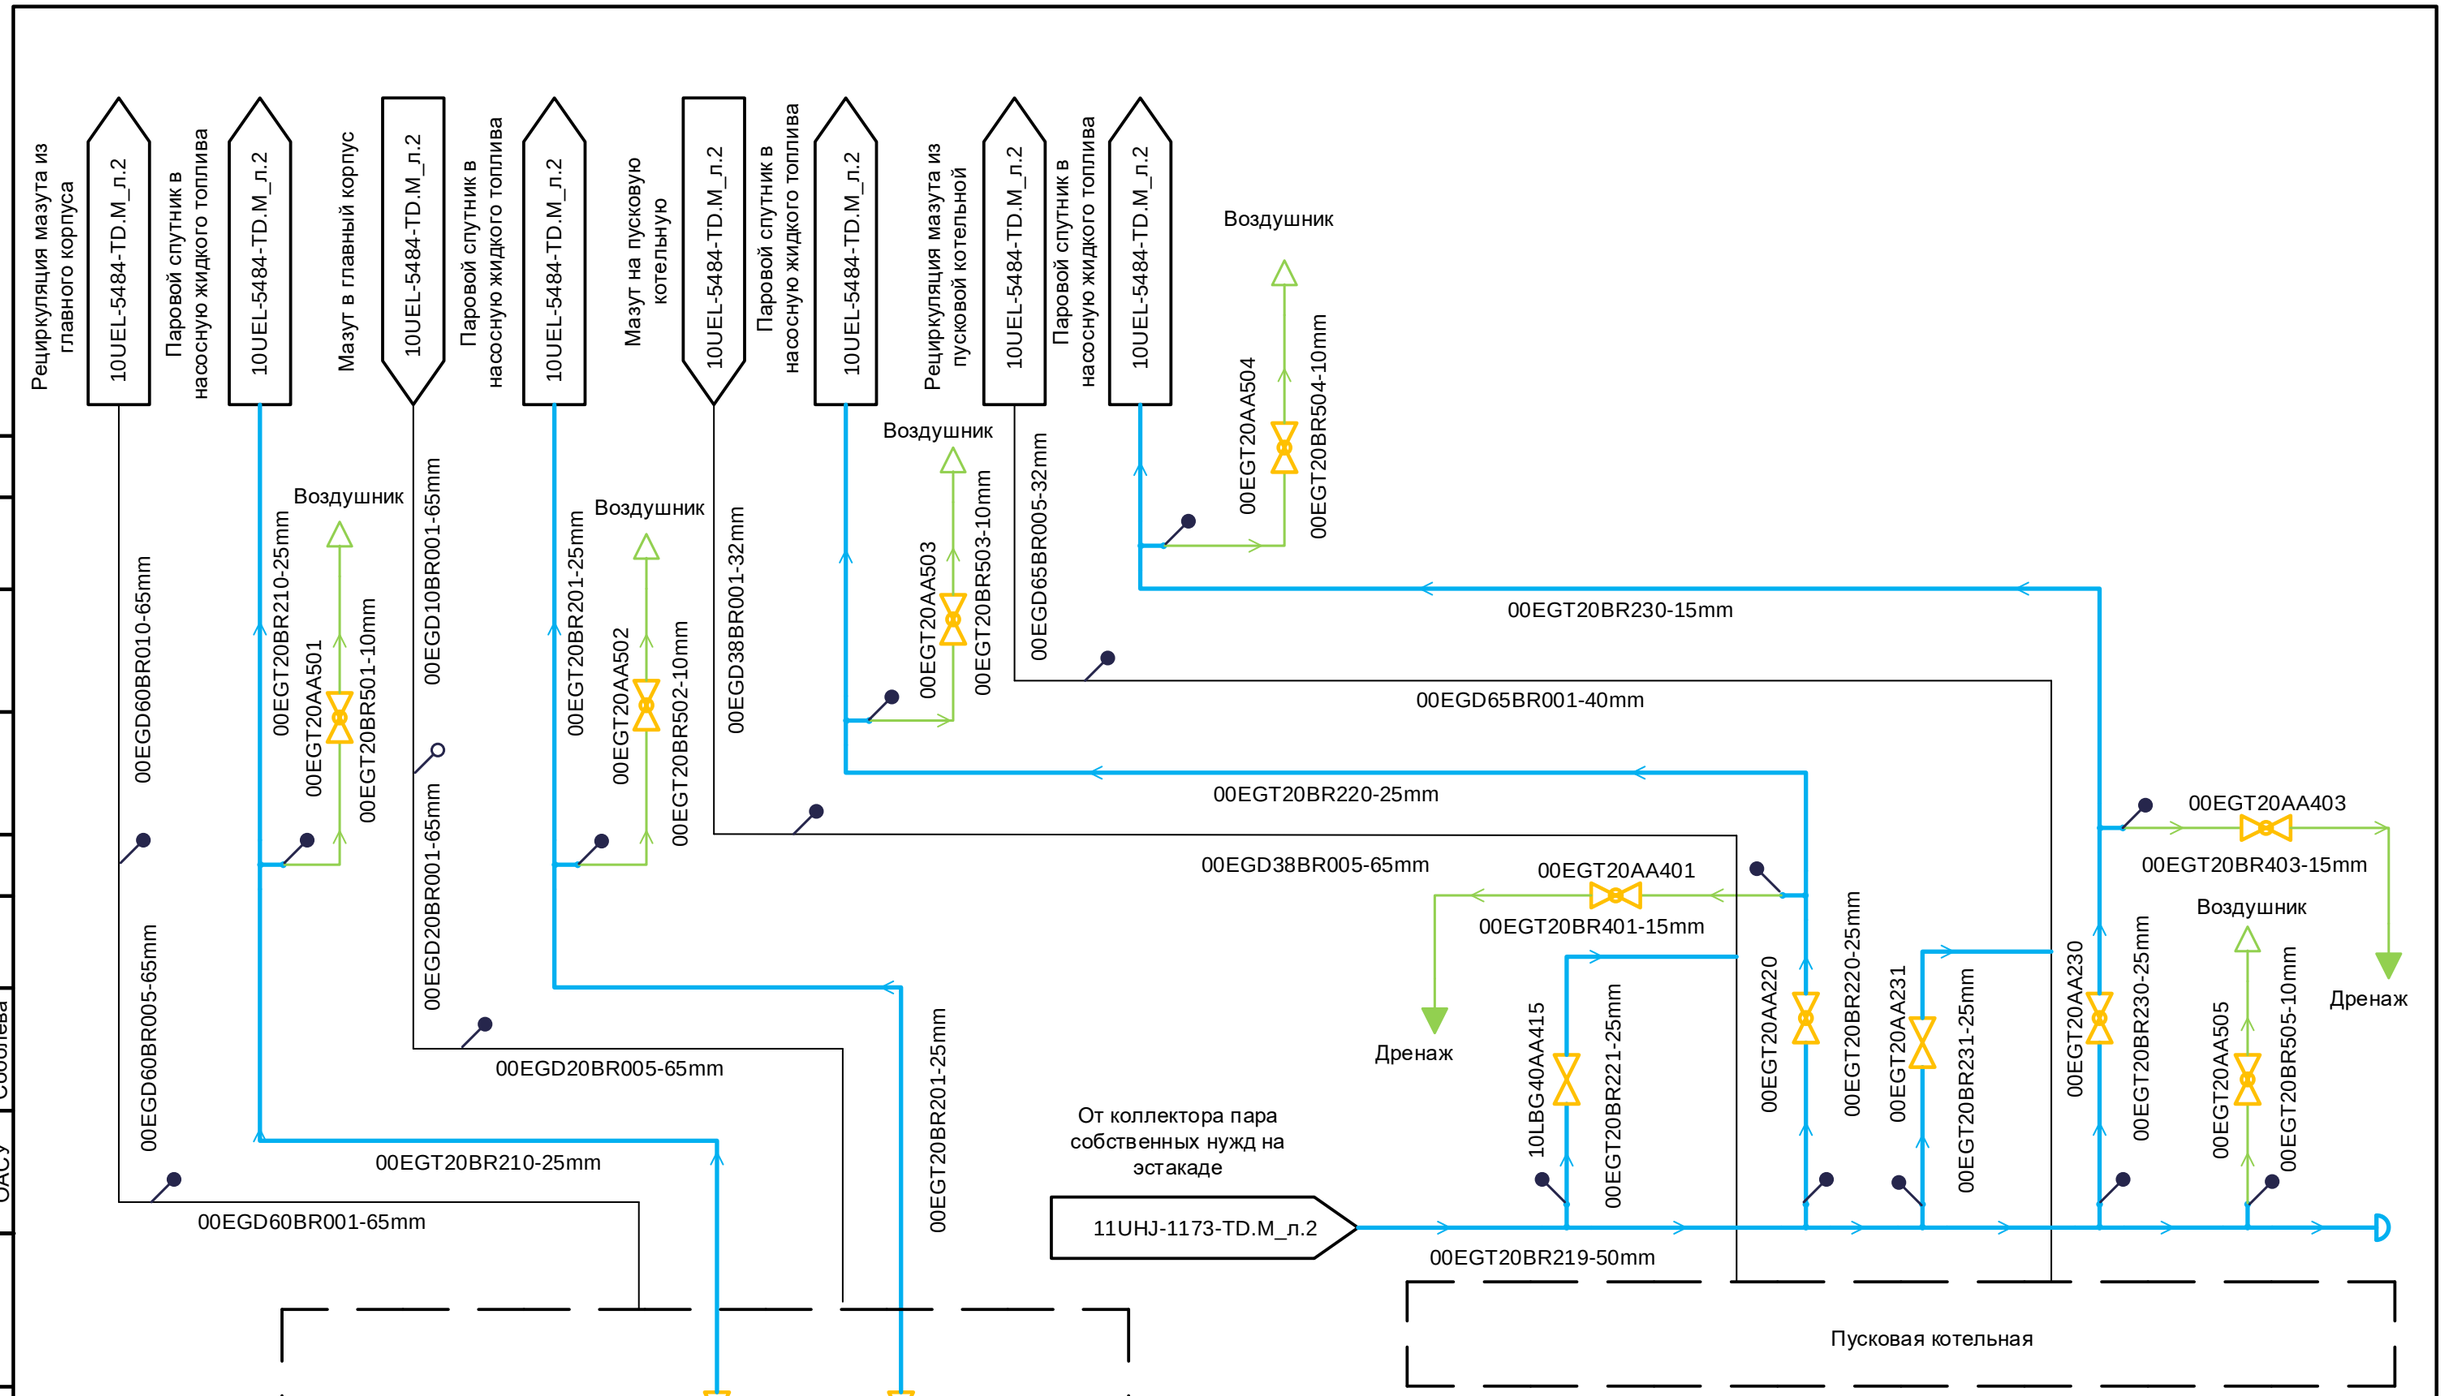

2	-	Зам.				132N32 – 10UTZ – 5691 – TD.M
Изм.	Кол.уч	Лист	№ док.	Подп.	Дата	Строительство Сахалинской ГРЭС-2. Основной производственный комплекс. Внутриплощадочные объекты (1-ая очередь)
Разработал		Захарова				Эстакады технологических трубопроводов PI-диаграмма трубопроводов парового спутникового обогрева на эстакаде.
Проверил		Калинкина				Стадия: Р; Лист: 2; Листов:
Гл.спец.		Бакатин				
Н. контр.		Черемушкина				PI-диаграмма трубопроводов парового спутникового обогрева на эстакаде. Система EGT

АКЦИОНЕРНОЕ ОБЩЕСТВО ИНСТИТУТ ТЕПЛОЭЛЕКТРОПРОЕКТ Г. МОСКВА

Согласовано: Соболева; ОАСУ

Взам. инв. №

Подпись и дата

Инв. № подл.

Формат А3